EW1 L1-2-3-4

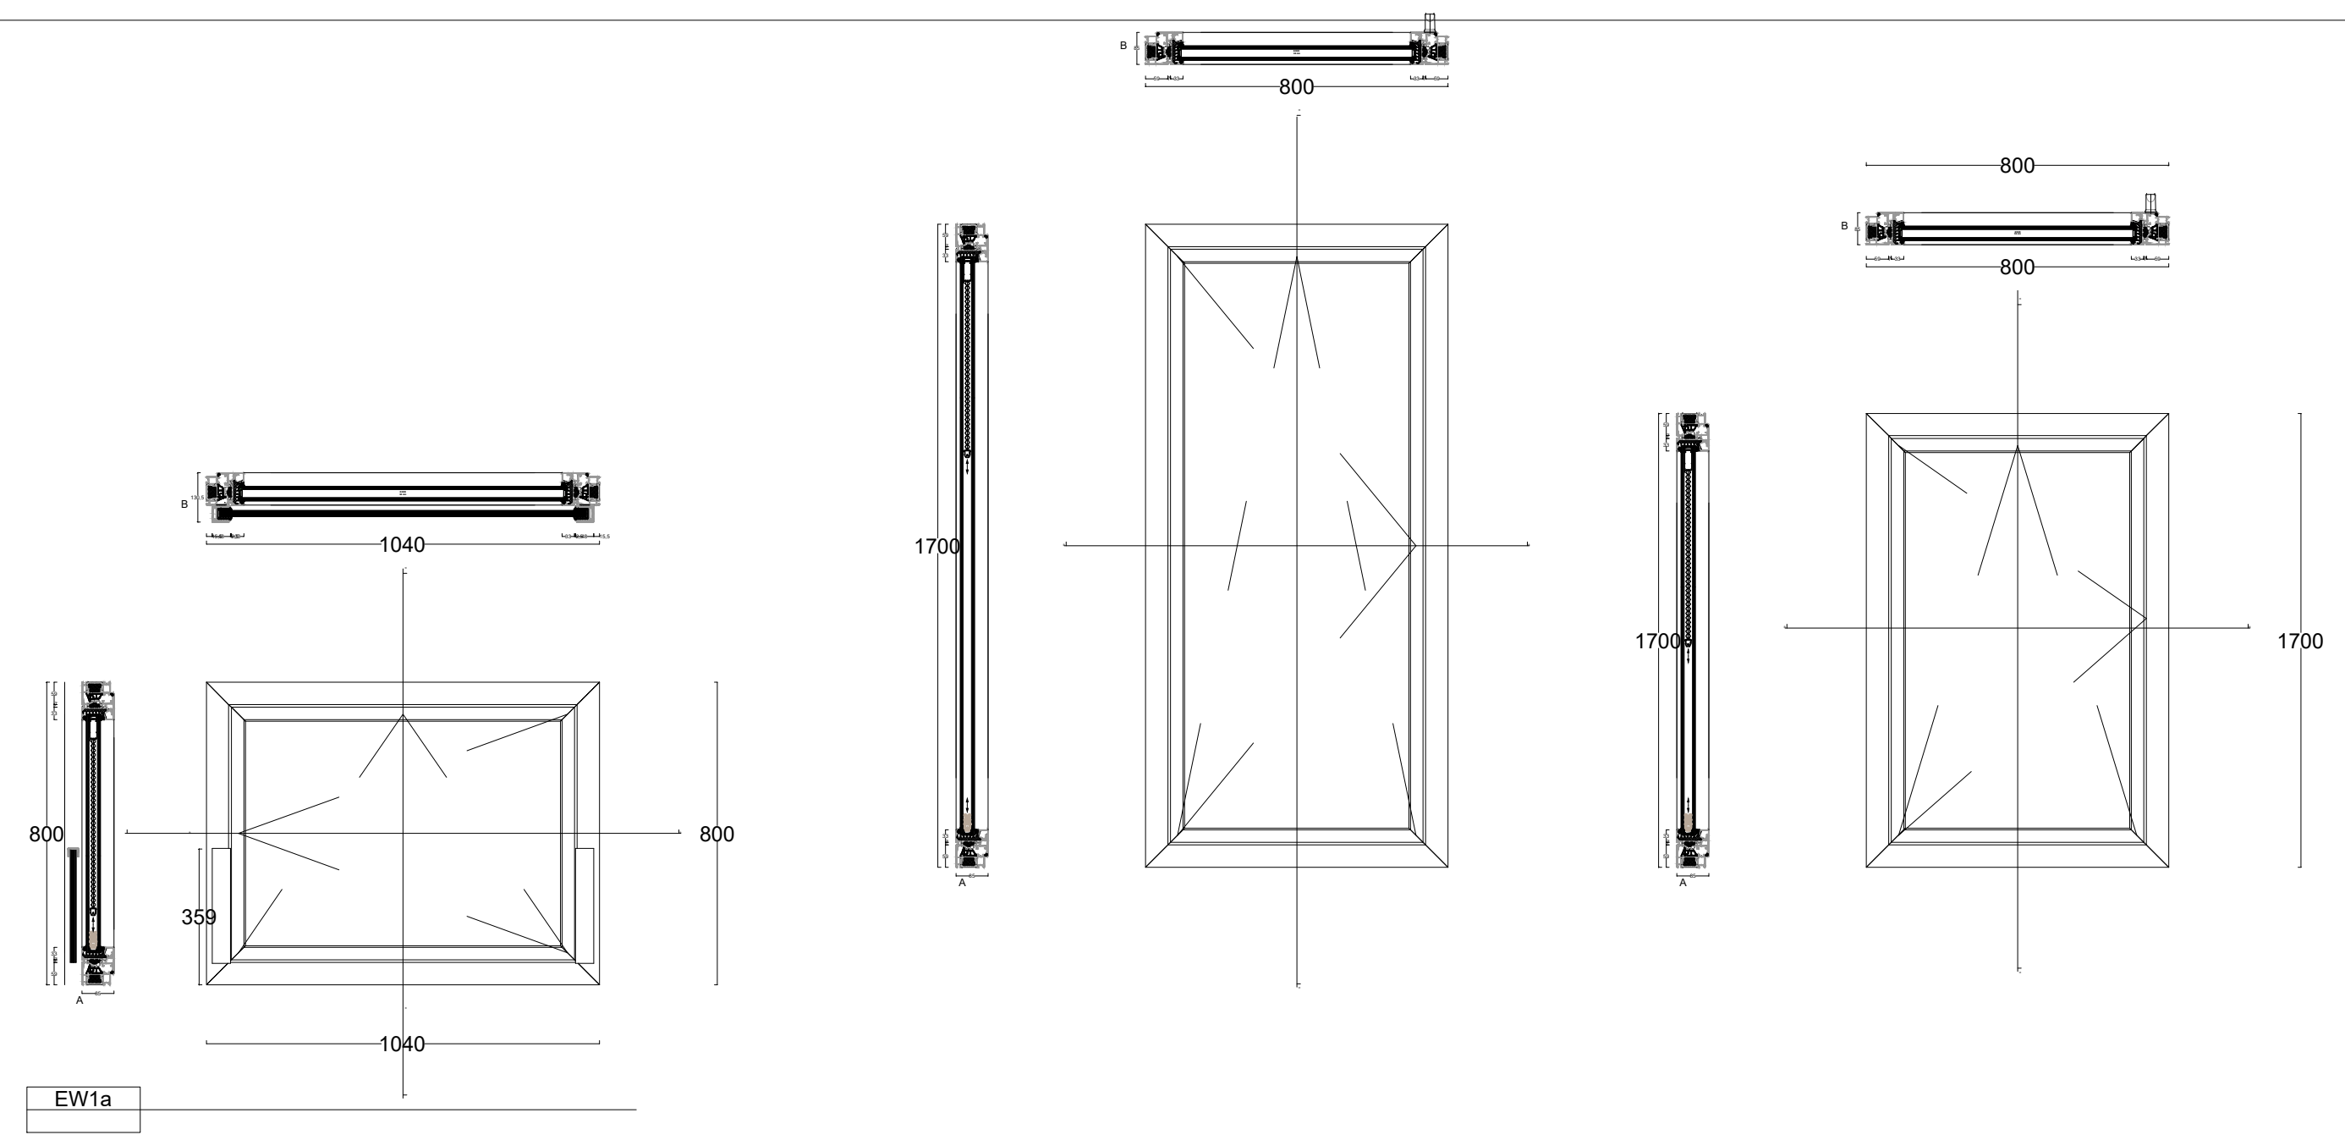

EW1a

CODICE	EW1a
TIPOLOGIA	APRIBILE ANTA RIBALTA
POSIZIONE	PIANO L1,L2, L3,L4,L5 CAMERE
SERRAMENTO	ALLUMINIO TAGLIO TERMICO UW 1.2
VETRO	STRATIFICATO 66.2+20 ARGON 90%+66.2 (interposto PVB 0.76)
CARATTERISTICHE	
DOTAZIONI	PARAPETTO IN CRISTALLO

EW2

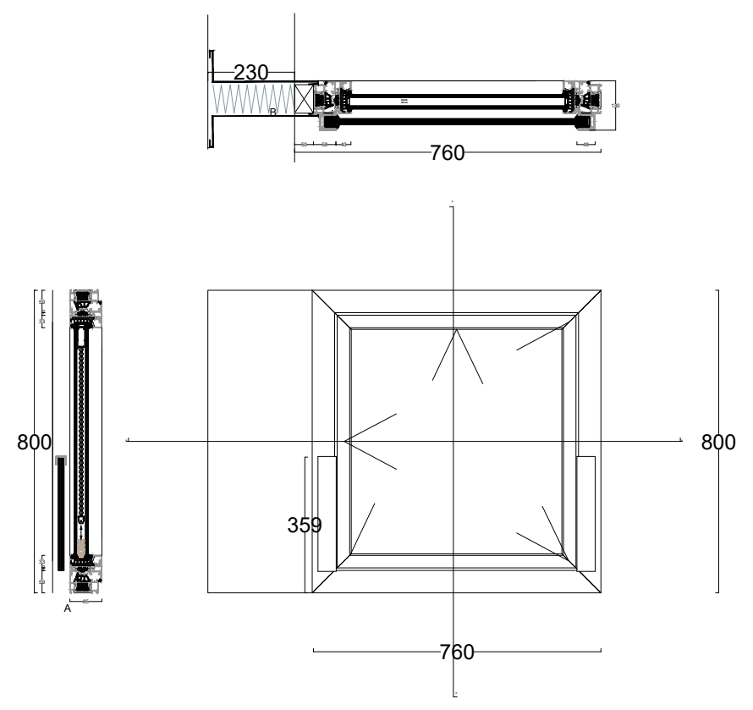

EW3

Serramento
Schuco AWS 75.SI+

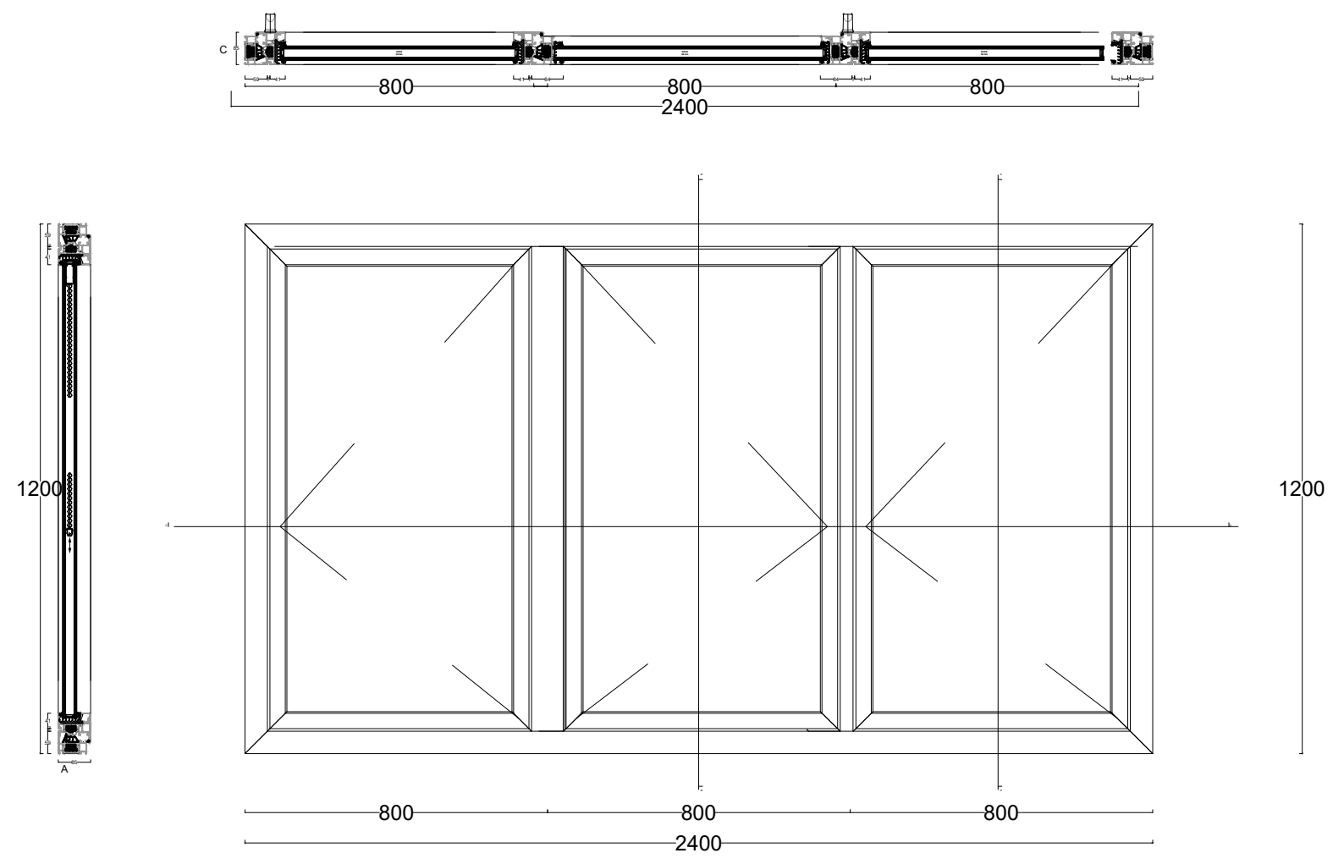

EW5

Serramento fisso EI60
Schuco ADS 80 FR 60
(vetro Contraflam EI 60 (EN 13501-2)

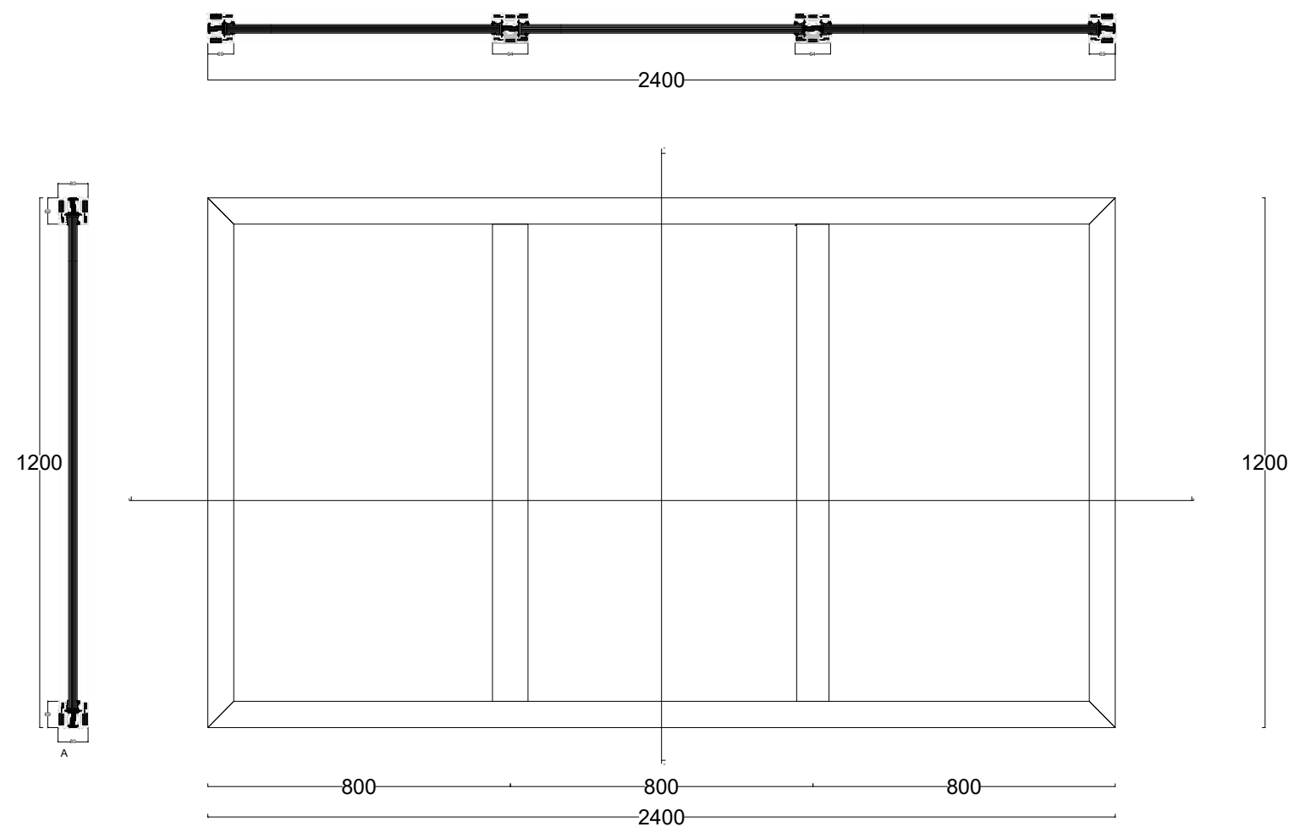

EW6-L0

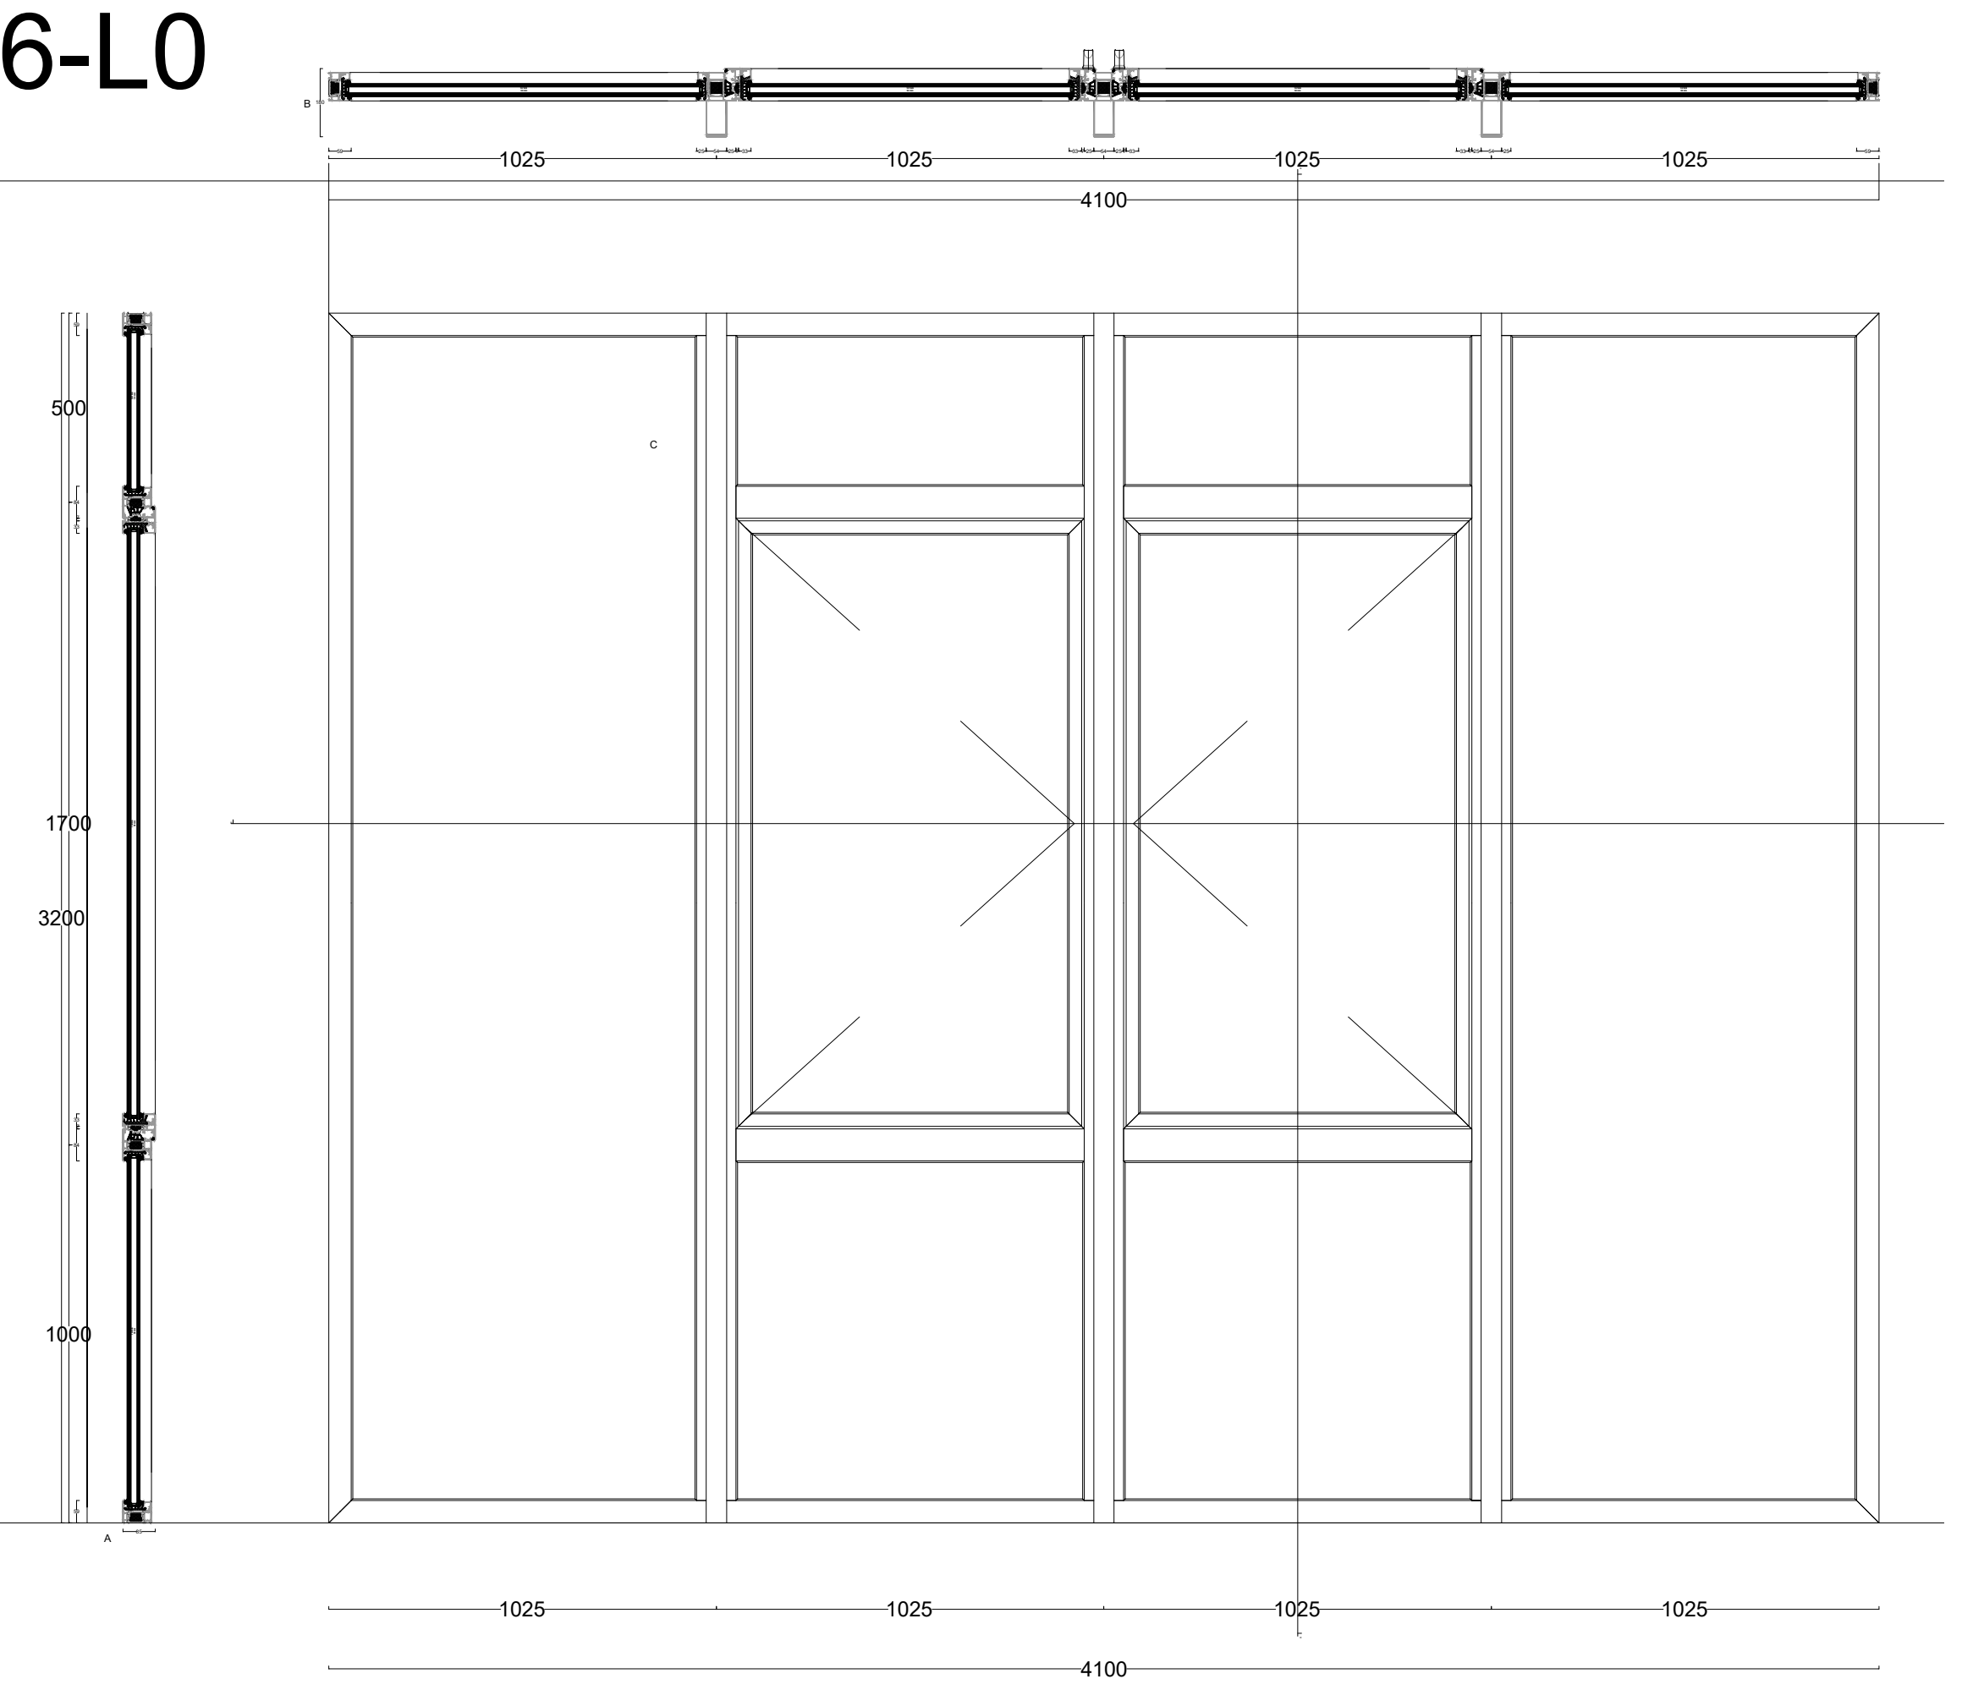

EW3L

EW9

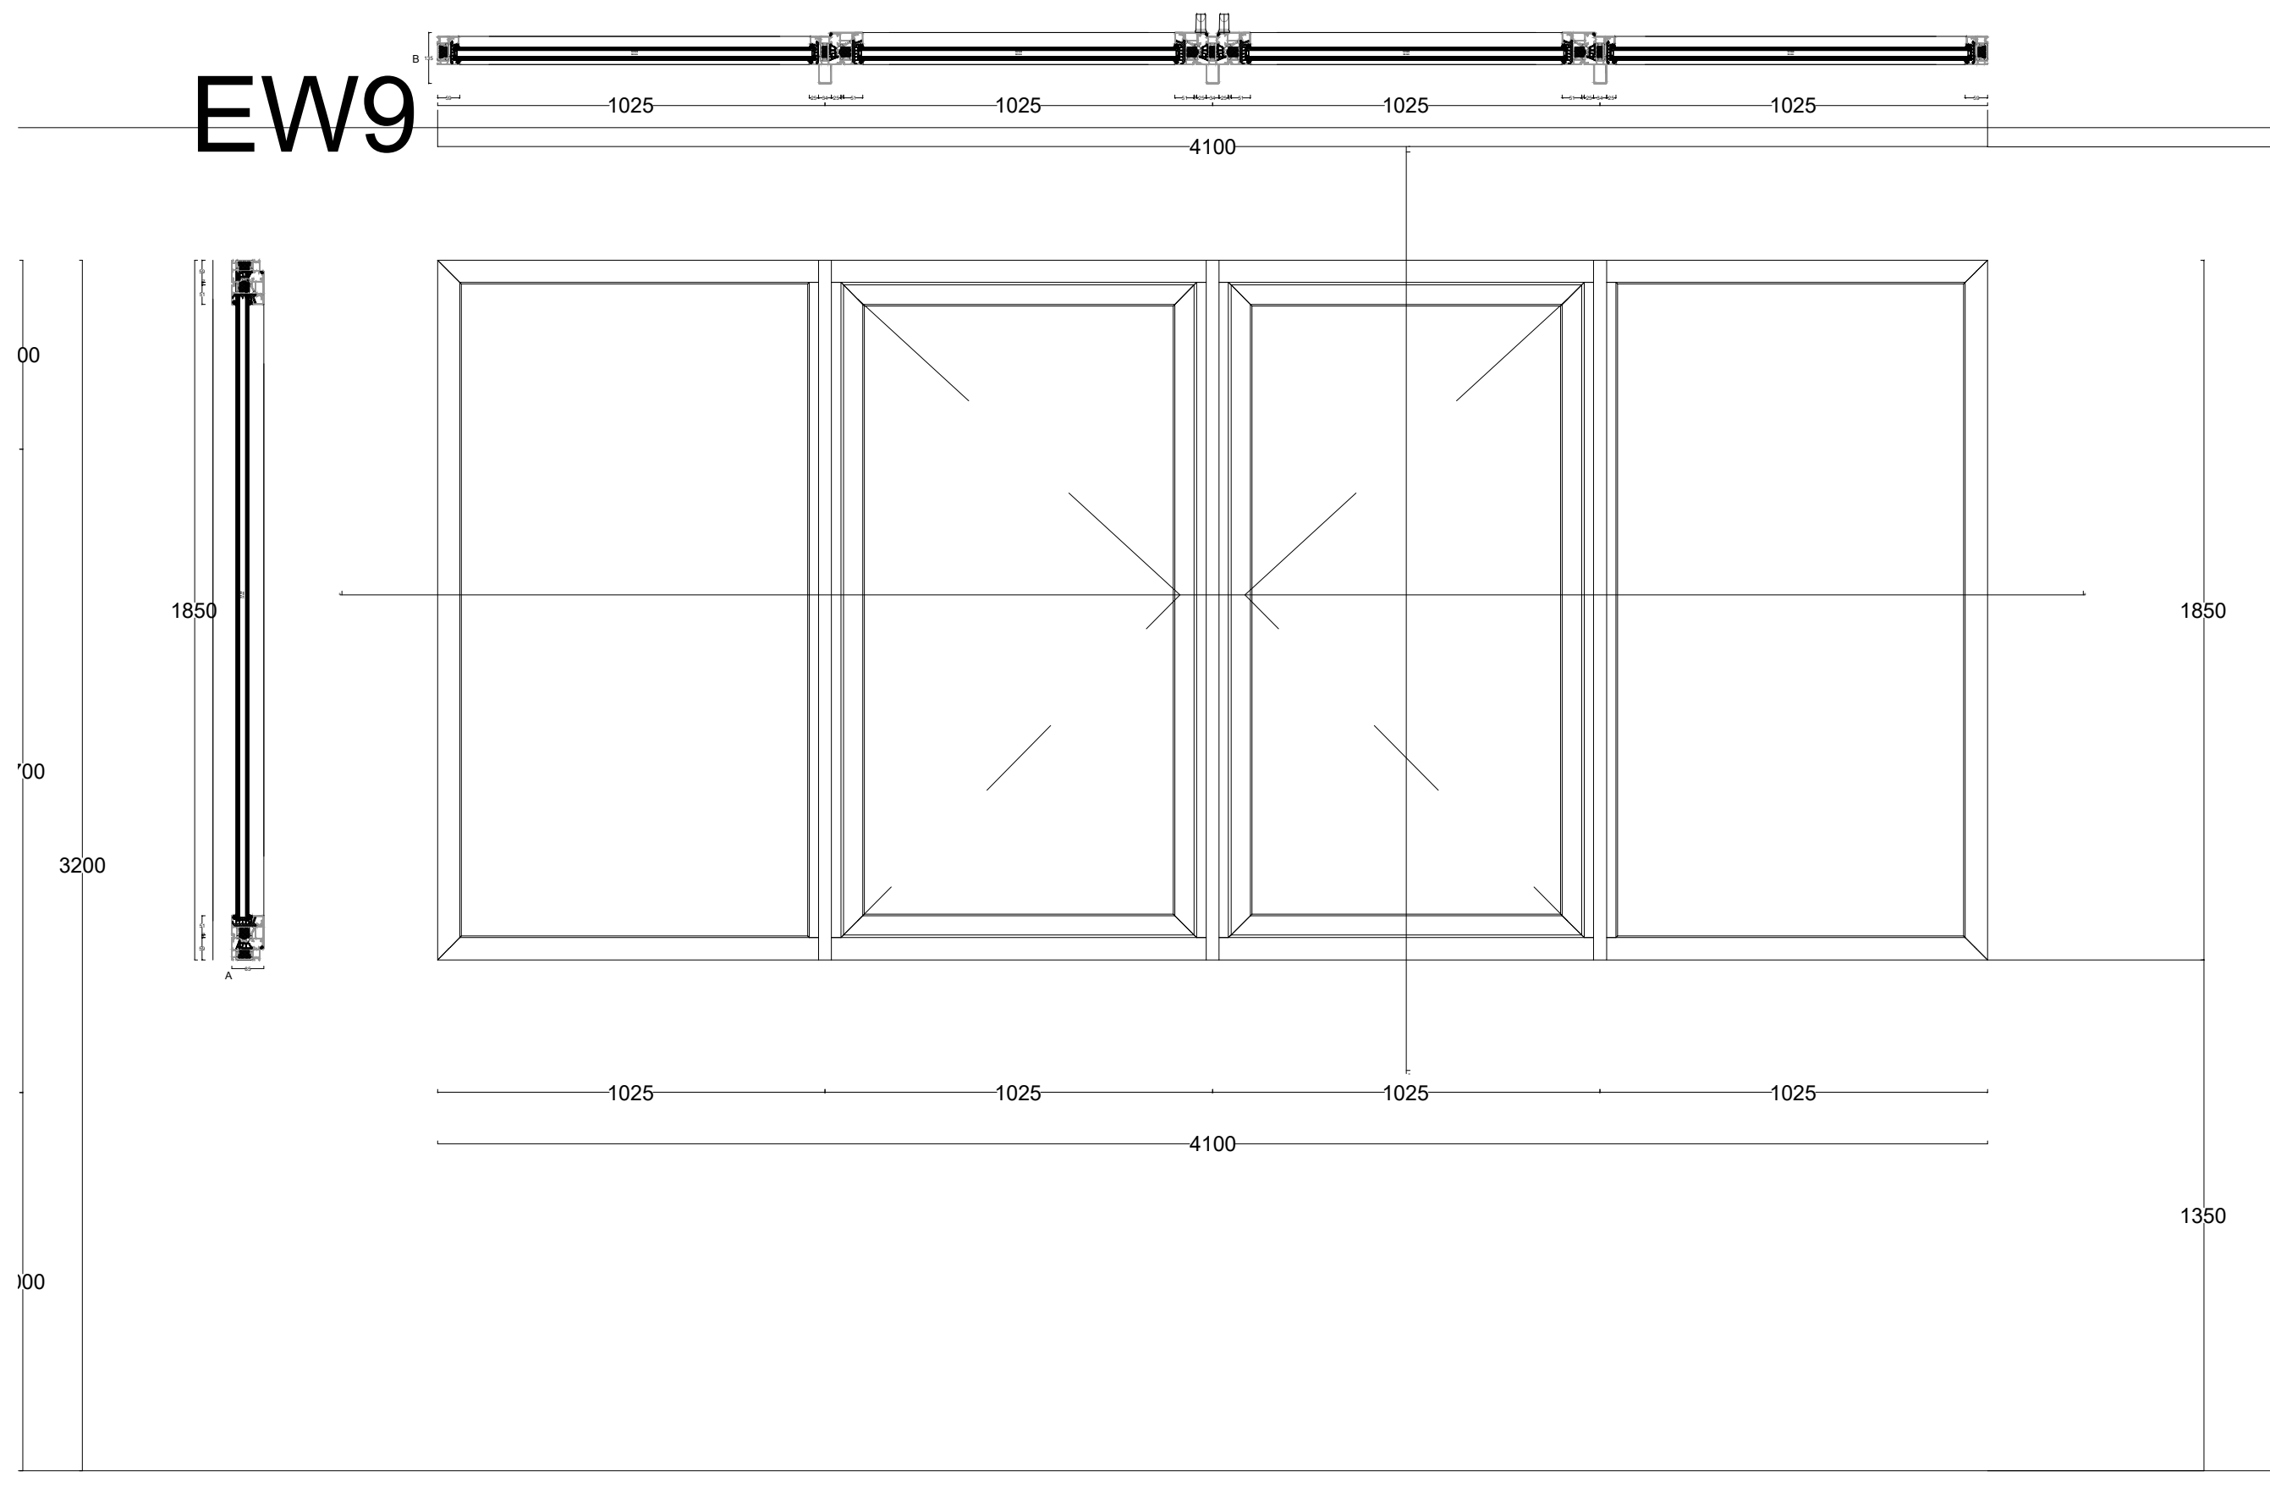

EW10

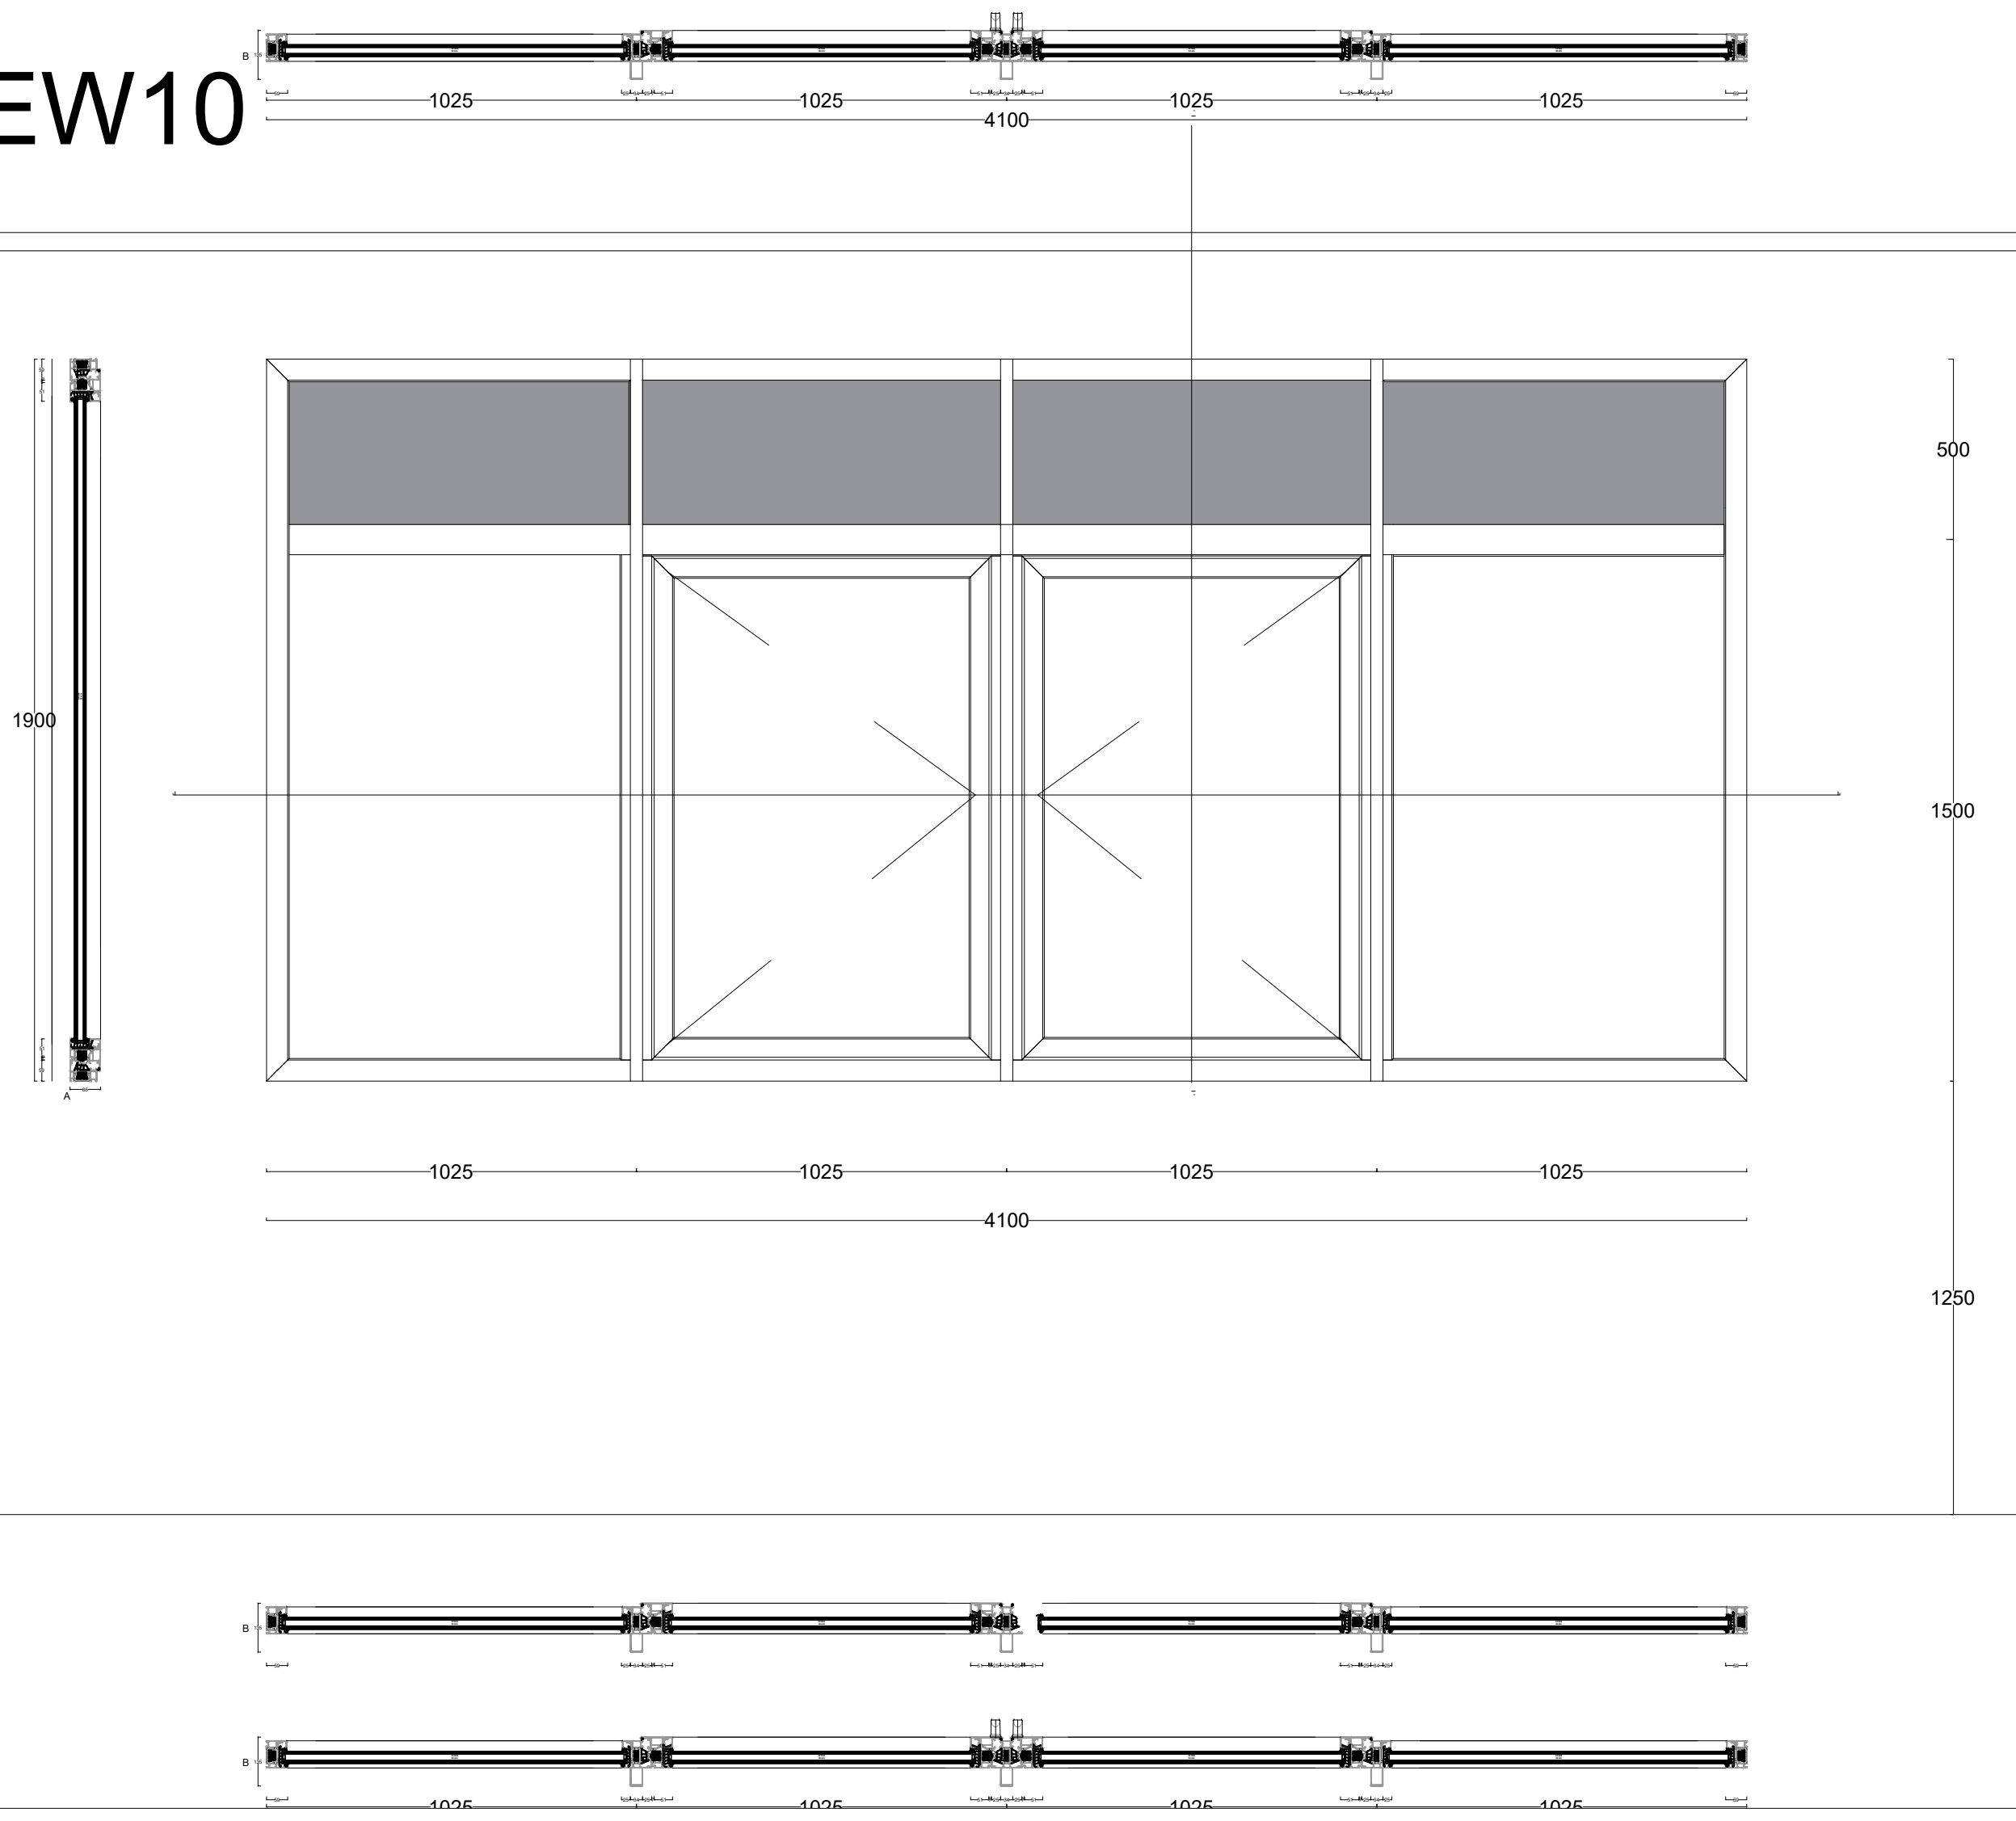

EW11

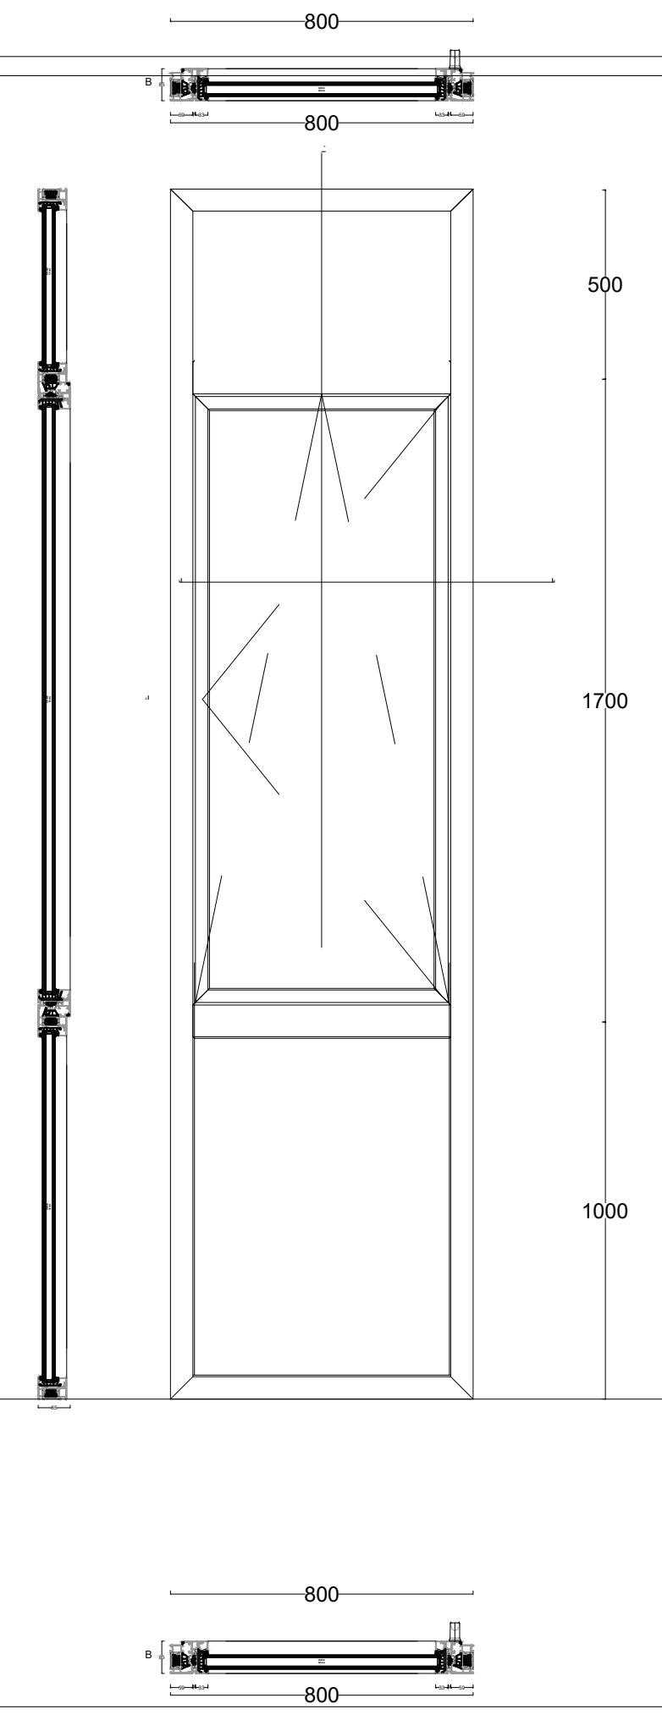

EW12

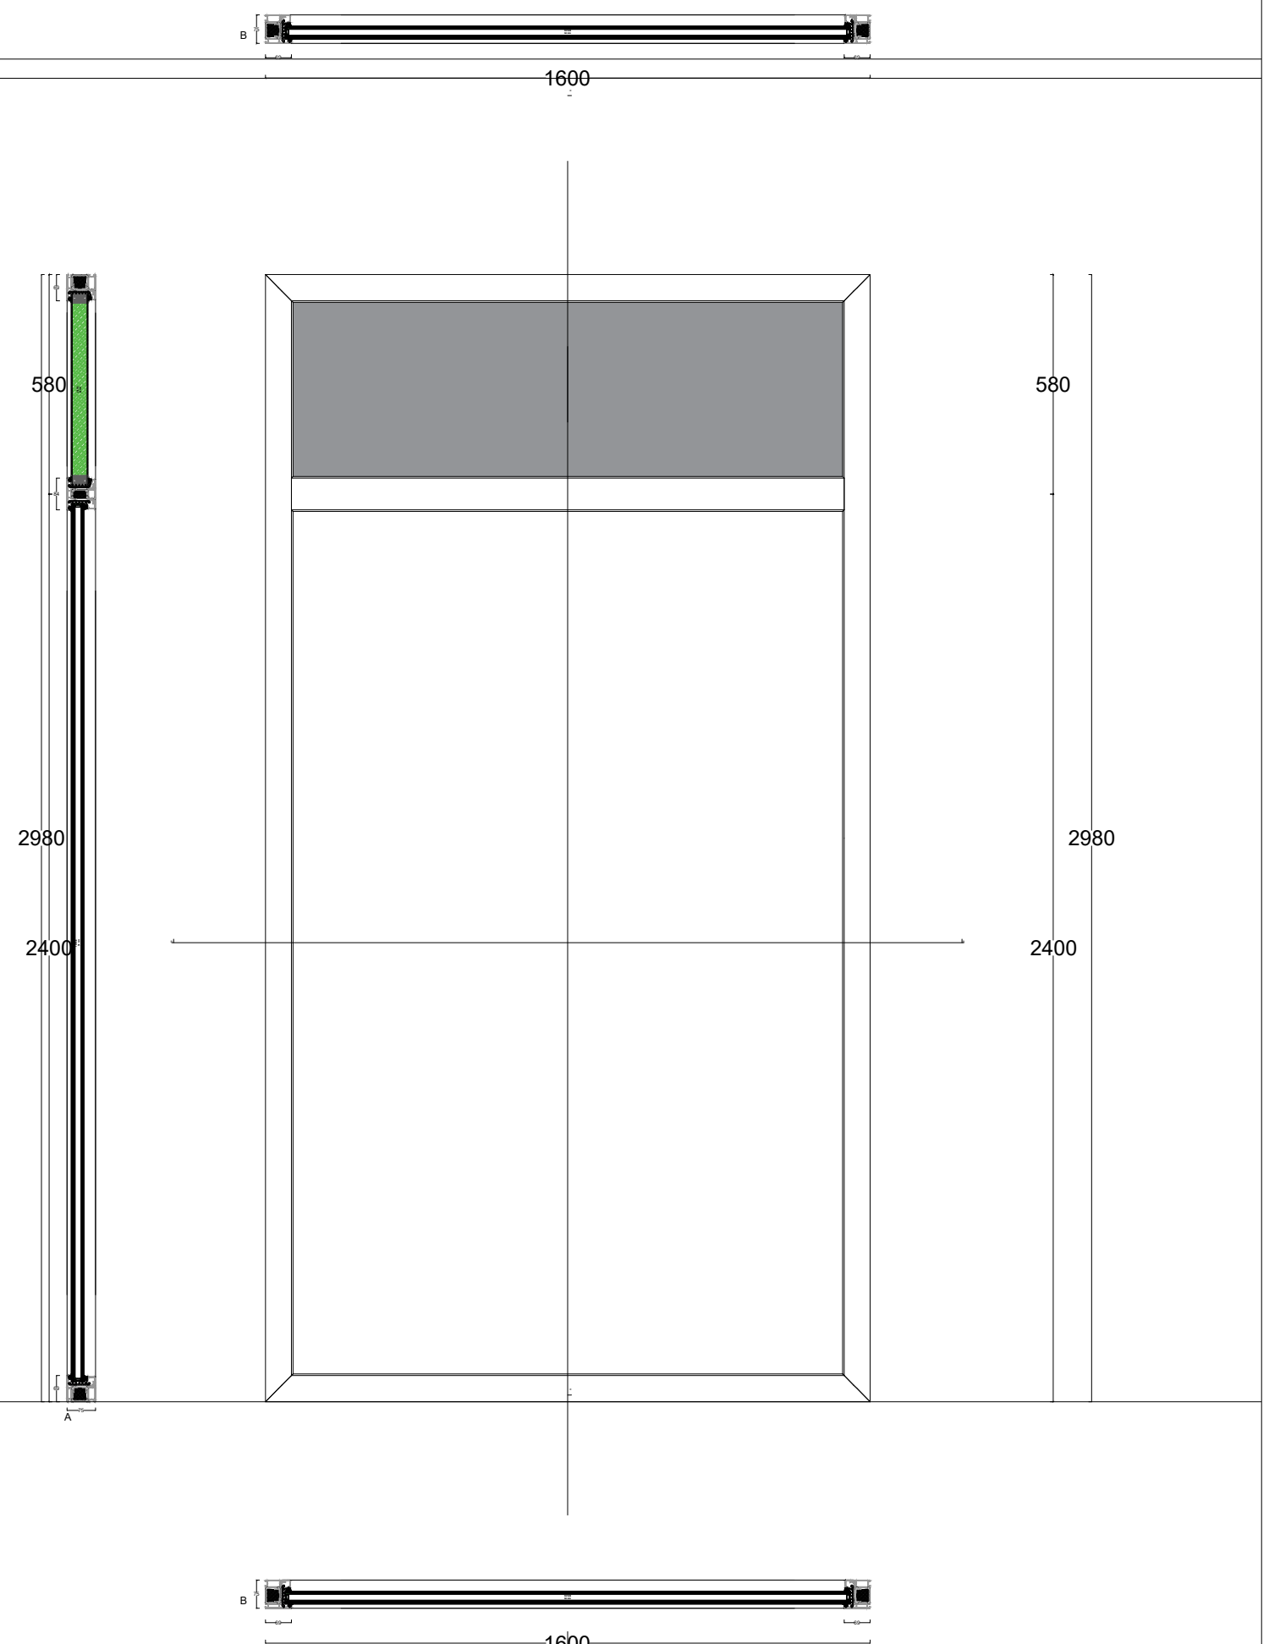

EW 13

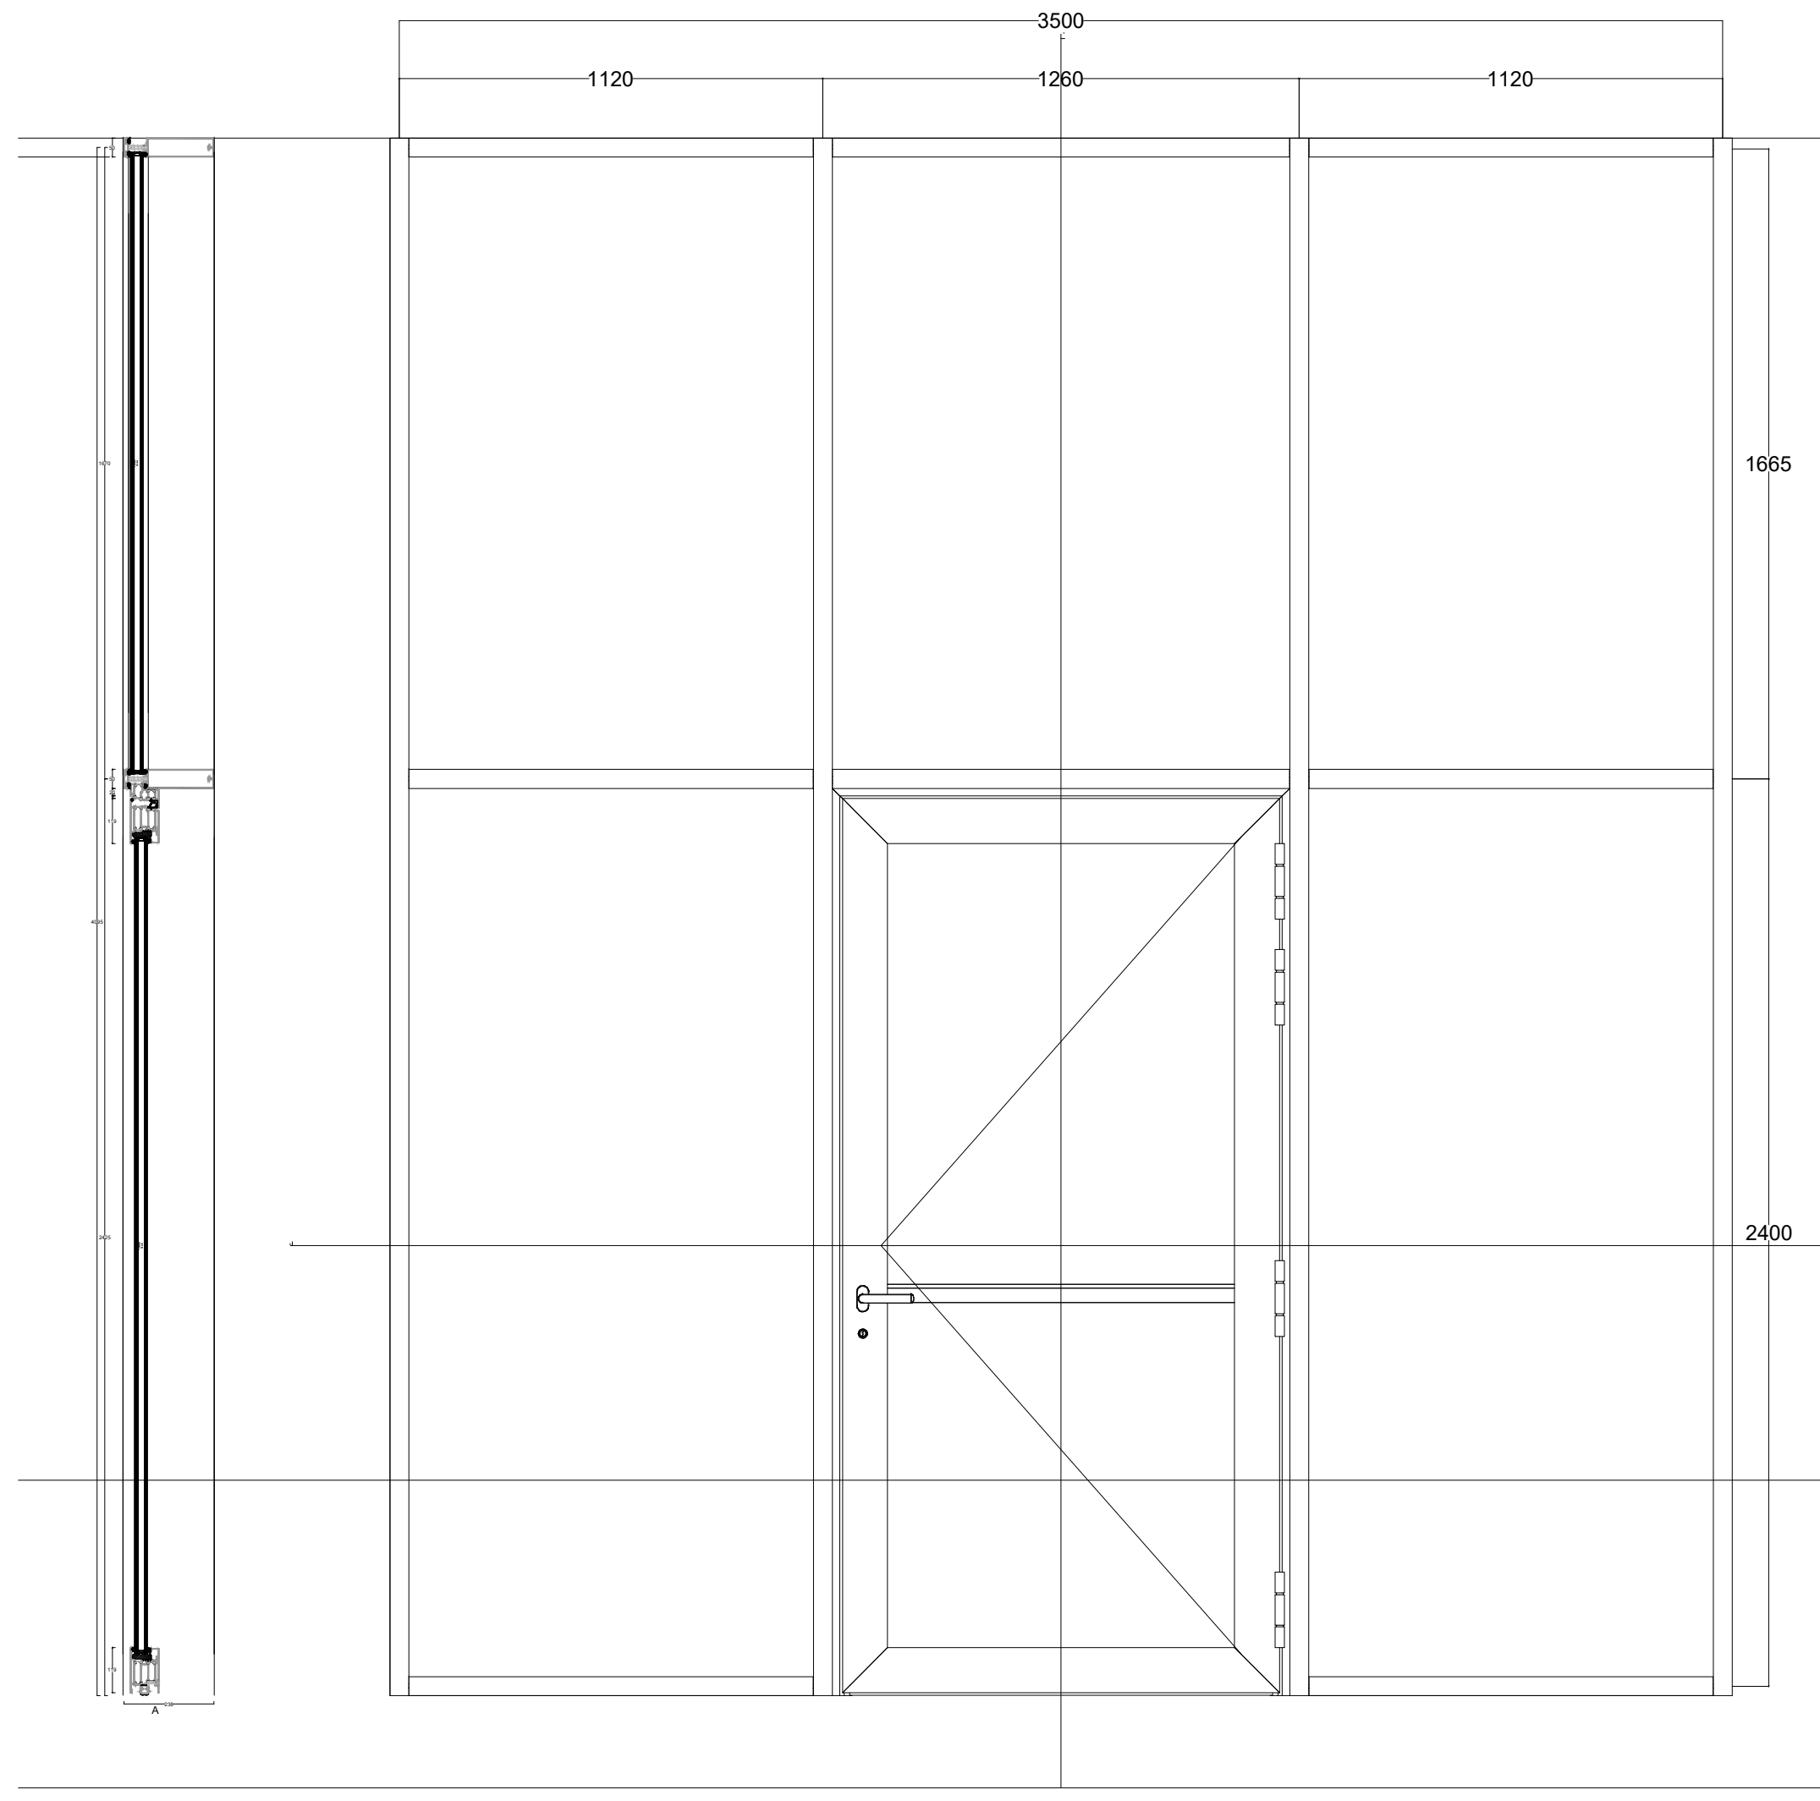

EW 14

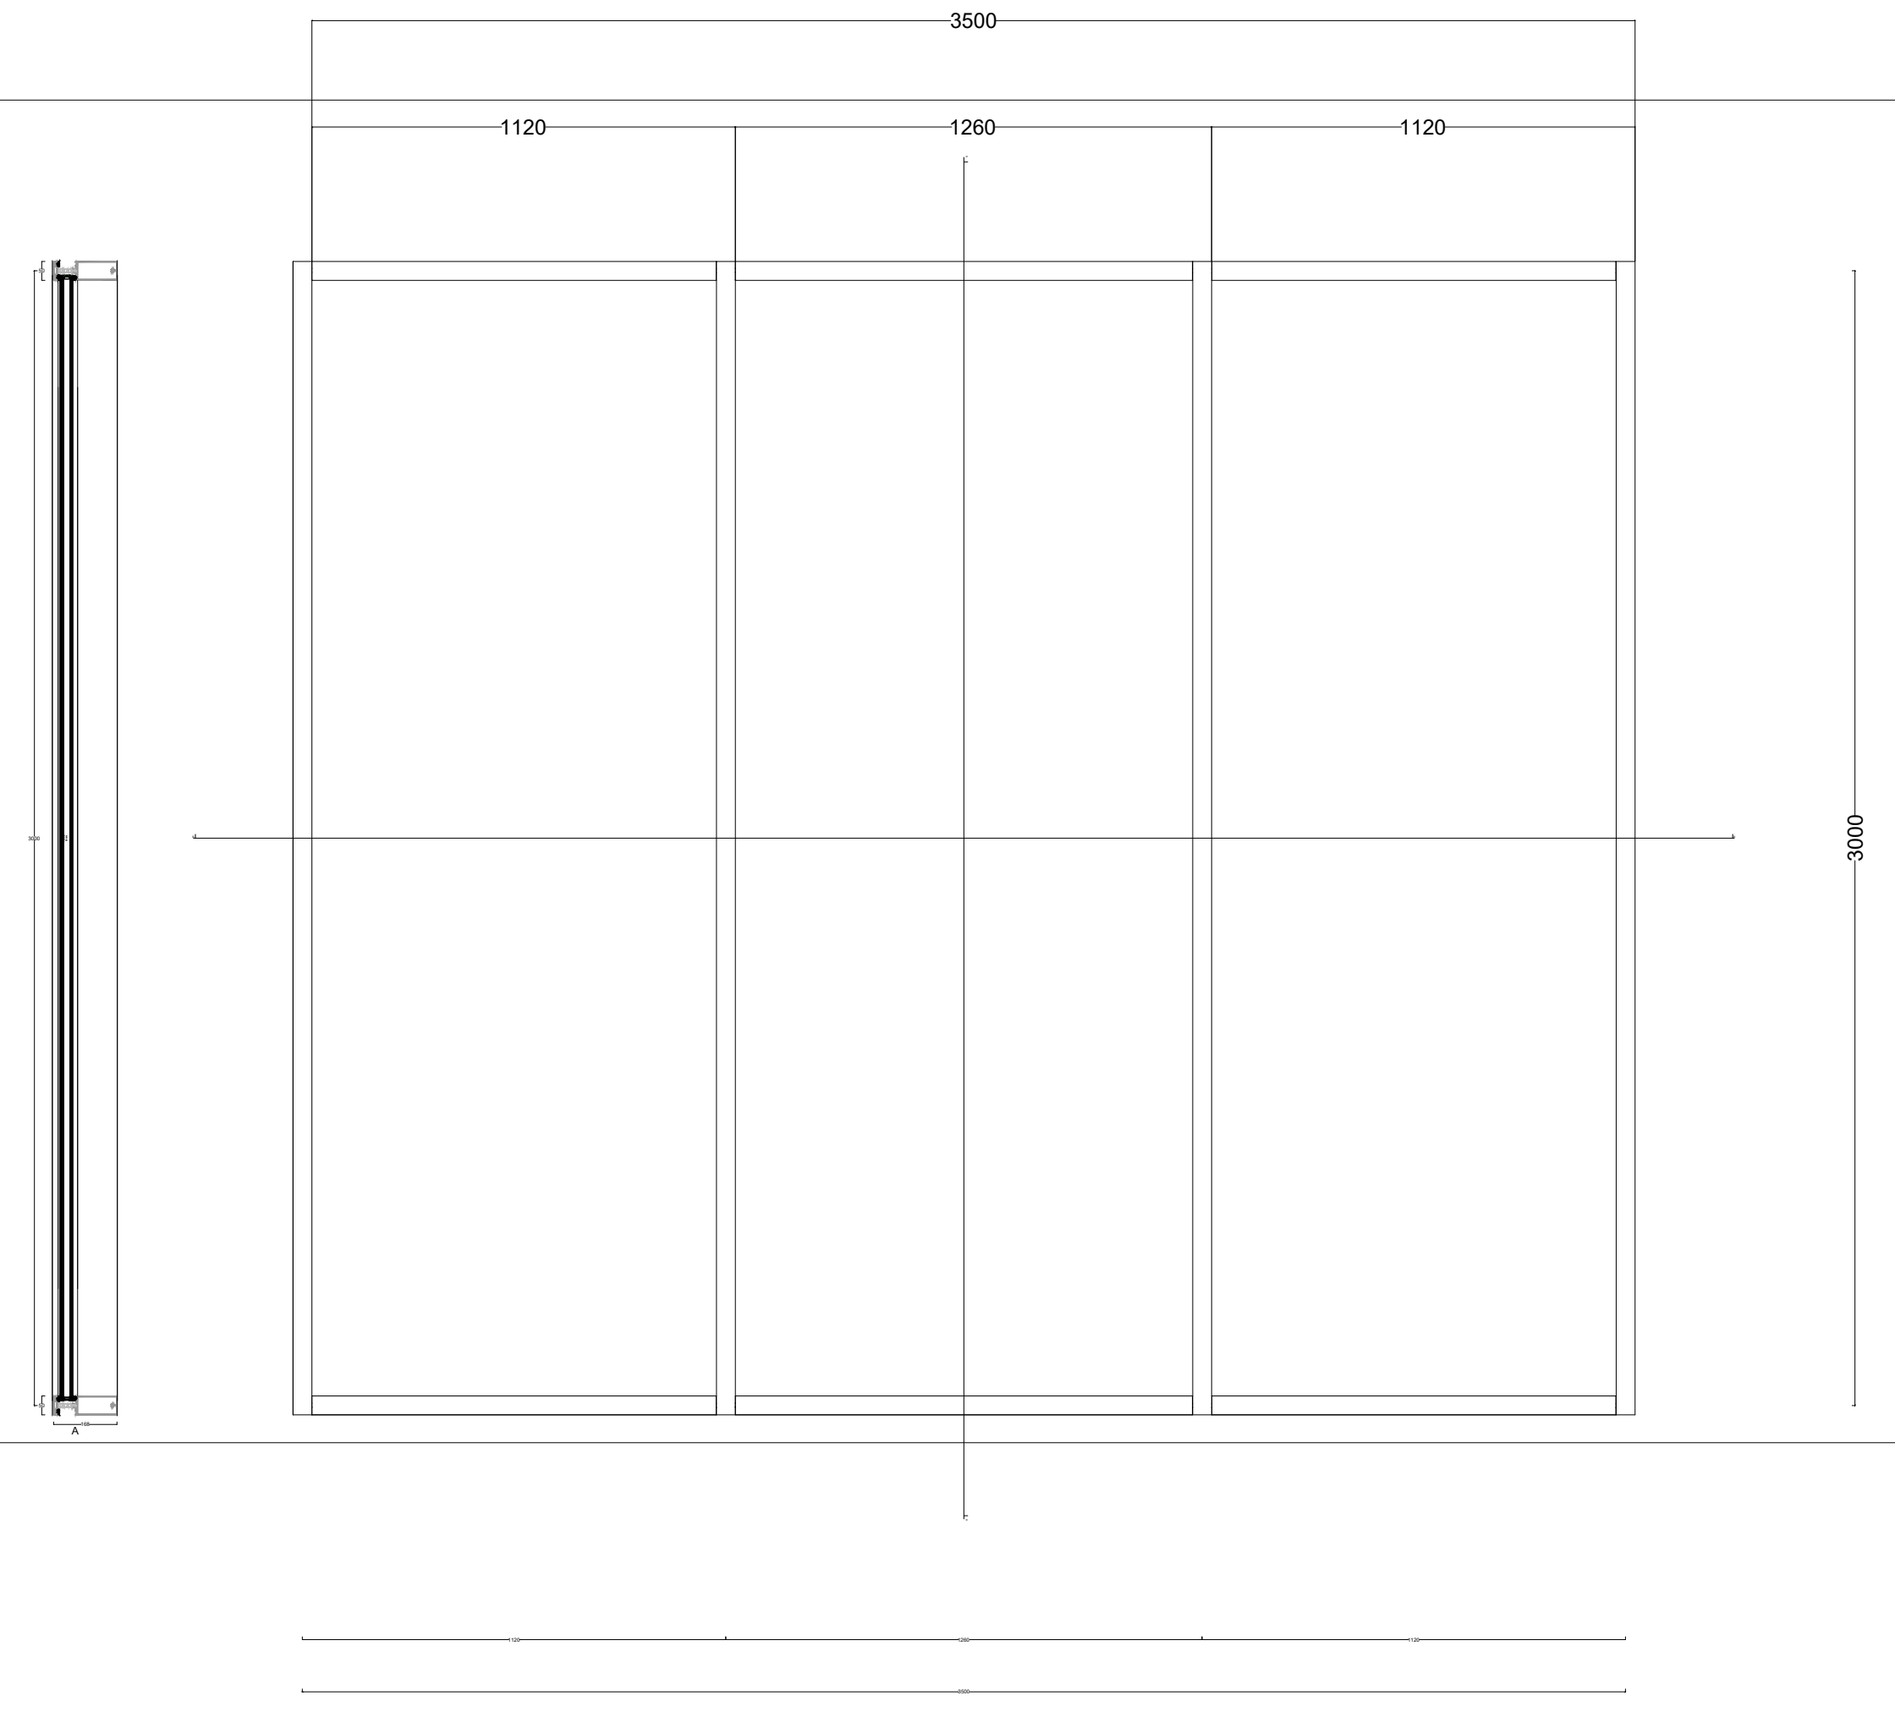

EW15

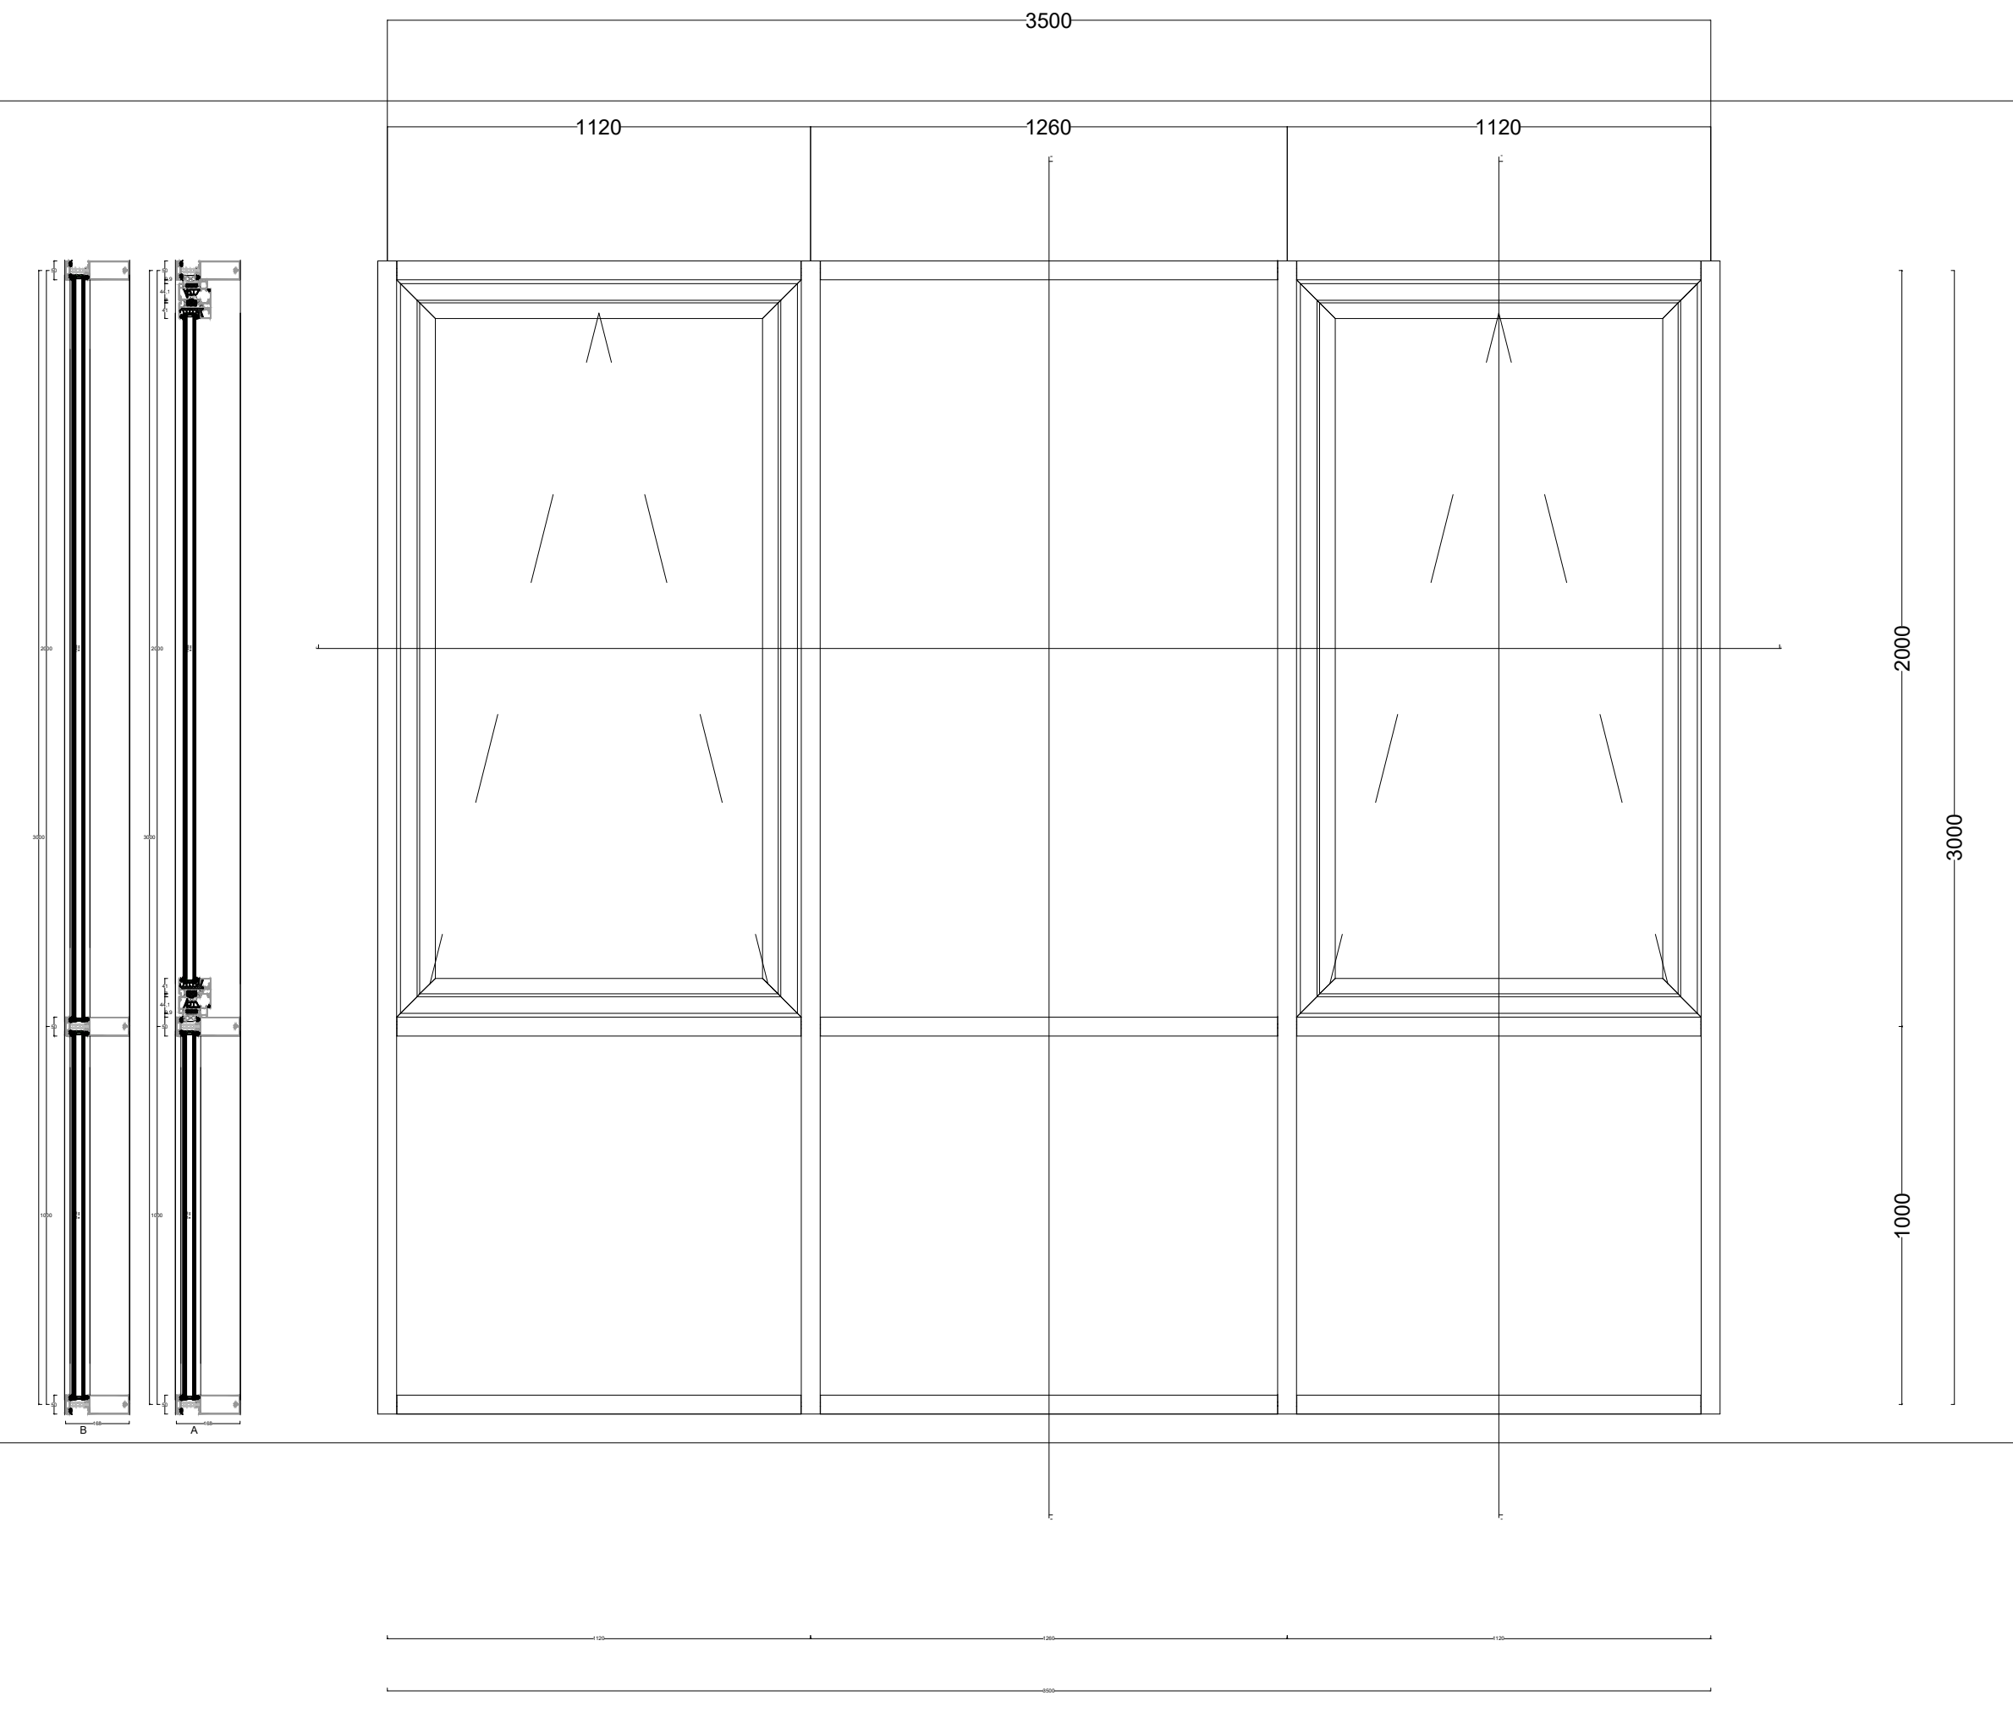

CUP F18H22000220005 - CIG 9210532374

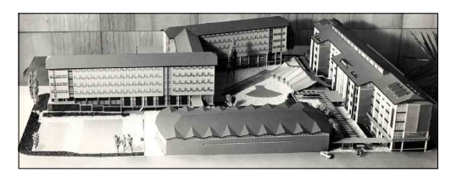

UNIVERSITA' DEGLI STUDI DI BERGAMO
EX CASERMA GUARDIA DI FINANZA

Progetto di investimento relativo all'intervento di ristrutturazione e rifunzionalizzazione del complesso immobiliare di Via dello Statuto, n. 21 - Bergamo - Corpo C) - "Residenze"

PROGETTO ESECUTIVO

COMMITTENZA
Università degli studi di Bergamo
Area Infrastrutture - Settore Infrastrutture
via Salvecchio 19, 24129 Bergamo

RESPONSABILE UNICO DEL PROCEDIMENTO
Ing. Marta Sabbatini

RTP DI PROGETTAZIONE

CAPOGRUPPO MANDATARIA

Studio Altieri S.p.A.
Coordinamento progettuale ed integrazioni specialistiche, progettazione edile-architettonica e coordinamento della sicurezza in fase di progettazione

Responsabile integrazione tra le prestazioni specialistiche & PM
Ing. Alessandro Artuso

Project Coordinator & CDE Manager (Giovane professionista)
Ing. Filippo Bee

Esperto in sistemi edilizi
Ing. Andrea Sbalchiero

BIM Manager
Geom. Marika Riccobene

Progettazione ambientale
Ing. Laura Dalla Valle

Progettazione architettonica
Arch. Andrea Chiarolini
Arch. Laura Von Dellemann

Coordinatore della Sicurezza in fase di Progettazione
Geom. Moreno Gazzetto

MANDANTI

ICONIA Ingegneria Civile S.r.l.

Progettazione strutturale
Ing. Romj Friso
Ing. Domenico D'Anza

Energo S.r.l.

Responsabile progettazione impianti meccanici, elettrici, idrico sanitari
Certificazione energetica
Professionista antincendio
Arch. Denis Zuin

Dott. Geol. Paolo Cornale Geologo

TITOLO DEL DOCUMENTO:
ARCHITETTURA
ABACO SERRAMENTI ESTERNI 1 DI 3

SCALA 1:20

CODICE:	C1088	E	AR	DET	00	030	R00
	Commessa	Fase	Disciplina	Set	Livello	Numero	Revisione

Revisione	Data	Motivo	Redatto	Controllato	Approvato
00	OTTOBRE 2026	EMISSIONE PE	L.V.D.	F.B.	A.A.