

MONTANTI TRAVERSI LATO NORD BASSO EMISSIVI

EW14

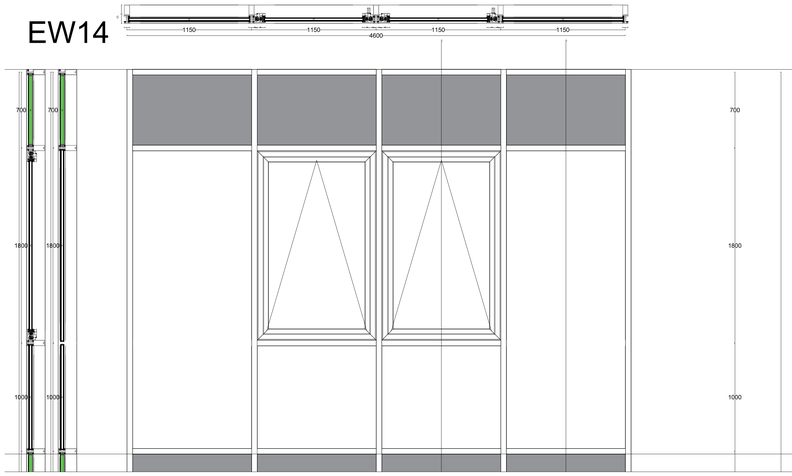


VETRATA LATO NORD L0
BASSO EMISSIVI

EW15

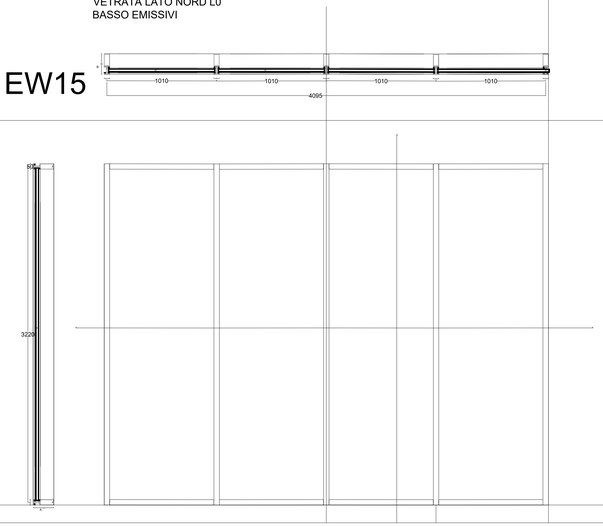

VETRATA SALA POLIVALENTE LATO NORD BASSO EMISSIVO
CON RULLO INTERNO OSCURANTE MOTORIZZATO

EW16

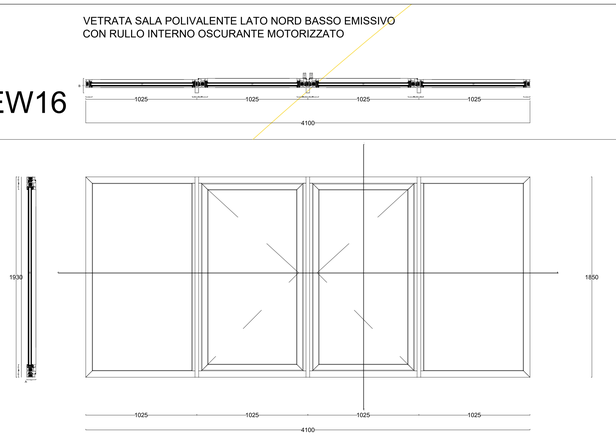


'17



EW18





EW19

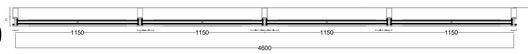



EW20




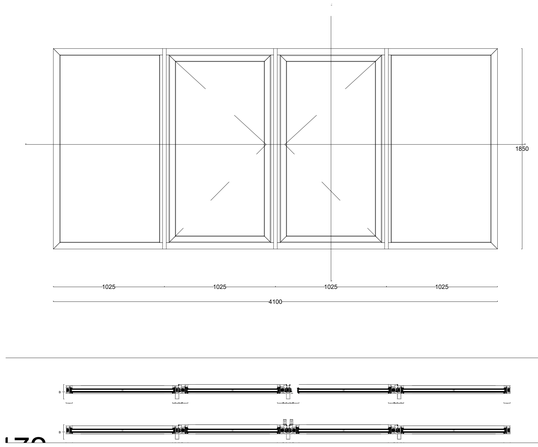

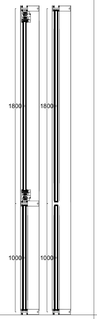

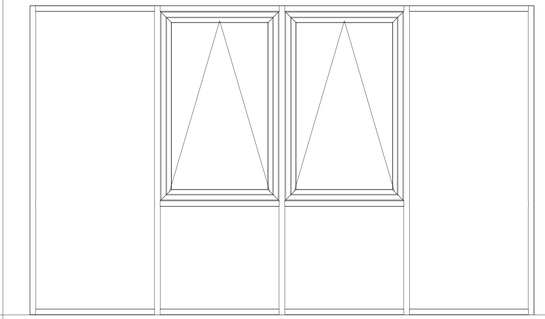


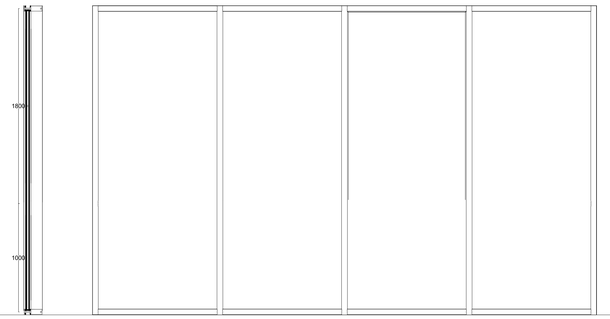


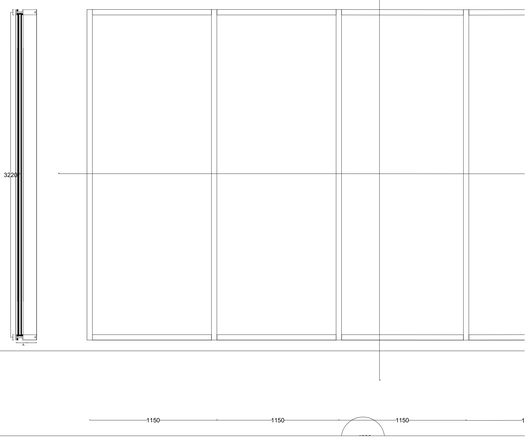


F21

VETRATA L0 CON SPORTO 1M
FATTORE SOLARE

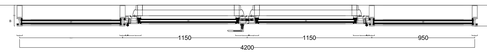


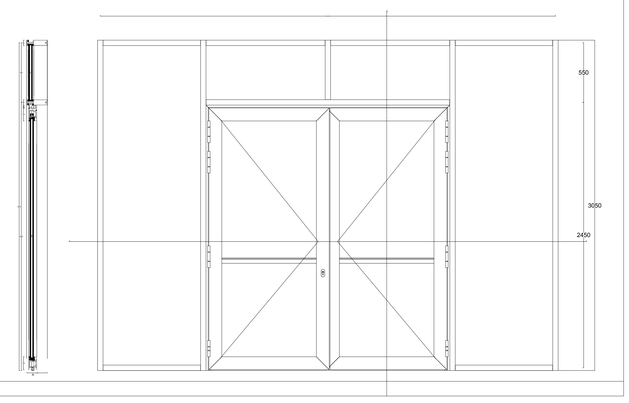

EW22

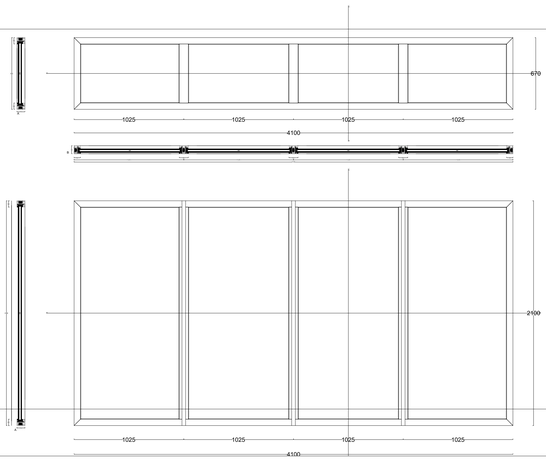

EW23

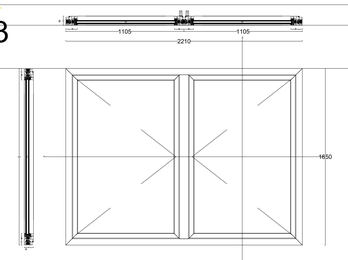

EW24

CUP F18H22000220005 - CIG 9210532374



UNIVERSITA' DEGLI STUDI DI BERGAMO

EX CASERMA GUARDIA DI FINANZA

Progetto di investimento relativo all'intervento di ristrutturazione e rifunzionalizzazione del complesso immobiliare di Via dello Statuto, n. 21 - Bergamo - Corpo C) - "Residenze"

PROGETTO ESECUTIVO

COMMITTENZA
Università degli studi di Bergamo
Area Infrastrutture - Settore Infrastrutture
via Salvecchio 19, 24129 Bergamo

RESPONSABILE UNICO DEL PROCEDIMENTO
Ing. Marta Sabbatini

RTP DI PROGETTAZIONE

CAPOGRUPPO MANDATARIA

Studio Albert S.p.A.
Coordinamento progettuale ed integrazioni specialistiche, progettazione edile-architettonica e strutturale, sicurezza in fase di progettazione

Responsabile integrazione tra le prestazioni specialistiche & PM
Ing. Alessandro Artuso

Project Coordinator & CDE Manager (Gli/ovane professionista)
Ing. Filippo Bee

BIM Manager
Geom. Marika Riccobene

Progettazione architettonica
Arch. Andrea Chiarolini
Arch. Laura Von Dellemann

Esperto in sistemi edilizi
Ing. Andrea Sbalchiero

Progettazione ambientale
Ing. Laura Dalla Valle

Coordinatore della Sicurezza in fase di Progettazione
Geom. Moreno Gazzetto

MANDANTI

ICONIA Ingegneria Civile S.r.l.

Progettazione strutturale
Ing. Romj Friso
Ing. Domenico D'Anza

Energo S.r.l.

Responsabile progettazione impianti meccanico, elettrici, idrico sanitari Certificazione energetica
Professionista antincendio
Arch. Denis Zuin

Dott. Geol. Paolo Cornale Geologo

TITOLO DEL DOCUMENTO:
ARCHITETTURA
ABACO SERRAMENTI ESTERNI 2 DI 3

SCALA 1:20

CODICE:

C1088	E	AR	DET	00	031	R00
Commessa	Fase	Disciplina	Set	Livello	Numero	Revisione

Revisione	Data	Motivo	Redatto	Controllato	Approvato
00	OTTOBRE 2020	EMISSIONE PE	L.V.D.	F.B.	A.A.