

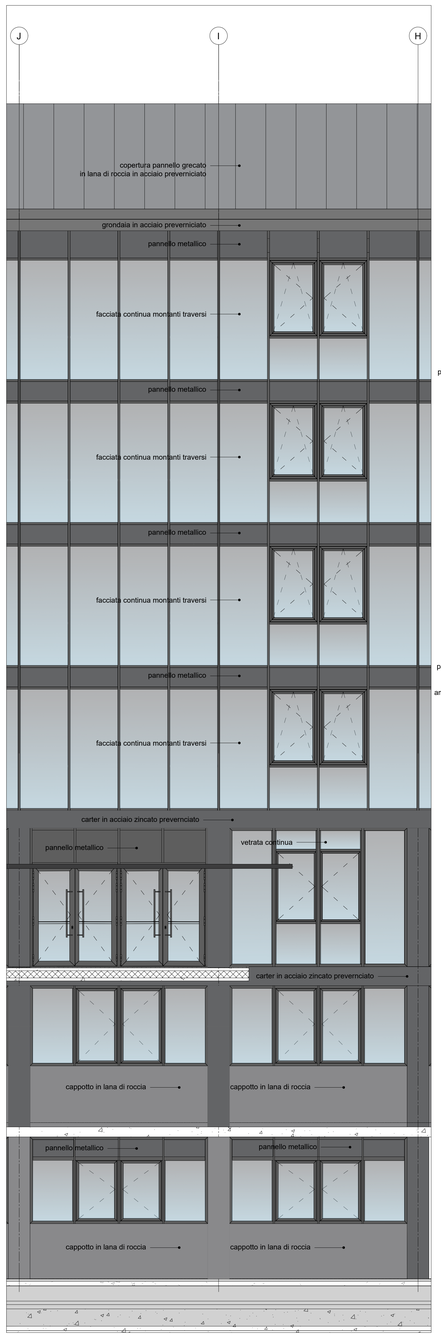



ALZATO NORD CORPO CENTRALE

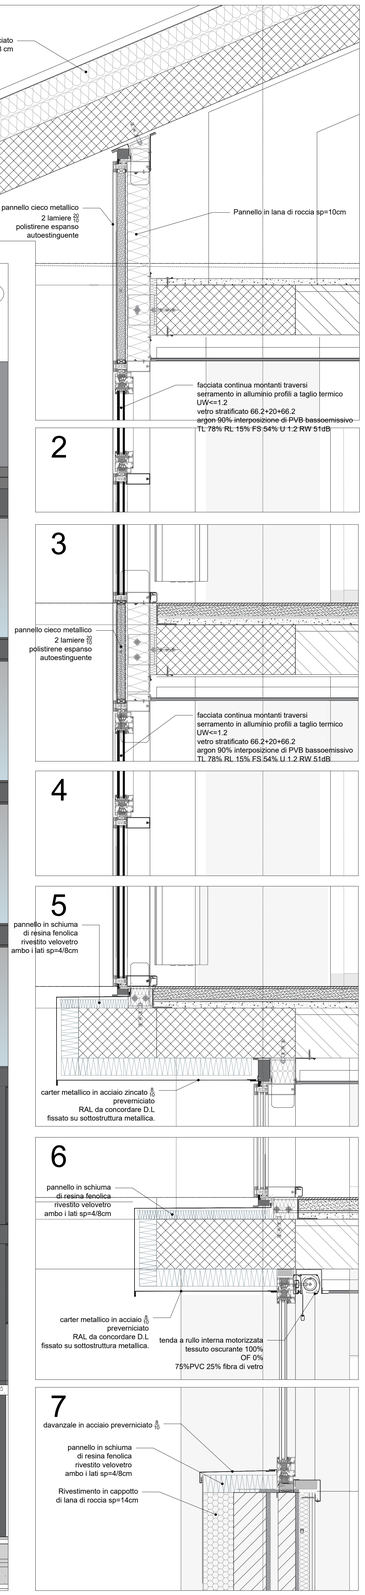


SEZIONI DI DETTAGLIO LATO NORD 1/20

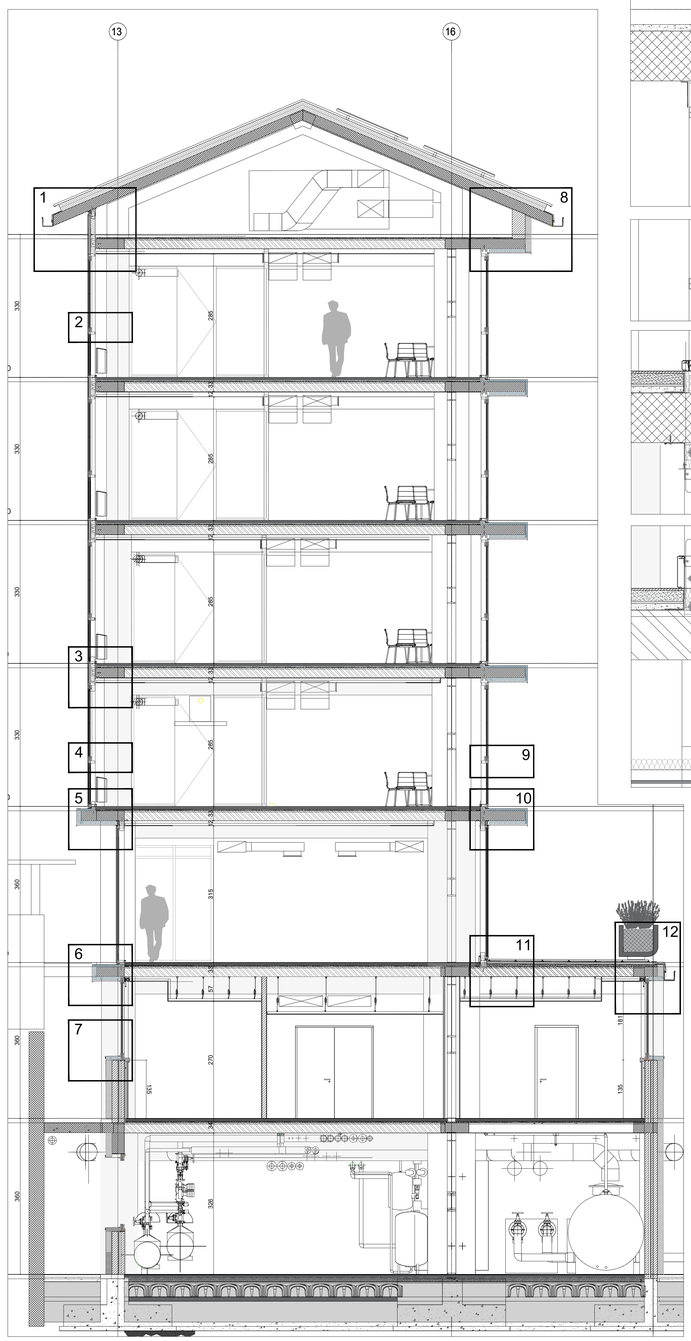


SEZIONE CORPO CENTRALE

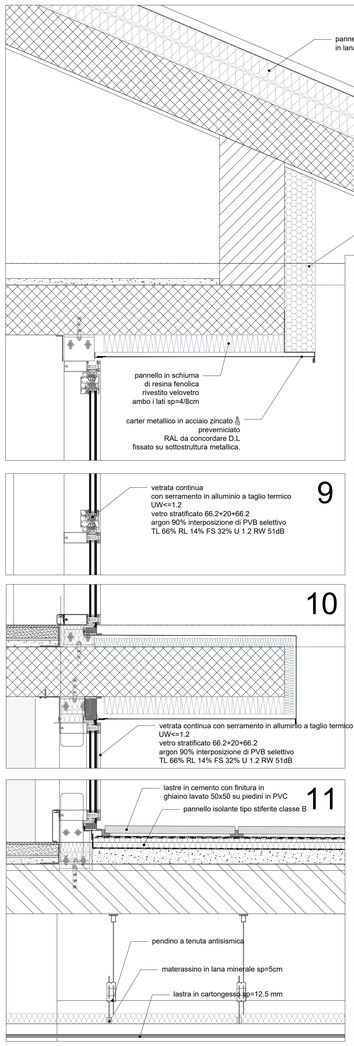

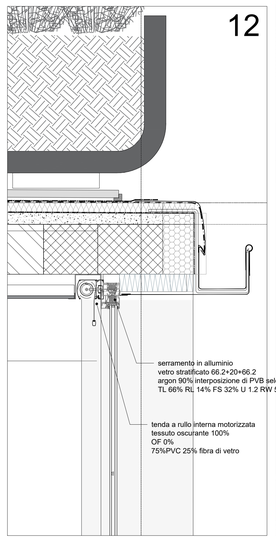

SEZIONI DI DETTAGLIO LATO SUD 1/20

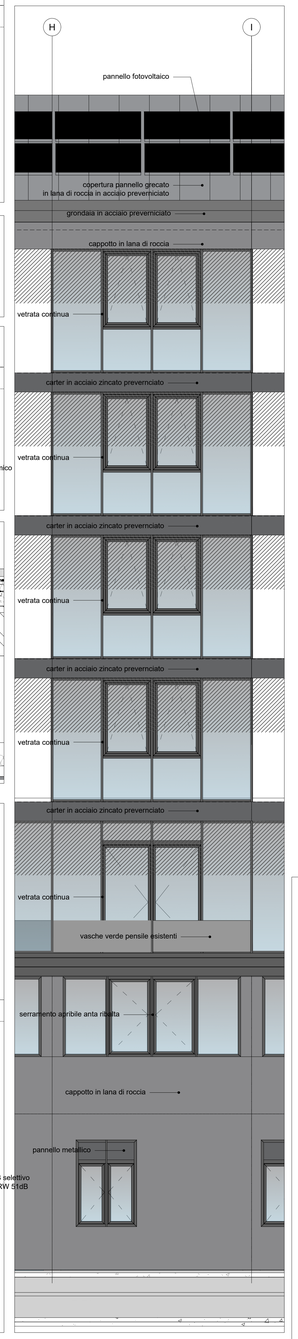

ALZATO SUD CENTRALE

CUP F18H22000220005 - CIG 9210532374



UNIVERSITA' DEGLI STUDI DI BERGAMO

EX CASERMA GUARDIA DI FINANZA

Progetto di investimento relativo all'intervento di ristrutturazione e rifunzionalizzazione del complesso immobiliare di Via dello Statuto, n. 21 - Bergamo - Corpo C) - "Residenze"

PROGETTO ESECUTIVO

COMMITTENZA
Università degli studi di Bergamo
Area Infrastrutture - Settore Infrastrutture
via Salvecchio 19, 24129 Bergamo

RESPONSABILE UNICO DEL PROCEDIMENTO
Ing. Marta Sabbatini

RTP DI PROGETTAZIONE

CAPOGRUPPO MANDATARIA

Studio Atlieri S.p.A.
Coordinamento progettuale ed integrazione prestazioni progettazione edile-architettonica e coordinamento della sicurezza in fase di progettazione

Responsabile integrazione tra le prestazioni specialistiche & PM
Ing. Alessandro Artuso

Project Coordinator & CDE Manager (Giovane professionista)
Ing. Filippo Bee

BIM Manager
Geom. Marika Riccobene

Progettazione architettonica
Arch. Andrea Chiarolini
Arch. Laura Von Dellemann

Esperto in sistemi edilizi
Ing. Andrea Sbalchiero

Progettazione ambientale
Ing. Laura Dalla Valle

Coordinatore della Sicurezza in fase di Progettazione
Geom. Moreno Gazzetto

MANDANTI

ICONIA Ingegneria Civile S.r.l.
Progettazione strutturale
Ing. Ronj Friso
Ing. Domenico D'Anza

Energo S.r.l.
Responsabile progettazione impianti meccanici, elettrici, idrico sanitari
Certificazione energetica
Professionista antincendio
Arch. Denis Zuin

Dott. Geol. Paolo Cornale Geologo

TITOLO DEL DOCUMENTO:
ARCHITETTURA
SEZIONI DI DETTAGLIO 2 DI 2

SCALA 1:50
1:20

CODICE: C1088 | E | AR | SAE | 00 | 016 | R00
Commessa | Fase | Disciplina | Set | Livello | Numero | Revisione

Revisione	Data	Motivo	Redatto	Controllato	Approvato
00	OTTOBRE 2026	EMISSIONE PE	L.V.D.	F.B.	A.A.