
PIANTA PIANO INTERRATO DI STATO DI PROGETTO_01

Scala 1 : 100

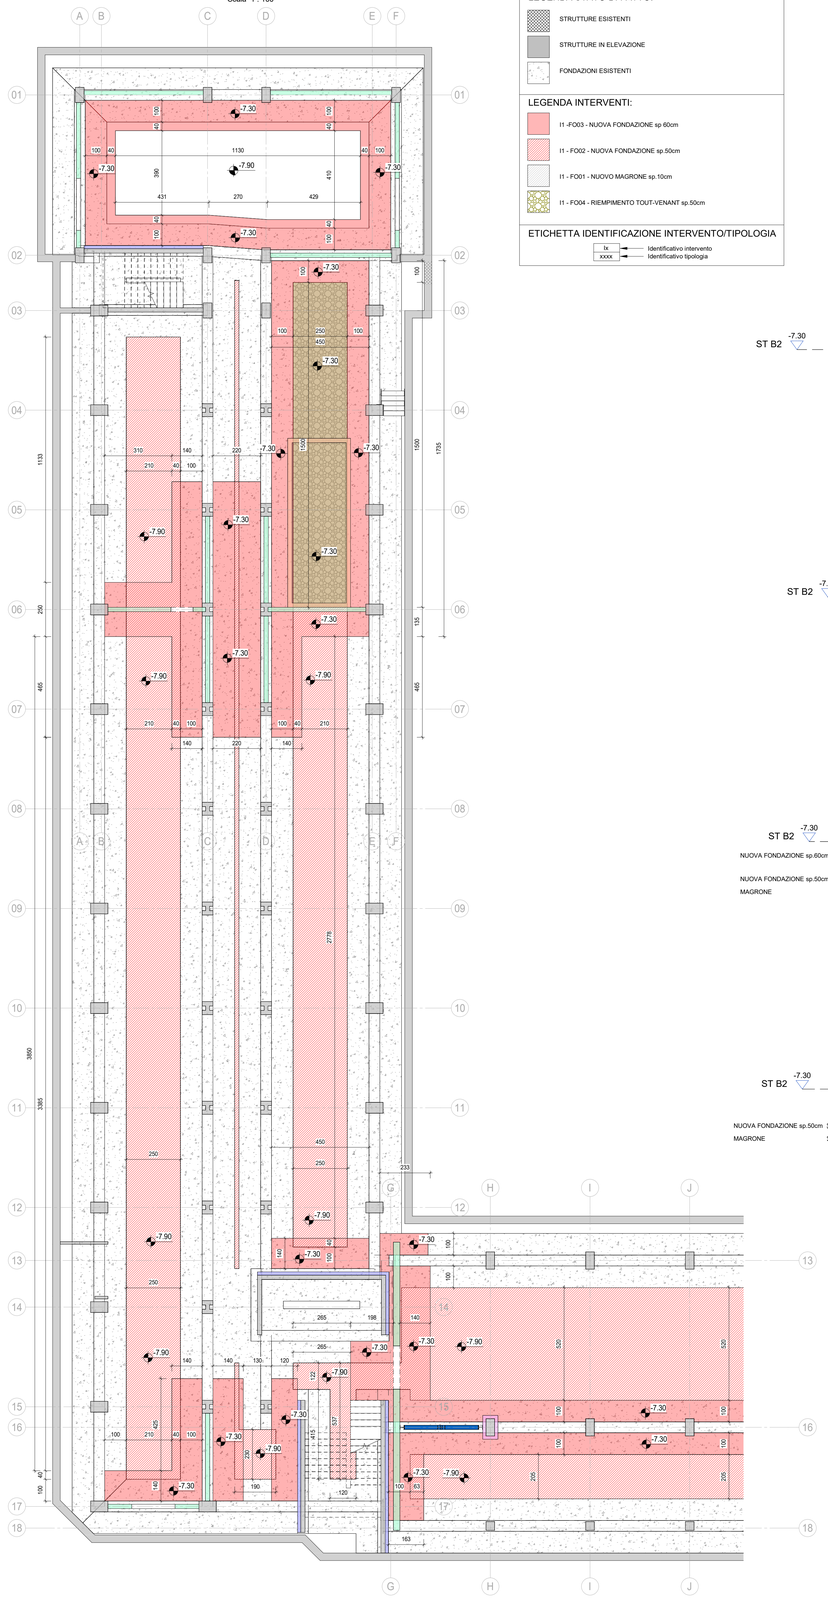

LEGENDA STATO DI FATTO:

- STRUTTURE ESISTENTI
- STRUTTURE IN ELEVAZIONE
- FONDAZIONI ESISTENTI

LEGENDA INTERVENTI:


- I1 -FO03 - NUOVA FONDAZIONE sp 60cm
- I1 - FO02 - NUOVA FONDAZIONE sp.50cm
- I1 - FO01 - NUOVO MAGRONE sp.10cm
- I1 - FO04 - RIEMPIMENTO TOUT-VENANT sp.50cm

ETICHETTA IDENTIFICAZIONE INTERVENTO/TIPOLOGIA

Ix — Identificativo intervento
XXXX — Identificativo tipologia


TIPO 1

Scala 1 : 50

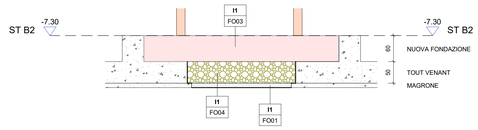


TIPO 2

Scala 1 : 50

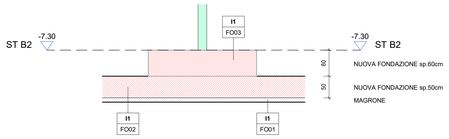


TIPO 3

Scala 1 : 50

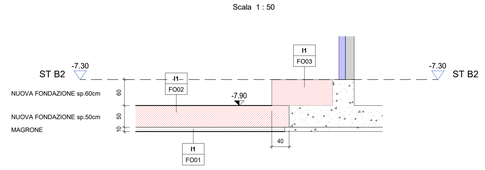


TIPO 4

Scala 1 : 50

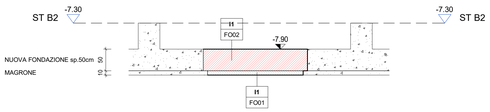


SEZIONE ARMATURA PLATEA TIPO 1

scala 1:20

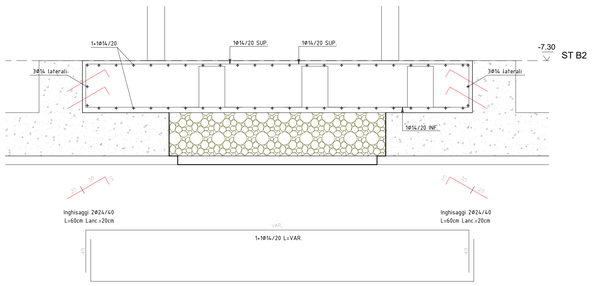


SEZIONE ARMATURA PLATEA TIPO 2

scala 1:20

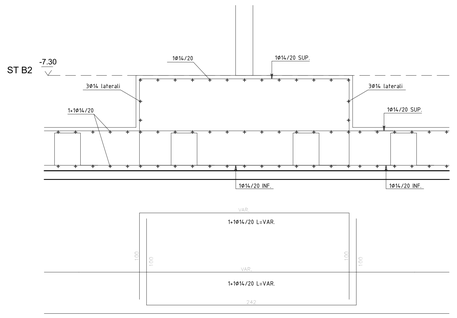


SEZIONE ARMATURA PLATEA TIPO 3

scala 1:20

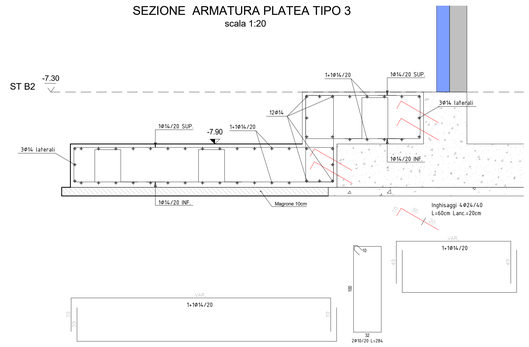


SEZIONE ARMATURA PLATEA TIPO 4

scala 1:20

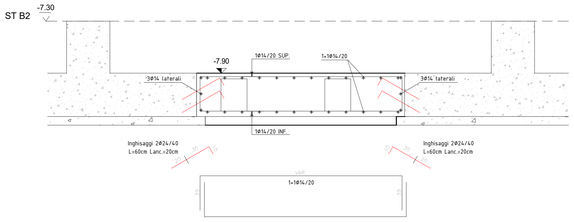


SEZIONE CENTRALE TIPOLOGICA PLATEA sp.50cm

scala 1:20

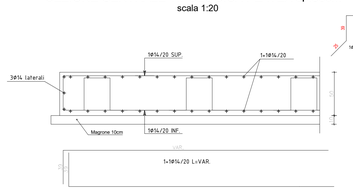


SEZIONE CENTRALE TIPOLOGICA PLATEA sp.60cm

scala 1:20

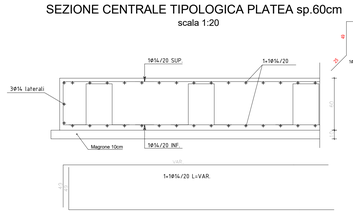

NODI BULLONATI

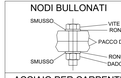

ACCIAIO PER CARPENTERIA METALLICA

- Carpenteria metallica: S275JR zincato
- Zincatura a caldo
- Zincatura a freddo nelle zone di saldatura in opera
- Inghisaggi chimici:
  Connessioni certificate C2 con resina TIPO HILTI HIT RE500 V4 e barre filettate classe 8.8

CLASSE DI ESECUZIONE SECONDO UNIEN1090

Classe di conseguenza	CC3
Categoria di servizio	SC1
Categoria di produzione	PC2
Classe di esecuzione	EXC3

INGHISAGGI CHIMICI




BULLONI

classe 8.8

Ø BULL	12	14	16	20	24
Ø FORO	13.0	15.0	17.0	21.0	25.5
COPPIE SERR.to	conforme vigente normativa				
SIMBOLO	◆	□	➔	✣	✣

SALDATURA A CORDONE D'ANGOLO

(OVE NON ALTRIMENTI INDICATO)

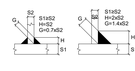

SALDATURA DI PRIMA CLASSE PER GIUNTO a "T" A COMPLETA PENETRAZIONE

(PER TUTTE LE FLANGE OVE NON ALTRIMENTI INDICATO)



PARTICOLARE GANCI



PARTICOLARE RIPRESA DI GETTO VERTICALE



PARTICOLARE SOVRAPPOSIZIONI



PARTICOLARE CHIUSURA DELLE GABBIE




SPECIFICA COPRIFERRO/QUOTATURA



CALCESTRUZZO

Calcestruzzo per	Magrone	Fondazione	Orizzontale	Strutture in elevazione
Classe di resistenza (Fck/Rck)	C12/15	C28/35	C35/45	C35/45
Classe esposizione ambientale	-	XC2	XC2	XC2
Cemento tipo	42.5N	42.5N	42.5N	42.5N
Rapporto max acqua/cemento	CONFORME ALLA NORMATIVA VIGENTE			
Contenuto min. cemento (kg/m³)				
Ø max inerti (mm)	-	16	16	16
Classe di consistenza	-	S4	S5	SCC
Copriferro netto (mm)	-	40	30	30
Copriferro netto controterra	≥ 40 mm			
Profondità permeazione acqua secondo ISO7031	< 20 mm			

SCHEMA PIEGATURE

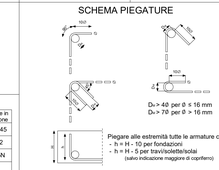

D_m > 40 per Ø ≤ 16 mm
D_m > 70 per Ø > 16 mm

ACCIAIO PER CEMENTO ARMATO

ACCIAIO TIPO B450C controllato in stabilimento e saldabile

PRESCRIZIONI NOTE GENERALI

- VERIFICARE TUTTE LE MISURE IN CANTIERE PRIMA DI EFFETTUARE L'ORDINATIVO DEI MATERIALI
- VERIFICARE TUTTE LE MISURE E I FORI CON IL PROGETTO ARCHITETTONICO E IMPIANTISTICO
- OVE PREVISTI FIORETTI INGHISATI CON RESINA E TASSELLI CHIMICI DOVRANNO ESSERE POSTI IN OPERA SECONDO LE PRESCRIZIONI DEL PRODUTTORE DELLE RESINE NELLE CONDIZIONI AMBIENTALI IDONEE E PREVIA PERFETTA PULIZIA DEL FORO
-IN SEGUITO ALLO STRIP-OUT VERIFICARE GEOMETRIA E DIMENSIONI DELLE STRUTTURE INTERESSATE DAGLI INTERVENTI IN CANTIERE
-VERIFICA PREVENTIVAMENTE LA STABILITA' DELLE STRUTTURE ESISTENTI E LE FASI OPERATIVE PRIMA DI DEMOLIRE
-PER LE DEMOLIZIONI DEI SOLAI PROCEDERE PER AREE LIMITATE VERIFICANDONE LA STABILITA' PRIMA DI PROCEDERE IN ALTRE ZONE
-PER LE DEMOLIZIONI PREVEDERE OPPORTUNE OPERE PROVVISIONALI E PUNTELLAZIONE

CUP F18H22000220005 - CIG 9210532374



UNIVERSITA' DEGLI STUDI DI BERGAMO

EX CASERMA GUARDIA DI FINANZA

Progetto di investimento relativo all'intervento di ristrutturazione e rifunzionalizzazione del complesso immobiliare di Via dello Statuto, n. 21 - Bergamo - Corpo C) - "Residenze"

PROGETTO ESECUTIVO

COMMITTENZA
Università degli studi di Bergamo
Area Infrastrutture - Settore Infrastrutture
via Salvecchio 19, 24129 Bergamo

RESPONSABILE UNICO DEL PROCEDIMENTO
Ing. Marta Sabbatini

RTP DI PROGETTAZIONE

CAPOGRUPPO MANDATARIA

Studio Alberi S.p.A.
Coordinamento progettuale ed integrazioni specialistiche, progettazione edile-architettonica e direzione lavori strutturale in fase di progettazione

Responsabile integrazione tra le prestazioni specialistiche & PM
Ing. Alessandro Arluso

Project Coordinator & CDE Manager (Gioviane professionista)
Ing. Filippo Bes

BIM Manager
Geom. Marika Riccobene

Progettazione architettonica
Arch. Andrea Chiarelini
Arch. Laura Von Dellemann

Esperto in sistemi edili
Ing. Andrea Sbalchiero

Progettazione ambientale
Ing. Laura Dalla Valle

Coordinatore della Sicurezza in fase di Progettazione
Geom. Moreno Gazzetto

MANDANTI

ICONIA Ingegneria Civile S.r.l.
Progettazione strutturale
Ing. Ronj Frisa
Ing. Domenico D'Anza

Energo S.r.l.
Responsabile progettazione impianti meccanico, elettrici, idrico sanitari
Certificazione energetica
Professionista antincendio
Arch. Denis Zuin

Dott. Geol. Paolo Corrado Geologo

TITOLO DEL DOCUMENTO: STRUTTURE

SCALA: VAR

FONDAZIONI-DETTAGLI CARPENTERIA ARMATURA 1 DI 2

CODICE: C1088 (Commessa) E (Fase) ST (Disciplina) DET (Sett.) 00 (Livello) 010 (Numero) r00 (Revisione)

Revisione	Data	Motivo	Redatto	Controllato	Approvato
00	19/10/2026	Prima emissione	RM	MG	DD