

PROSPETTO SETTO SE.20 ARMATURA AGGIUNTIVA
scala 1:100

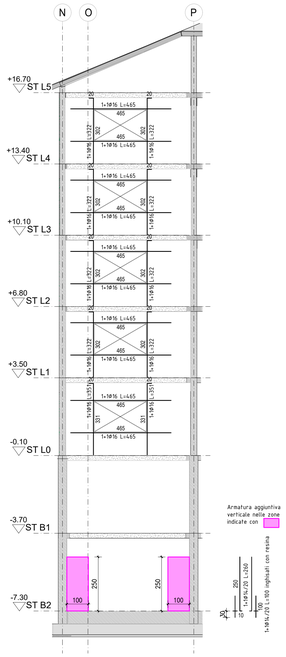


SEZIONE SETTO SE.20
scala 1:50

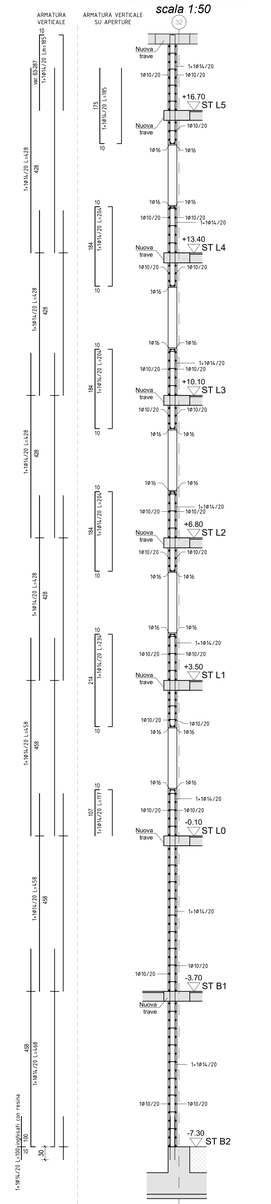

PROSPETTO SETTO SE.21 ARMATURA AGGIUNTIVA
scala 1:100


SEZIONE SETTO SE.21
scala 1:50

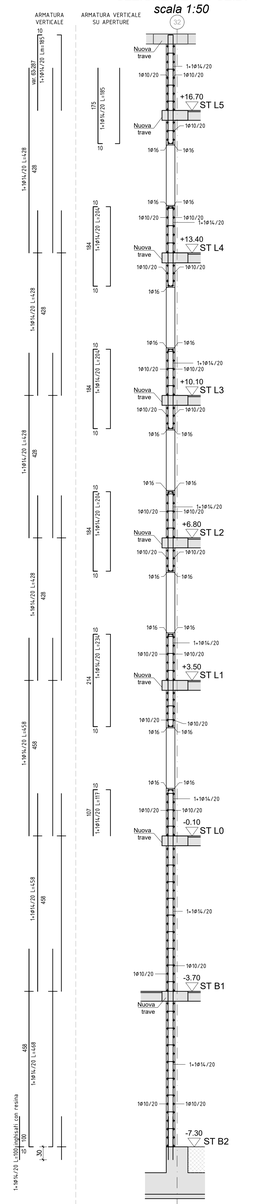


N.B. Per posizione e dimensioni delle nuove travi vedere le piante di progetto

N.B. Per posizione e dimensioni delle nuove travi vedere le piante di progetto

PROSPETTO SETTO SE.22 ARMATURA AGGIUNTIVA
scala 1:100

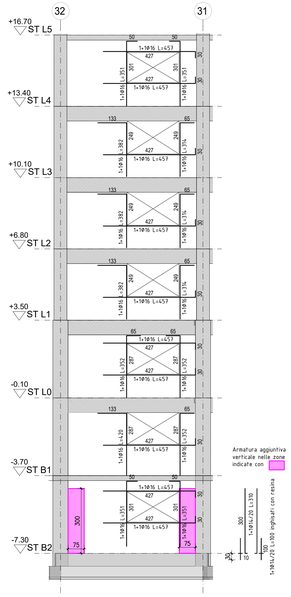


SEZIONE SETTO SE.22
scala 1:50

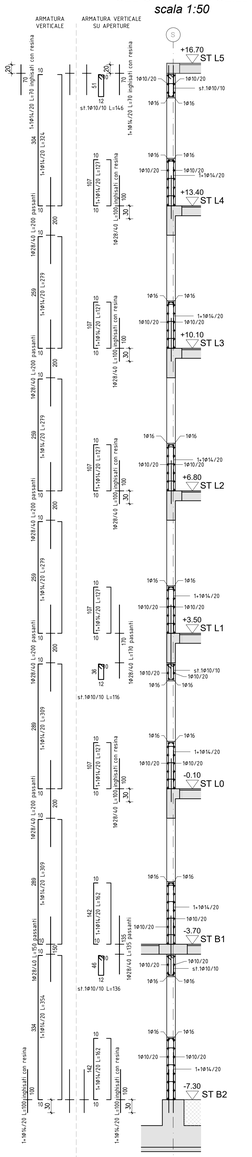


PROSPETTO SETTO SE.23 ARMATURA AGGIUNTIVA
scala 1:100


SEZIONE SETTO SE.23
scala 1:50

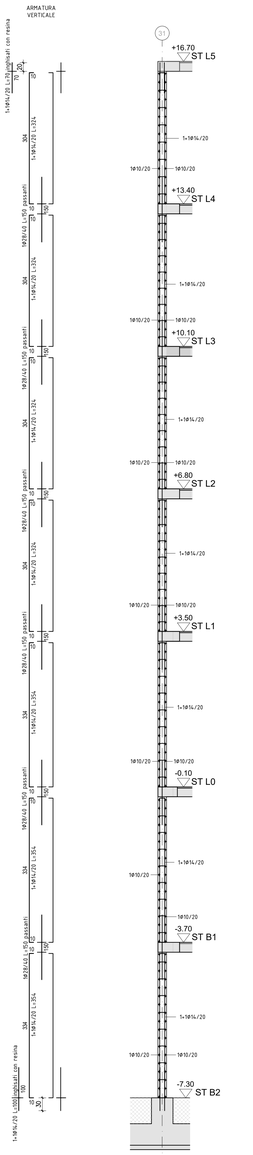


DETTAGLIO COLLEGAMENTO NUOVI SETTI-SOLAIO ESISTENTE
SEZIONE
SCALA 1:25

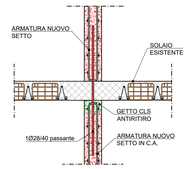


DETTAGLIO COLLEGAMENTO NUOVI SETTI-PILASTRI
PIANTA
SCALA 1:25

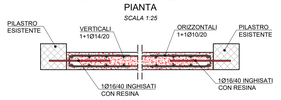

KEY PLAN
scala 1:600

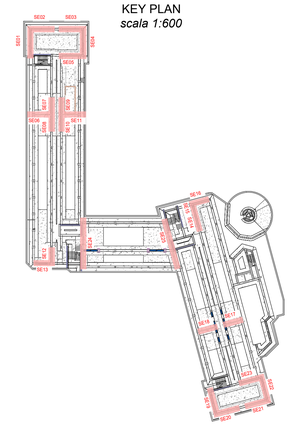

NODI BULLONATI

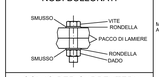

ACCIAIO PER CARPENTERIA METALLICA
- *Carpenteria metallica: S275JR zincato*
- *Zincatura a caldo*
- *Zincatura a freddo nelle zone di saldatura in opera*
- *Inghisaggi chimici:*
  Connessioni certificate C2 con resina TIPO HILTI HIT RE500 V4 e barre filettate classe 8.8


CLASSE DI ESECUZIONE SECONDO UNIEN1090

Classe di conseguenza	*CC3*
Categoria di servizio	*SC1*
Categoria di produzione	*PC2*
Classe di esecuzione	*EXC3*

INGHISAGGI CHIMICI



SALDATURA A CORDONE D'ANGOLO
(OVE NON ALTRIMENTI INDICATO)

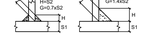

BULLONI *classe 8.8*


Ø BULL	*12*	*14*	*16*	*20*	*24*
Ø FORO	*13.0*	*15.0*	*17.0*	*21.0*	*25.5*
COPRI SERR.(mm)	*conforme vigente normativa*				
SIMBOLO	◆	■	●	▲	▼

SALDATURA DI PRIMA CLASSE PER GIUNTO A "T" A COMPLETA PENETRAZIONE
(PER TUTTE LE FLANGE OVE NON ALTRIMENTI INDICATO)



- *LE STRUTTURE METALLICHE DOVRANNO AVERE LE CONTROFRECCE DI MONTAGGIO OVE PREVISTO*

PARTICOLARE GANCI

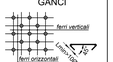


min 90ds/mq su tutti i muri

PARTICOLARE RIPRESA DI GETTO VERTICALE




Interruzione di getto

PARTICOLARE SOVRAPPOSIZIONI

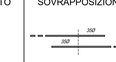

Sovrapposizione di reti elettrosaldate minimo due maglie

PARTICOLARE CHIUSURA DELLE GABBIE

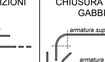


SPECIFICA COPRIFERRO/QUOTATURA



Le cuote sono riferite al filo esterno

SCHEMA PIEGATURE

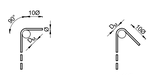

D≥ 40 per ø ≤ 16 mm
D≥ 70 per ø > 16 mm

Piegare alle estremità tutte le armature correnti:
- h = H - 10 per fondazioni
- h = H - 5 per travi/solette/solai
(salvo indicazione maggiore di copriferro)

CALCESTRUZZO

Calcestruzzo per	*Magrone*	*Fondazione*	*Orizzontale*	*Strutture in elevazione*
Classe di resistenza (Rck/Rck)	*C12/15*	*C28/35*	*C35/45*	*C35/45*
Classe esposizione ambientale		*XC3*	*XC2*	*XC2*
Cemento tipo	*42.5N*	*42.5N*	*42.5N*	*42.5N*
Rapporto max acqua/cemento	*CONFORME ALLA NORMATIVA VIGENTE*			
Contenuto min. cemento (kg/m³)				
Ø max inerti (mm)	-	*16*	*16*	*16*
Classe di consistenza	-	*S4*	*S5*	*SCC*
Copriferro netto (mm)	-	*40*	*30*	*30*
Copriferro netto controterra	*≥ 40 mm*			
Profondità permeazione acqua secondo ISO7031	*< 20 mm*			

ACCIAIO PER CEMENTO ARMATO

ACCIAIO TIPO B450C controllato in stabilimento e saldabile

PRESCRIZIONI NOTE GENERALI
- *VERIFICARE TUTTE LE MISURE IN CANTIERE PRIMA DI EFFETTUARE L'ORDINATIVO DEI MATERIALI*
- *VERIFICARE TUTTE LE MISURE E I FORI CON IL PROGETTO ARCHITETTONICO E IMPIANTISTICO*
- *OVE PREVISTI FIORETTI INGHISATI CON RESINA E TASSELLI CHIMICI DOVRANNO ESSERE POSTI IN OPERA SECONDO LE PRESCRIZIONI DEL PRODUTTORE DELLE RESINE NELLE CONDIZIONI AMBIENTALI IDONEE E PREVIA PERFETTA PULIZIA DEL FORO*
- *IN SEGUITO ALLO STRIP-OUT VERIFICARE GEOMETRIA E DIMENSIONI DELLE STRUTTURE INTERESSATE DAGLI INTERVENTI IN CANTIERE*
- *VERIFICARE PREVENTIVAMENTE LA STABILITÀ DELLE STRUTTURE ESISTENTI E LE FASI OPERATIVE PRIMA DI DEMOLIRE*
- *PER LE DEMOLIZIONI DEI SOLAI PROCEDERE PER AREE LIMITATE VERIFICANDONE LA STABILITA' PRIMA DI PROCEDERE IN ALTRE ZONE*
- *PER LE DEMOLIZIONI PREVEDERE OPPORTUNE OPERE PROVVISIONALI E PUNTELLAZIONE*

PIANTA SETTO SE.20
scala 1:50

PIANTA SETTO SE.21
scala 1:50

PIANTA SETTO SE.22
scala 1:50

PIANTA SETTO SE.23
scala 1:50

CUP F18H22000220005 - CIG 9210532374



UNIVERSITA' DEGLI STUDI DI BERGAMO

EX CASERMA GUARDIA DI FINANZA

Progetto di investimento relativo all'intervento di ristrutturazione e rifunzionalizzazione del complesso immobiliare di Via dello Statuto, n. 21 - Bergamo - Corpo C) - "Residenze"

PROGETTO ESECUTIVO

COMMITTENZA
Università degli studi di Bergamo
Area Infrastrutture - Settore Infrastrutture
via Salvecchio 19, 24129 Bergamo

RESPONSABILE UNICO DEL PROCEDIMENTO
Ing. Marta Sabbatini

RTP DI PROGETTAZIONE

CAPOGRUPPO MANDATARIA

Studio Attieri S.p.A.
Coordinamento progettuale ed integrazioni specialistiche, progettazione architettonica e coordinamento della sicurezza in fase di progettazione

Responsabile integrazione tra le prestazioni specialistiche & PM:
Ing. Alessandro Artuso

Project Coordinator & CDE Manager (Giovane professionista):
Ing. Filippo Bee

BIM Manager
Geom. Marika Riccobene

Progettazione architettonica
Arch. Andrea Chiarolini
Arch. Laura Von Dellemann

Esperto in sistemi edilizi
Ing. Andrea Sbalchiero

Progettazione ambientale
Ing. Laura Dalla Valle

Coordinatore della Sicurezza in fase di Progettazione
Geom. Moreno Gazzetto

MANDANTI

ICONIA Ingegneria Civile S.r.l.
Progettazione strutturale
Ing. Ronj Frino
Ing. Domenico D'Anza

Energo S.r.l.
Responsabile progettazione impianti meccanici, elettrici, idrico sanitari
Certificazione energetica
Professionista antincendio
Arch. Denis Zuin

Dott. Geol. Paolo Cornale Geologo

TITOLO DEL DOCUMENTO: STRUTTURE
NUOVI SETTI-DETTAGLI ARMATURA 5 DI 6

SCALA 1:50

CODICE: C1088 | E | ST | DET | 00 | 110 | r00
Commessa | Fase | Disciplina | Set | Livello | Numero | Revisione

Revisione	Data	Motivo	Redatto	Controllato	Approvato
00	10/10/2026	Prima emissione	D.B.	DB	MG