


CP07-1
Scala 1 : 50

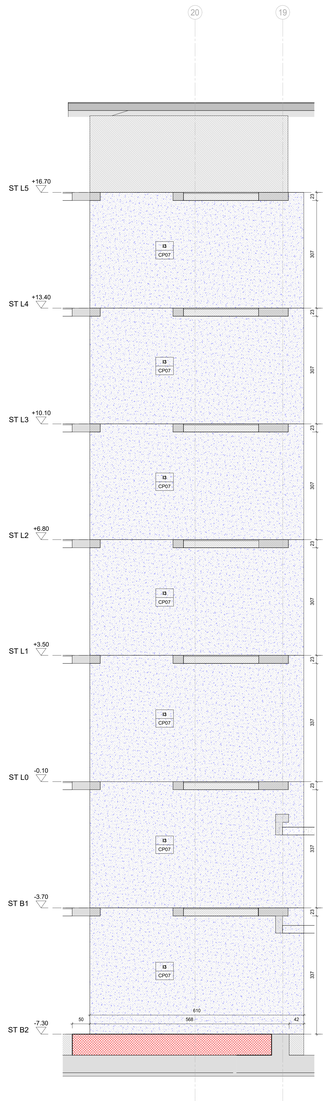

CP07-2
Scala 1 : 50

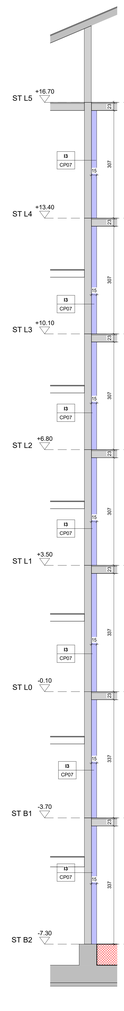


CP08-1
Scala 1 : 50

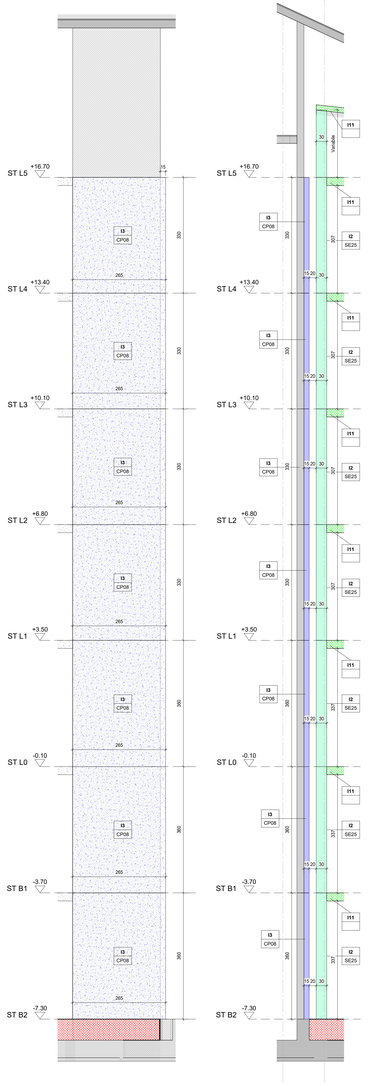


CP08-2
Scala 1 : 50


CP09-1
Scala 1 : 50

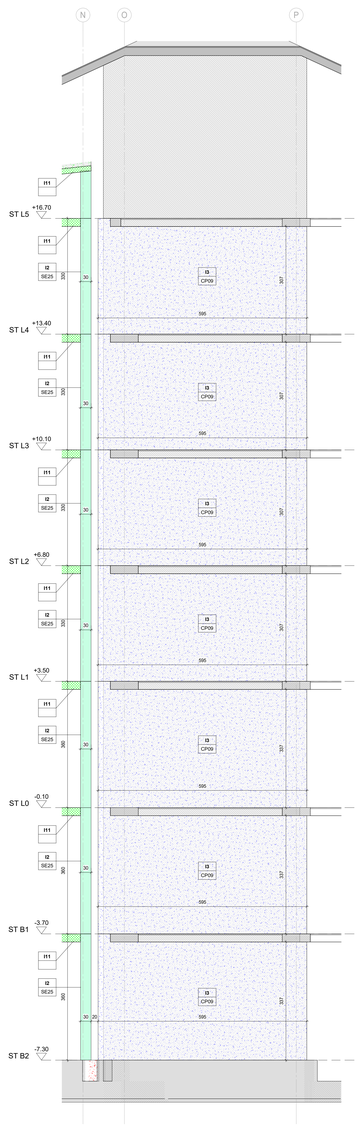

CP09-2
Scala 1 : 50

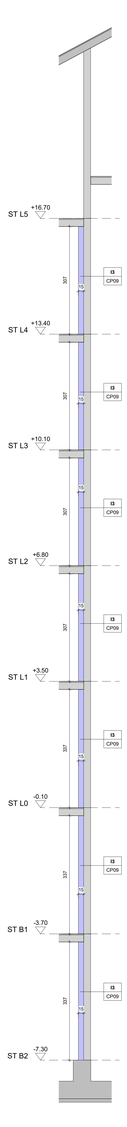


CP10-1
Scala 1 : 50

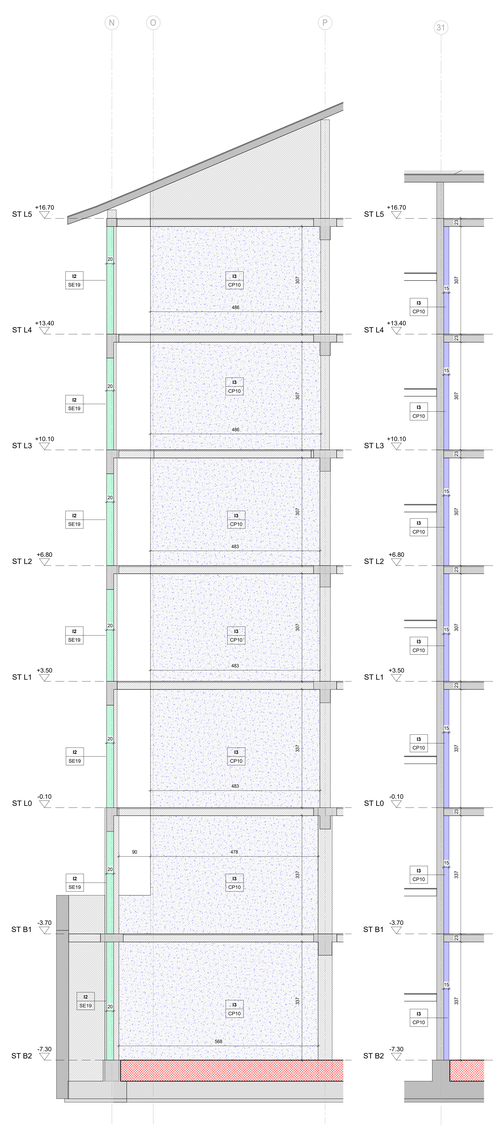

CP10-2
Scala 1 : 50

Key-Plan Contropareti

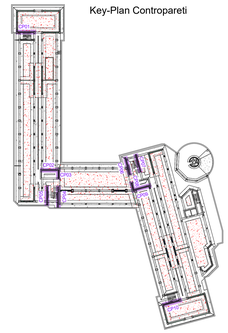

NODI BULLONATI



ACCIAIO PER CARPENTERIA METALLICA

- Carpenteria metallica: S275JR zincato
- Bullonatura 8.8
- Zincatura a freddo nelle zone di saldatura in opera
- Inghisaggi chimici
- Connessioni certificate C2 con resina TIPO HILTI HIT RE500 V4 e barre filettate classe 8.8

CLASSE DI ESECUZIONE SECONDO UNIEN1090


Classe di conseguenza	CC3
Categoria di servizio	SC1
Categoria di produzione	PC2
Classe di esecuzione	EXC3

INGHISAGGI CHIMICI



SALDATURA A CORDONE D'ANGOLO

(SVE NON ALTRIMENTI INDICATO)

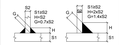

BULLONI classe 8.8

Ø BULL	12	14	16	20	24
Ø FORO	13.0	15.0	17.0	21.0	25.5
COPPIE SERR.to	conforme vigente normativa				
SIMBOLO	●	□	✦	✧	✎


SALDATURA DI PRIMA CLASSE PER GIUNTO a "T" A COMPLETA PENETRAZIONE

(PER TUTTE LE FLANGE DVE NON ALTRIMENTI INDICATO)



- LE STRUTTURE METALLICHE DOVRANNO AVERE LE CONTROFRECCE DI MONTAGGIO OVE PREVISTO

PARTICOLARE GANCI

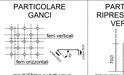

PARTICOLARE RIPRESA DI GETTO VERTICALE



PARTICOLARE SOVRAPPOSIZIONI



PARTICOLARE CHIUSURA DELLE GABBIE

SPECIFICA COPRIFERRO/QUOTATURA



SCHEMA PIEGATURE



D= 4Ø per Ø < 16 mm
D= 7Ø per Ø ≥ 16 mm

Piegare alle estremità tutte le armature correnti:
- a h-H > 50 per fondazione
- a h-H > 5 per travi/solette/scale
(salvo indicazione maggiore di esercizio)

CALCESTRUZZO

Calcestruzzo per	Magrone	Fondazione Diconnesi	Strutture in elevazione
Classe di resistenza (Fck/Rck)	C12/15	C28/35	C35/45
Classe esposizione ambientale	-	XC2	XC2	XC2
Cemento tipo	42.5N	42.5N	42.5N	42.5N
Rapporto max acqua/cemento	CONFORME ALLA NORMATIVA VIGENTE			
Contenuto min. cemento Kg/m³				
Ø max inerti (mm)	-	16	16	16
Classe di consistenza	-	S4	S5	SCC
Copriferro netto (mm)	-	40	30	30
Copriferro netto controterra	≥ 40 mm			
Profondità permeazione acqua secondo ISO7031	< 20 mm			

ACCIAIO PER CEMENTO ARMATO

ACCIAIO TIPO B450C controllato in stabilimento e saldabile

PRESCRIZIONI NOTE GENERALI

- VERIFICARE TUTTE LE MISURE IN CANTIERE PRIMA DI EFFETTUARE L'ORDINATIVO DEI MATERIALI
- VERIFICARE TUTTE LE MISURE E I FORI CON IL PROGETTO ARCHITETTONICO E IMPIANTISTICO
- LE STRUTTURE METALLICHE DOVRANNO ESSERE REALIZZATE DA PERSONALE QUALIFICATO IN OPERA SECONDO LE PRESCRIZIONI DEL PRODUTTORE DELLE RESINE NELLE CONDIZIONI AMBIENTALI IDONEE E PREVIA PERFETTA PULIZIA DEL FORO
-IN SEGUITO ALLO STRIP-OUT VERIFICARE GEOMETRIA E DIMENSIONI DELLE STRUTTURE INTERESSATE DAGLI INTERVENTI IN CANTIERE
-VERIFICA PREVENTIVA/INTERVENTI/ATTUALE DELLE STRUTTURE ESISTENTI E LE FASI OPERATIVE PRIMA DI DEMOLIRE
-PER LE DEMOLIZIONI DEI SOLAI PROCEDERE PER AREE LIMITATE VERIFICANDONE LA STABILITA' PRIMA DI PROCEDERE IN ALTRE ZONE
-PER LE DEMOLIZIONI PREVEDERE OPPORTUNE OPERE PROVVISIONALI E PUNTELLAZIONE

CUP F18H22000220005 - CIG 9210532374



UNIVERSITA' DEGLI STUDI DI BERGAMO
EX CASERMA GUARDIA DI FINANZA

Progetto di investimento relativo all'intervento di ristrutturazione e rifunzionalizzazione del complesso immobiliare di Via dello Statuto, n. 21 - Bergamo - Corpo C) - "Residenze"

PROGETTO ESECUTIVO

COMMITTENZA
Università degli studi di Bergamo
Area Infrastrutture - Settore Infrastrutture
via Salvecchio 19, 24129 Bergamo

RESPONSABILE UNICO DEL PROCEDIMENTO
Ing. Marta Sabbatini

RTP DI PROGETTAZIONE

CAPOGRUPPO MANDATARIA

Studio Arkam S.p.A.
Ingegneria, architettura ed urbanistica specialistica; progettazione edile-architettonica e strutturale; direzione lavori; coordinatore fase di progettazione

Responsabile integrazione tra le prestazioni specialistiche & PM
Ing. Alessandro Artuso

Project Coordinator & CDE Manager (Gestione professionista)
Ing. Filippo Bee

Esperto in sistemi elettr.
Ing. Andrea Stanchiero

BIM Manager
Geom. Marika Riccabene

Progettazione ambientale
Ing. Laura Della Valle

Progettazione architettonica
Arch. Andrea Chiarelli
Arch. Laura Von Dellemann

Coordinatore della Sicurezza in fase di Progettazione
Geom. Moreno Gazetto

MANDANTI

ICONIA Ingegneria Civile S.r.l.

Progettazione strutturale
Ing. Bonj Friso
Ing. Domenico D'Anza

Energo S.r.l.

Responsabile progettazione impianti meccanici, elettrici, idrico sanitari
Certificazione energetica
Professionista antincendio
Arch. Denis Zuin

Dott. Geol. Paolo Corrado Geologo


TITOLO DEL DOCUMENTO: STRUTTURE — SCALA: VAR

NUOVE CONTROPARETI-DETTAGLI CARPENTERIA 3 DI 3


CODICE: C1088 (Commessa) E (Fase) ST (Disciplina) DET (Set) 00 (Livello) 302 (Numero) r00 (Revisione)

Revisione	Data	Motivo	Redatto	Controllato	Approvato
00	15/10/2026	Prima emissione	RM	MG	DD


Pianta Controparete CP07
Scala 1 : 50

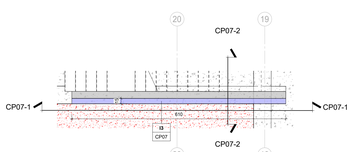

Pianta Controparete CP08
Scala 1 : 50

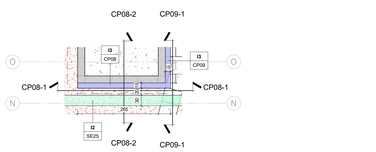

Pianta Controparete CP09
Scala 1 : 50

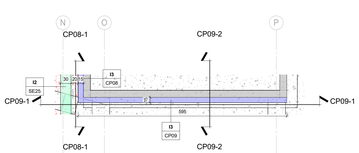

Pianta Controparete CP10
Scala 1 : 50

