


PIANTA VASCA ST-B2
SCALA 1:50

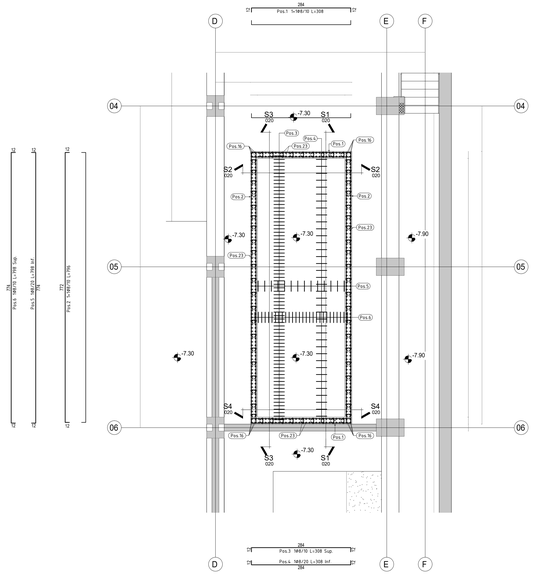


PIANTA VASCA ST-B1
SCALA 1:50

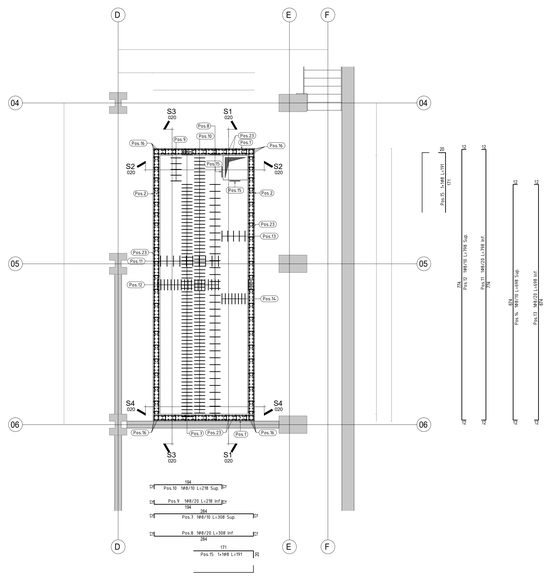



KEY-PLAN
SCALA 1:500

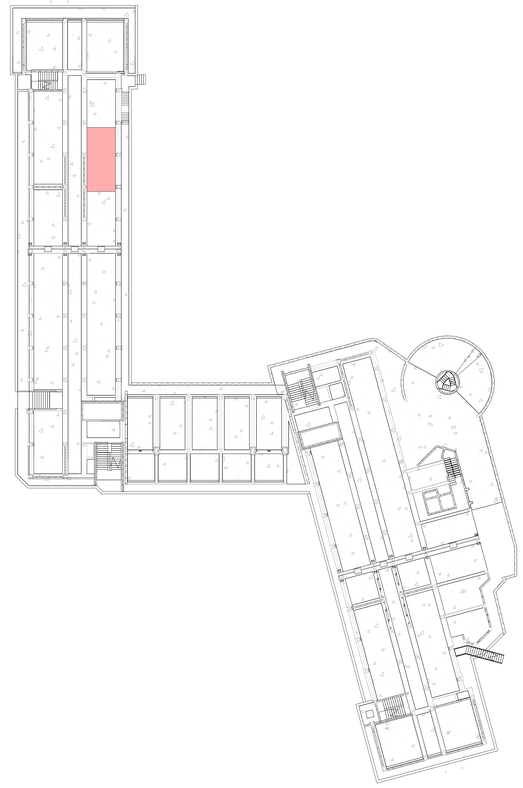

KEY-SECTION
SCALA 1:400

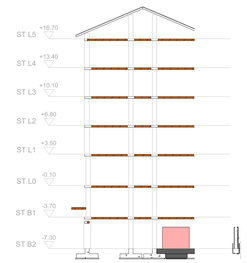

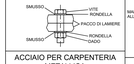NODI BULLONATI

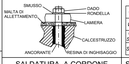
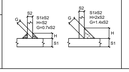
INGHISAGGI CHIMICI


BULLONI *classe 8.8*

Ø BULL	12	14	16	20	24
Ø FORO	13.0	15.0	17.0	21.0	25.5
COPRIF. SERR.min	conforme vigente normativa				
SIMBOLO	●	□	▲	⊙	ϕ

ACCIAIO PER CARPENTERIA METALLICA
- *Carpenteria metallica: S275JR zincato*
- *Zincatura a caldo*
- *Bullonatura: classe nelle zone di saldatura in opera highstrength chimici*
- *Connessori certificate C2 con resina TIPO HILTI HIT RE500 V4 e barra filettata classe 8.8*

SALDATURA A CORDONE D'ANGOLO
(OVE NON ALTRIMENTI INDICATO)




SALDATURA DI PRIMA CLASSE PER GIUNTO A "T" A COMPLETA PENETRAZIONE
(PER TUTTE LE PLANARI OVE NON ALTRIMENTI INDICATO)




CLASSE DI ESECUZIONE SECONDO UNIEN1090

Classe di conseguenza	*CC3*
Categoria di servizio	*SC1*
Categoria di produzione	*PC2*
Classe di esecuzione	*EXC3*

- *LE STRUTTURE METALLICHE DOVRANNO AVERE LE CONTROFRECCE DI MONTAGGIO OVE PREVISTO*

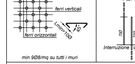PARTICOLARE GANCI

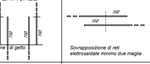
PARTICOLARE RIPRESA DI GETTO VERTICALE


PARTICOLARE SOVRAPPOSIZIONI

PARTICOLARE CHIUSURA DELLE GABBIE

SPECIFICA COPRIFERRO/QUOTATURA


SCHEMA PIEGATURE



CALCESTRUZZO

Calcestruzzo per	Magrone	Fondazioni	Orizzontali	Strutture in elevazione
Classe di resistenza (Rck/fck)	C12/15	C28/35	C35/45	C35/45
Classe esposizione ambientale	-	XC2	XC2	XC2
Cemento tipo	42.5N	42.5N	42.5N	42.5N
Rapporto max acqua/cemento	CONFORME ALLA NORMATIVA VIGENTE			
Contenuto min. cemento (kg/m³)	CONFORME ALLA NORMATIVA VIGENTE			
Ø max inerti (mm)	-	16	16	16
Classe di consistenza	-	S4	S5	SCC
Copriferro netto (mm)	-	40	30	30
Copriferro netto controterra	≥ 40 mm			
Profondità permeazione acqua secondo ISO7031	< 20 mm			


ACCIAIO PER CEMENTO ARMATO
ACCIAIO TIPO B450C controllato in stabilimento e saldabile

PRESCRIZIONI NOTE GENERALI
- *VERIFICARE TUTTE LE MISURE IN CANTIERE PRIMA DI EFFETTUARE L'ORDINATIVO DEI MATERIALI*
- *VERIFICARE TUTTE LE MISURE DI OGNI DISEGNO, PROGETTO ARCHITETTONICO E IMPIANTISTICO*
- *LE STRUTTURE METALLICHE DOVRANNO ESSERE FORNITE DAL PRODUTTORE CERTIFICATO IN OPERA SECONDO LE PRESCRIZIONI DEL PRODUTTORE DELLE RESINE NELLE CONDIZIONI AMBIENTALI IDONEE E PREVIA PERFETTA PULIZIA DEL FORO*
- *IN SEGUITO ALLO STRIP-OUT VERIFICARE GEOMETRIA E DIMENSIONI DELLE STRUTTURE INTERESSATE DAGLI INTERVENTI IN CANTIERE*
- *VERIFICARE PREVENTIVAMENTE LA STABILITA' DELLE STRUTTURE ESISTENTI E LE FASI OPERATIVE PRIMA DI DEMOLIRE*
- *PER LE DEMOLIZIONI DEI SOLAI PROCEDERE PER AREE LIMITATE VERIFICANDONE LA STABILITA' PRIMA DI PROCEDERE IN ALTRE ZONE*
- *PER LE DEMOLIZIONI PREVEDERE OPPORTUNE OPERE PROVVISIONALI E PUNTELLATURE*


SEZIONE VASCA S1
SCALA 1:50

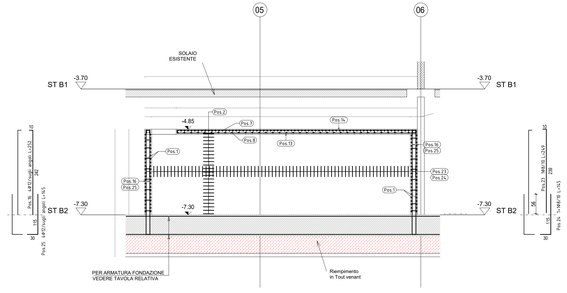


SEZIONE VASCA S3
SCALA 1:50

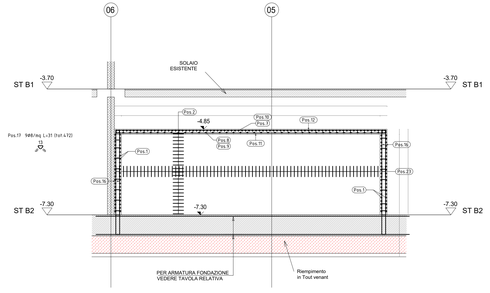

SEZIONE VASCA S4
SCALA 1:50

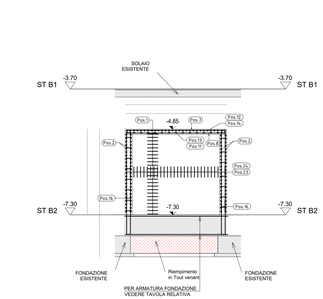

SEZIONE VASCA S2
SCALA 1:50

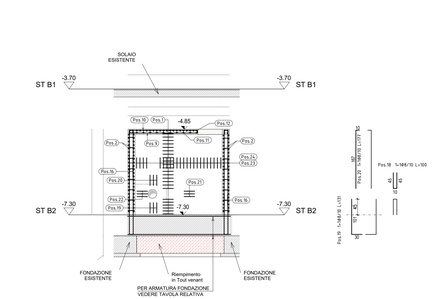

CUP F18H22000220005 - CIG 9210532374



UNIVERSITA' DEGLI STUDI DI BERGAMO

EX CASERMA GUARDIA DI FINANZA

Progetto di investimento relativo all'intervento di ristrutturazione e rifunzionalizzazione del complesso immobiliare di Via dello Statuto, n. 21 - Bergamo - Corpo C) - "Residenze"

PROGETTO ESECUTIVO

COMMITTENZA
Università degli studi di Bergamo
Area Infrastrutture - Settore Infrastrutture
via Salvecchio 19, 24129 Bergamo

RESPONSABILE UNICO DEL PROCEDIMENTO
Ing. Marta Sabbatini

RTP DI PROGETTAZIONE

CAPOGRUPPO MANDATARIA

Studio Alberi S.p.A.
Coordinamento progettuale ed integrazione specialistica architettonica e strutturale, progettazione in fase di progettazione

Responsabile integrazione tra le prestazioni specialistiche & PM
Ing. Alessandro Arfuso

Project Coordinator & CDE Manager (Gruppo professionista)
Ing. Filippo Bee

BIM Manager
Geom. Marika Riccobene

Progettazione architettonica
Arch. Andrea Chiarotto
Arch. Laura Von Dellemann

Esperto in sistemi edilizi
Ing. Andrea Stabilcheo

Progettazione ambientale
Ing. Laura Dalla Valle

Coordinatore della Sicurezza in fase di Progettazione
Geom. Moreno Gazzetto

MANDANTI

ICONIA Ingegneria Civile S.r.l.

Progettazione strutturale
Ing. Ronj Frisc
Ing. Domenico D'Anza

Energia S.r.l.

Responsabile progettazione impianti meccanici, elettrici, idrico sanitari e antincendio antincendio
Professionista antincendio
Arch. Denis Zuin

Dott. Geol. Paolo Corrale Geologo

TITOLO DEL DOCUMENTO:

STRUTTURE
VASCA-DETTAGLI ARMATURA CARPENTERIA

SCALA 1:50

CODICI: C1088 | E | ST | DET | 00 | 0021 | r00
Commessa | Fase | Disciplina | Set | Livello | Numero | Revisione

Revisione	Data	Motivo	Redatto	Controllato	Approvato
00	19/10/2206	Prima consegna	AV	ME	DS