


SEZIONE G-G CONTROPARETE CP06
SCALA 1:50

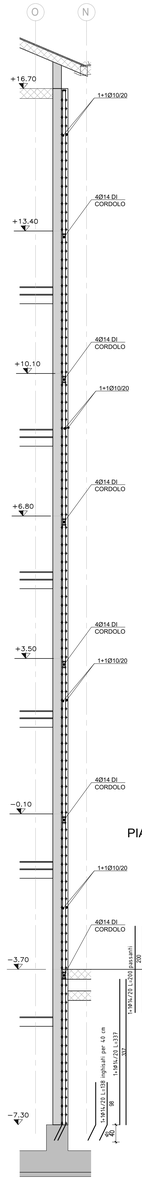


SEZIONE H-H CONTROPARETE CP08
SCALA 1:50

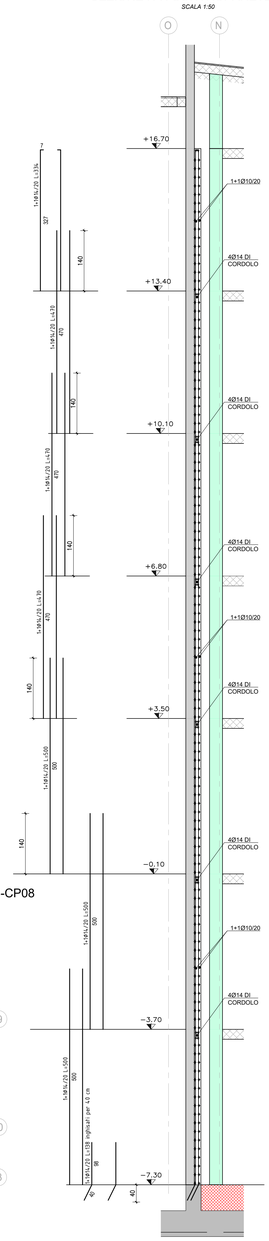


SEZIONE F-F CONTROPARETE CP07
SCALA 1:50

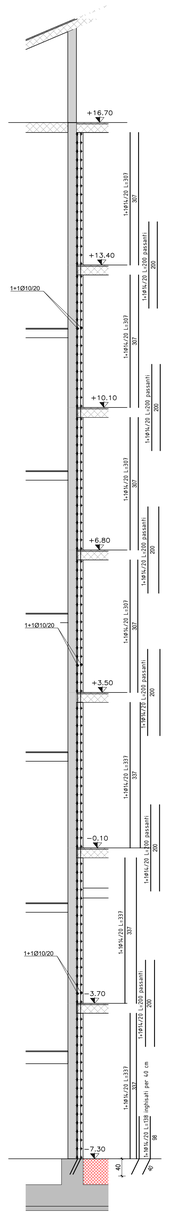


SEZIONE I-I CONTROPARETE CP09
SCALA 1:50

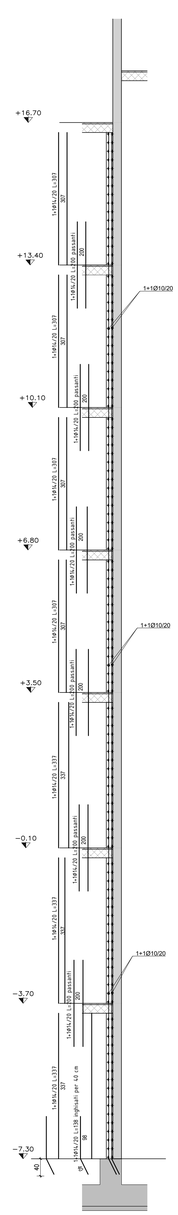


SEZIONE L-L CONTROPARETE CP09
SCALA 1:50

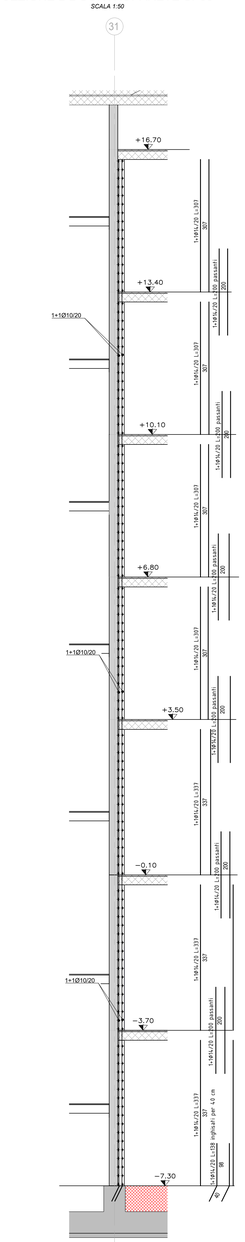


KEY PLAN
SCALA 1:400

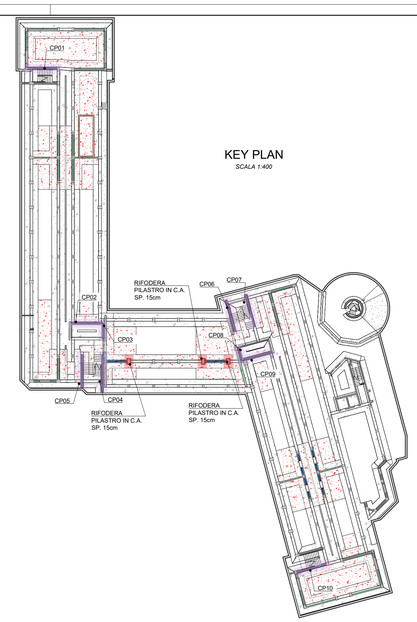


PIANTA CONTROPARETI CP06-CP08
SCALA 1:50

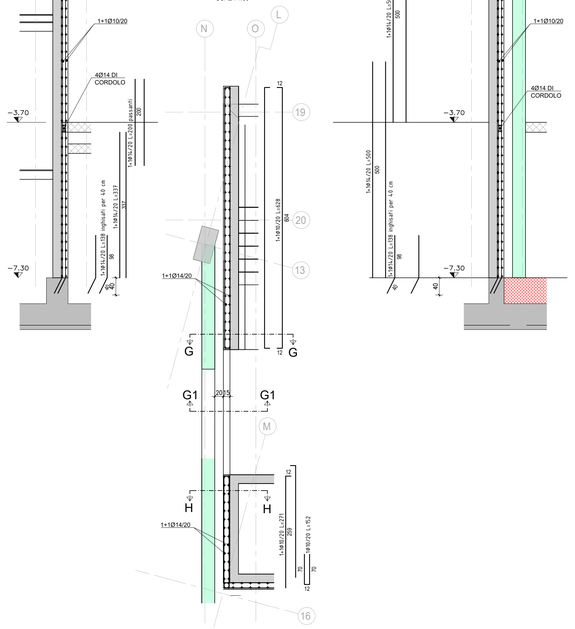


PIANTA CONTROPARETE CP07
SCALA 1:50

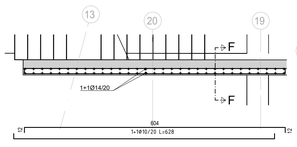

PIANTA CONTROPARETE CP09
SCALA 1:50

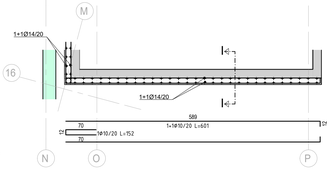


PIANTA CONTROPARETE CP10
SCALA 1:50

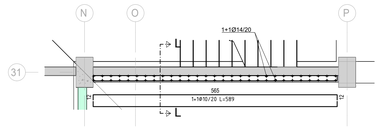

SEZIONE G1-G1 CORDOLO DI COLLEGAMENTO A LIVELLO SOLAIO TRA LE CONTROPARETI CP06 E CP08
SCALA 1:50


DETTAGLIO TIPOLOGICO INGHISAGGI NUOVE CONTROPARETI
SEZIONE
SCALA 1:25

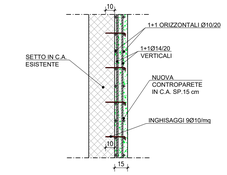

DETTAGLIO TIPOLOGICO NUOVE CONTROPARETI IN C.A.
PIANTA
SCALA 1:10



NODI BULLONATI

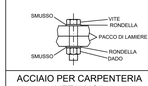


ACCIAIO PER CARPENTERIA METALLICA
- *Carpenteria metallica: S275JR zincato*
- *Zincatura a caldo*
- *Zincatura a freddo nelle zone di saldatura in opera*
- *Inghisaggi chimici:*
  Connessioni certificate C2 con resina TIPO HILTI HIT RE500 V4 e barre filettate classe 8.8


CLASSE DI ESECUZIONE SECONDO UNIEN1090

Classe di conseguenza	*CC3*
Categoria di servizio	*SC1*
Categoria di produzione	*PC2*
Classe di esecuzione	*EXC3*

INGHISAGGI CHIMICI

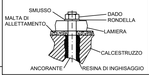


SALDATURA A CORDONE D'ANGOLO
(OVE NON ALTRIMENTI INDICATO)

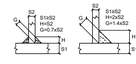

BULLONI
classe 8.8


Ø BULL	*12*	*14*	*16*	*20*	*24*
Ø FORO	*13.0*	*15.0*	*17.0*	*21.0*	*25.5*
COPPIE SERR.(Nm)	*conforme vigente normativa*				
SIMBOLO					

SALDATURA DI PRIMA CLASSE PER GIUNTO A "T" A COMPLETA PENETRAZIONE
(PER TUTTE LE FLANGE OVE NON ALTRIMENTI INDICATO)

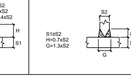

- *LE STRUTTURE METALLICHE DOVRANNO AVERE LE CONTROFRECCE DI MONTAGGIO OVE PREVISTO*


PARTICOLARE GANCI

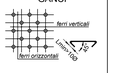


PARTICOLARE RIPRESA DI GETTO VERTICALE



PARTICOLARE SOVRAPPOSIZIONI

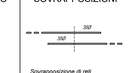

PARTICOLARE CHIUSURA DELLE GABBIE

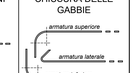


SPECIFICA COPRIFERRO/QUOTATURA



CALCESTRUZZO

Calcestruzzo per	*Magrone*	*Fondazione*	*Orizzontale*	*Strutture in elevazione*
Classe di resistenza (Fck/Rck)	*C12/15*	*C28/35*	*C35/45*	*C35/45*
Classe esposizione ambientale	-	*XC2*	*XC2*	*XC2*
Cemento tipo	*42.5N*	*42.5N*	*42.5N*	*42.5N*
Rapporto max acqua/cemento	*CONFORME ALLA NORMATIVA VIGENTE*			
Contenuto min. cemento (kg/m³)				
Ø max inerti (mm)	-	*16*	*16*	*16*
Classe di consistenza	-	*S4*	*S5*	*SCC*
Copriferro netto (mm)	-	*40*	*30*	*30*
Copriferro netto controterra	*≥ 40 mm*			
Profondità permeazione acqua secondo ISO7031	*< 20 mm*			

SCHEMA PIEGATURE

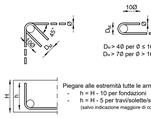

D≥h> 40 per Ø ≤ 16 mm
D≥h> 70 per Ø > 16 mm

Piegare alle estremità tutte le armature correnti:
- h = H - 5 per fondazioni
- h = H - 5 per travi/solette/solai
(salvo indicazione maggiore di copriferro)

ACCIAIO PER CEMENTO ARMATO
ACCIAIO TIPO B450C controllato in stabilimento e saldabile

PRESCRIZIONI NOTE GENERALI
- *VERIFICARE TUTTE LE MISURE IN CANTIERE PRIMA DI EFFETTUARE L'ORDINATIVO DEI MATERIALI*
- *VERIFICARE TUTTE LE MISURE E I FORI CON IL PROGETTO ARCHITETTONICO E IMPIANTISTICO*
- *OVE PREVISTI FORETTI INGHISATI CON RESINA E TASSELLI CHIMICI DOVRANNO ESSERE POSTI IN OPERA SECONDO LE PRESCRIZIONI DEL PRODUTTORE DELLE RESINE NELLE CONDIZIONI AMBIENTALI IDONEE E PREVIA PERFETTA PULIZIA DEL FORO*
- *IN SEGUITO ALLO STRIP-OUT VERIFICARE GEOMETRIA E DIMENSIONI DELLE STRUTTURE INTERESSATE DAGLI INTERVENTI IN CANTIERE*
- *VERIFICARE PREVENTIVAMENTE LA STABILITA' DELLE STRUTTURE ESISTENTI E LE FASI OPERATIVE PRIMA DI DEMOLIRE*
- *PER LE DEMOLIZIONI DEI SOLAI PROCEDERE PER AREE LIMITATE VERIFICANDONE LA STABILITA' PRIMA DI PROCEDERE IN ALTRE ZONE*
- *PER LE DEMOLIZIONI PREVEDERE OPPORTUNE OPERE PROVVISIONALI E PUNTELLAZIONE*

CUP F18H22000220005 - CIG 9210532374



UNIVERSITA' DEGLI STUDI DI BERGAMO
EX CASERMA GUARDIA DI FINANZA

Progetto di investimento relativo all'intervento di ristrutturazione e rifunzionalizzazione del complesso immobiliare di Via dello Statuto, n. 21 - Bergamo - Corpo C) - "Residenze"

PROGETTO ESECUTIVO

COMMITTENZA
Università degli studi di Bergamo
Area Infrastrutture - Settore Infrastrutture
via Salvecchio 19, 24129 Bergamo

RESPONSABILE UNICO DEL PROCEDIMENTO
Ing. Marta Sabbatini

RTP DI PROGETTAZIONE

CAPOGRUPPO MANDATARIA

Studio Alberi S.p.A.
Coordinamento progettuale ed integrazione tra le prestazioni di progettazione edile-architettonica e coordinamento della sicurezza in fase di progettazione

Responsabile integrazione tra le prestazioni specialistiche & PM
Ing. Alessandro Artuso

Project Coordinator & COE Manager (Giovane professionista)
Ing. Filippo Bee

Esperto in sistemi edilizi
Ing. Andrea Sbalchiero

BIM Manager
Geom. Marika Riccobene

Progettazione ambientale
Ing. Laura Dalla Valle

Progettazione architettonica
Arch. Andrea Chiarolini
Arch. Laura Von Dellemann

Coordinatore della Sicurezza in fase di Progettazione
Geom. Moreno Gazzetto

MANDANTI

ICONIA Ingegneria Civile S.r.l.
Progettazione strutturale
Ing. Romj Frino
Ing. Domenico D'Anza

Energo S.r.l.
Responsabile progettazione impianti meccanici, elettrici, idrico sanitari
Certificazione energetica
Professionista antincendio
Arch. Denis Zulin

Dott. Geol. Paolo Cornale Geologo

TITOLO DEL DOCUMENTO:
STRUTTURE
NUOVE CONTROPARETI-DETTAGLI ARMATURA 2 DI 2

SCALA 1:50 - 1:10

CODICE: C1088 | E | ST | DET | 00 | 0304 | r00
Commessa | Fase | Disciplina | Set | Livello | Numero | Revisione

Revisione	Data	Motivo	Redatto	Controllato	Approvato
00	19/10/2026	Prima emissione	AP	MG	DD