

PIANTA FONDAZIONI GIUNTO SETTO SE24

Scala 1 : 50

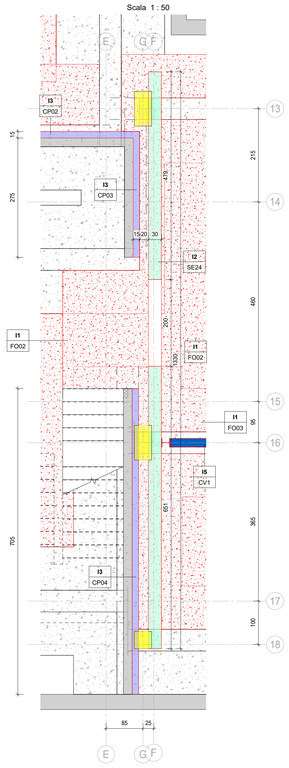


PIANTA DI PIANO GIUNTO SETTO SE24

Scala 1 : 50

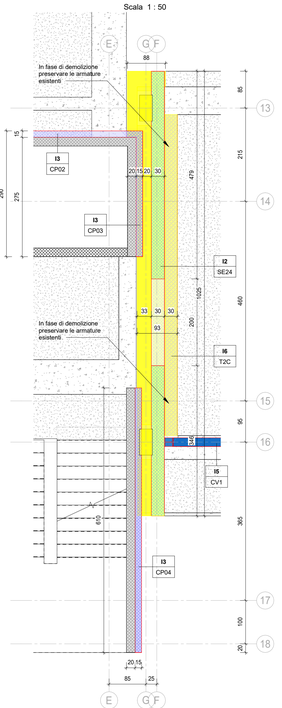


SE24-1 - SDF

Scala 1 : 50

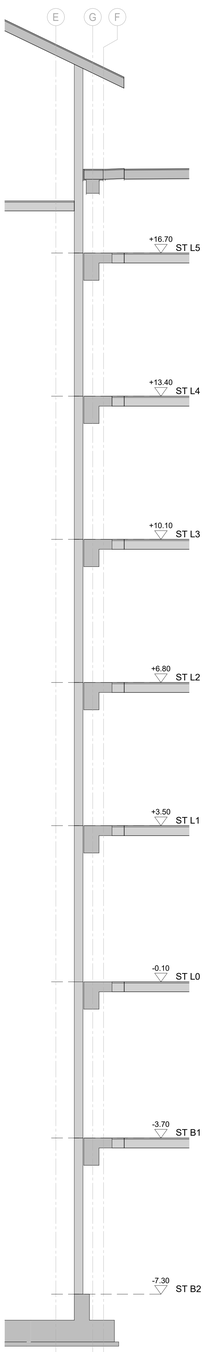


SE24-1 - COMPARATIVA

Scala 1 : 50

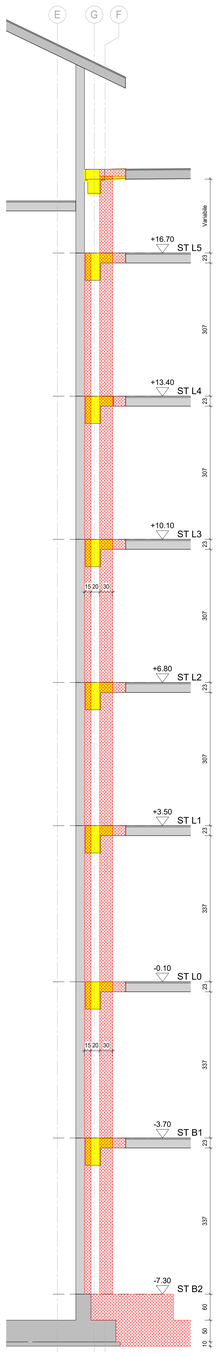


SE24-1 - PROGETTO

Scala 1 : 50

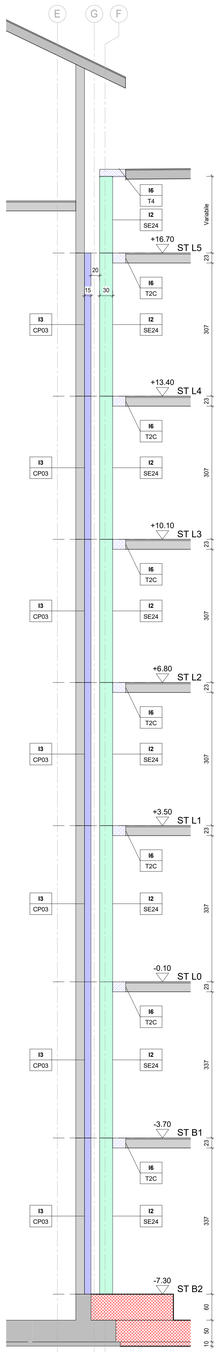

FASISTICA APERTURA GIUNTO PRIMA FASE

Scala 1 : 50

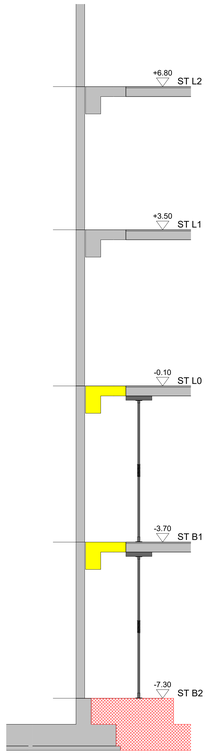

FASISTICA APERTURA GIUNTO


1) REALIZZAZIONE NUOVA PLATEA PREDISPONENDO I RICHIAMI DELLE NUOVE STRUTTURE VERTICALI IN ELEVAZIONE

2) PUNTELLAZIONE STRUTTURE ESISTENTI

3) DEMOLIZIONE TRATTO SOLAIO INTERESSATO DALL'INTERVENTO PER ALMENO DUE LIVELLI PRESERVANDONE LE ARMATURE ESISTENTI DA INGLOBARE NEI NUOVI SETTI

FASISTICA APERTURA GIUNTO SECONDA FASE

Scala 1 : 50

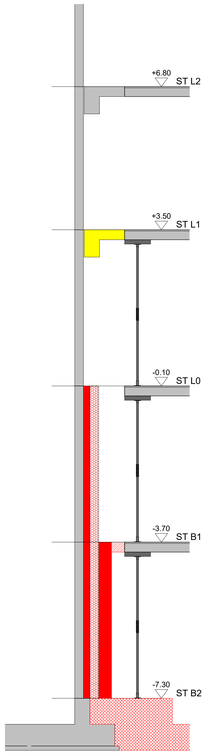


FASISTICA APERTURA GIUNTO

4) REALIZZAZIONE CONTROPARETE PRIMI DUE INTERPIANI, POSA DEL BLOCCO IN POLISTIROLO CHE FUNGERA' DA CASSERO A PERDERE PER LA REALIZZAZIONE DEL NUOVO SETTO RISPETTANDO LA DIMENSIONE DEL NUOVO GIUNTO

5) REALIZZAZIONE NUOVA PARETE E RELATIVA TRAVE DI SOLAIO DEL PRIMO INTERPIANO INGLOBANDO NEL GETTO LE ARMATURE PRESERVATE. IN CONTEMPORANEA PUNTELLAZIONE E DEMOLIZIONE DEL TRATTO DI SOLAIO SUPERIORE A QUELLO PRECEDENTEMENTE DEMOLITO

FASISTICA APERTURA GIUNTO TERZA FASE

Scala 1 : 50

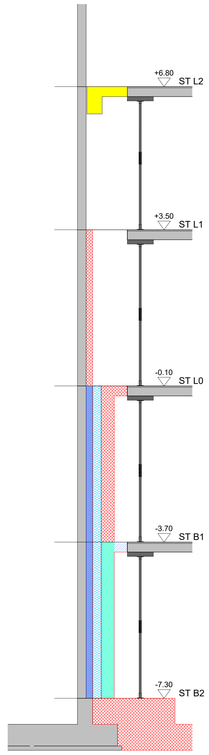

FASISTICA APERTURA GIUNTO

6) REALIZZAZIONE CONTROPARETE DEL TERZO INTERPIANO, POSA DEL BLOCCO IN POLISTIROLO CHE FUNGERA' DA CASSERO A PERDERE PER LA REALIZZAZIONE DEL NUOVO SETTO RISPETTANDO LA DIMENSIONE DEL NUOVO GIUNTO

7) REALIZZAZIONE NUOVA PARETE E RELATIVA TRAVE DI SOLAIO DEL SECONDO INTERPIANO INGLOBANDO NEL GETTO LE ARMATURE PRESERVATE. IN CONTEMPORANEA PUNTELLAZIONE E DEMOLIZIONE DEL TRATTO DI SOLAIO SUPERIORE A QUELLO PRECEDENTEMENTE DEMOLITO

8) PER I SUCCESSIVI PIANI RIPETERE LA FASE 6 FINO A COPERTURA

LEGENDA STATO DI FATTO:

- STRUTTURE SOTTOSTANTE
- STRUTTURE IN ELEVAZIONE

LEGENDA INTERVENTI:

- I1 - NUOVA FONDAZIONE
- I2 - NUOVI SETTI IN ELEVAZIONE
- I2 - NUOVI SETTI SOTTOSTANTI
- I3 - NUOVA RIFODERA C.A. IN ELEVAZIONE
- I3 - NUOVA RIFODERA C.A. SOTTOSTANTE
- I4 - VASCA ANTINCEDIO NUOVI MURI IN ELEVAZIONE
- I4 - VASCA ANTINCEDIO NUOVI MURI SOTTOSTANTI
- I4 - VASCA ANTINCEDIO NUOVA SOLETTA DI COPERTURA
- I5 - NUOVI CONTROVENTI IN ACCIAIO
- I6 - NUOVA TRAVE IN C.A.
- I7 - NUOVA RIFODERA PILASTRI C.A. IN ELEVAZIONE
- I7 - NUOVA RIFODERA PILASTRI C.A. SOTTOSTANTE
- I8 - SHOCK TRANSMITTER
- I9 - PIASTRA CHIUSURA GIUNTO
- I10 - NUOVA SCALA IN ACCIAIO
- I11 - NUOVA SOLETTA IN CALCESTRUZZO IN SPESSORE SOLAIO ESISTENTE


ETICHETTA IDENTIFICAZIONE INTERVENTO/TIPOLOGIA

Ix — Identificativo intervento
XXXX — Identificativo tipologia

LEGENDA COMPARATIVA

- NUOVE COSTRUZIONI (SEZIONATO)
- NUOVE COSTRUZIONI (PROIEZIONI)
- DEMOLIZIONI
- DEMOLIZIONI (PROIEZIONI)

NODI BULLONATI

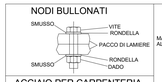

ACCIAIO PER CARPENTERIA METALLICA

- Carpenteria metallica: S275JR zincato
- Zincatura a caldo
- Zincatura a freddo nelle zone di saldatura in opera
- Inghisaggi chimici:
Connessioni certificate C2 con resina TIPO HILTI HIT RE500 V4 e barre filettate classe 8.8

CLASSE DI ESECUZIONE SECONDO UNIEN1090


Classe di conseguenza	CC3
Categoria di servizio	SC1
Categoria di produzione	PC2
Classe di esecuzione	EXC3

INGHISAGGI CHIMICI



SALDATURA A CORDONE D'ANGOLO

(OVE NON ALTRIMENTI INDICATO)

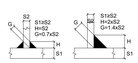


BULLONI

classe 8.8


Ø BULL	12	14	16	20	24
Ø FORO	13.0	15.0	17.0	21.0	25.5
COPPIE SERR.[N•m]	conforme vigente normativa				
SIMBOLO	◆	□	➔	✣	⚡

SALDATURA DI PRIMA CLASSE PER GIUNTO a "T" A COMPLETA PENETRAZIONE

(PER TUTTE LE FLANGE OVE NON ALTRIMENTI INDICATO)

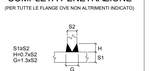

PARTICOLARE GANCI

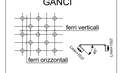


min 9\18/mq su tutti i muri

PARTICOLARE RIPRESA DI GETTO VERTICALE



PARTICOLARE SOVRAPPOSIZIONI

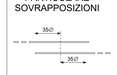


Sovrapposizione di reti elettrosaldate minimo due maglie

PARTICOLARE CHIUSURA DELLE GABBIE




SPECIFICA COPRIFERRO/QUOTATURA

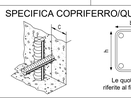

CALCESTRUZZO

Calcestruzzo per	Magrone	Fondazione	Orizzontale	Strutture in elevazione
Classe di resistenza (Fck/Rck)	C12/15	C28/35	C35/45	C35/45
Classe esposizione ambientale	-	XC2	XC2	XC2
Cemento tipo	42.5N	42.5N	42.5N	42.5N
Rapporto max acqua/cemento	CONFORME ALLA NORMATIVA VIGENTE			
Contenuto min. cemento (kg/m³)				
Ø max inerti (mm)	-	16	16	16
Classe di consistenza	-	S4	S5	SCC
Copriferro netto (mm)	-	40	30	30
Copriferro netto controterra	≥ 40 mm			
Profondità permeazione acqua secondo ISO7031	< 20 mm			

SCHEMA PIEGATURE

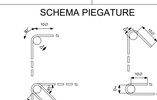

Dₘ > 40 per Ø ≤ 16 mm
Dₘ > 70 per Ø > 16 mm

ACCIAIO PER CEMENTO ARMATO

ACCIAIO TIPO B450C controllato in stabilimento e saldabile

PRESCRIZIONI NOTE GENERALI

- VERIFICARE TUTTE LE MISURE IN CANTIERE PRIMA DI EFFETTUARE L'ORDINATIVO DEI MATERIALI
- VERIFICARE TUTTE LE MISURE E I FORI CON IL PROGETTO ARCHITETTONICO E IMPIANTISTICO
- OVE PREVISTI FIORETTI INGHISATI CON RESINA E TASSELLI CHIMICI DOVRANNO ESSERE POSTI IN OPERA SECONDO LE PRESCRIZIONI DEL PRODUTTORE DELLE RESINE NELLE CONDIZIONI AMBIENTALI IDONEE E PREVIA PERFETTA PULIZIA DEL FORO
-IN SEGUITO ALLO STRIP-OUT VERIFICARE GEOMETRIA E DIMENSIONI DELLE STRUTTURE INTERESSATE DAGLI INTERVENTI IN CANTIERE
-VERIFICA PREVENTIVAMENTE LA STABILITA' DELLE STRUTTURE ESISTENTI E LE FASI OPERATIVE PRIMA DI DEMOLIRE
-PER LE DEMOLIZIONI DEI SOLAI PROCEDERE PER AREE LIMITATE VERIFICANDONE LA STABILITA' PRIMA DI PROCEDERE IN ALTRE ZONE
-PER LE DEMOLIZIONI PREVEDERE OPPORTUNE OPERE PROVVISIONALI E PUNTELLAZIONE



CUP F18H22000220005 - CIG 9210532374

UNIVERSITA' DEGLI STUDI DI BERGAMO
EX CASERMA GUARDIA DI FINANZA

Progetto di investimento relativo all'intervento di ristrutturazione e rifunzionalizzazione del complesso immobiliare di Via dello Statuto, n. 21 - Bergamo - Corpo C) - "Residenze"

PROGETTO ESECUTIVO

COMMITTENZA
Università degli studi di Bergamo
Area Infrastrutture - Settore Infrastrutture
via Salvecchio 19, 24129 Bergamo

RESPONSABILE UNICO DEL PROCEDIMENTO
Ing. Marta Sabbatini

RTP DI PROGETTAZIONE

CAPOGRUPPO MANDATARIA

Studio Alteri S.p.A.
Progettazione architettonica ed ingegneria specialistica, progettazione edile-architettonica e coordinamento della sicurezza in fase di progettazione

Responsabile integrazione tra le prestazioni specialistiche & PM
Ing. Alessandro Artuso

Project Coordinator & COE Manager (Giovane professionista)
Ing. Filippo Bee

BIM Manager
Geom. Marika Riccobene

Progettazione architettonica
Arch. Andrea Chiarolini
Arch. Laura Von Dellemann

Esperto in sistemi edilizi
Ing. Andrea Sbalchiero

Progettazione ambientale
Ing. Laura Dalla Valle

Coordinatore della Sicurezza in fase di Progettazione
Geom. Moreno Gazzetto

MANDANTI

ICONIA Ingegneria Civile S.r.l.

Progettazione strutturale
Ing. Romj Frixo
Ing. Domenico D'Anza

Energo S.r.l.

Responsabile progettazione impianti meccanici, elettrici, idrico sanitari Certificazione energetica
Professionista antincendio
Arch. Denis Zuin

Dott. Geol. Paolo Cornale Geologo

TITOLO DEL DOCUMENTO: STRUTTURE — SCALA: VAR

APERTURA GIUNTO-DETTAGLI E FASISTICA 1 DI 2

CODICE: C1088 (Commessa) E (Fase) ST (Disciplina) DET (Set) 00 (Livello) 401 (Numero) r00 (Revisione)

Revisione	Data	Motivo	Redatto	Controllato	Approvato
00	19/10/2026	Prima emissione	RM	MG	DD