
CUP F18H22000220005 - CIG 9210532374

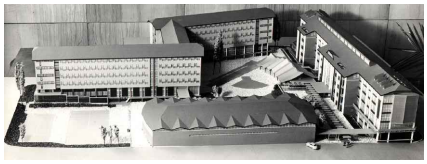

UNIVERSITA' DEGLI STUDI DI BERGAMO

EX CASERMA GUARDIA DI FINANZA

Progetto di investimento relativo all'intervento di ristrutturazione e rifunzionalizzazione del complesso immobiliare di Via dello Statuto, n. 21 - Bergamo - Corpo C) - "Residenze"

PROGETTO ESECUTIVO

COMMITTENZA
Università degli studi di Bergamo
Area Infrastrutture - Settore Infrastrutture
via Salvecchio 19, 24129 Bergamo

RESPONSABILE UNICO DEL PROCEDIMENTO
Ing. Marta Sabbatini

RTP DI PROGETTAZIONE

CAPOGRUPPO MANDATARIA

Studio Altieri S.p.A.
Coordinamento progettuale ed integrazioni specialistiche, progettazione edile-architettonica e coordinamento della sicurezza in fase di progettazione

Responsabile integrazione tra le prestazioni specialistiche & PM
Ing. Alessandro Artuso

Project Coordinator & CDE Manager (Giovane professionista)
Ing. Filippo Bee

BIM Manager
Geom. Marika Riccobene

Progettazione architettonica
Arch. Andrea Chiarolini
Arch. Laura Von Dellemann

Esperto in sistemi edilizi
Ing. Andrea Sbalchiero

Progettazione ambientale
Ing. Laura Dalla Valle

Coordinatore della Sicurezza in fase di Progettazione
Geom. Moreno Gazzetto

MANDANTI

ICONIA Ingegneria Civile S.r.l.

Progettazione strutturale
Ing. Romj Friso
Ing. Domenico D'Anza

Energo S.r.l.

Responsabile progettazione impianti meccanici, elettrici, idrico sanitari
Certificazione energetica
Professionista antincendio
Arch. Denis Zuin

Dott. Geol. Paolo Cornale Geologo

TITOLO DEL DOCUMENTO:

ARCHITETTURA
PARTIZIONI ORIZZONTALI

SCALA 1:10


CODICE:

C1088	E	AR	DET	00	010	R00
Commessa	Fase	Disciplina	Set	Livello	Numero	Revisione


Revisione	Data	Motivo	Redatto	Controllato	Approvato
00	OTTOBRE 2026	EMISSIONE PE	X.X.	X.X.	A.A.

COI


CHIUSURE ORIZZONTALI INFERIORI
DI PROGETTO

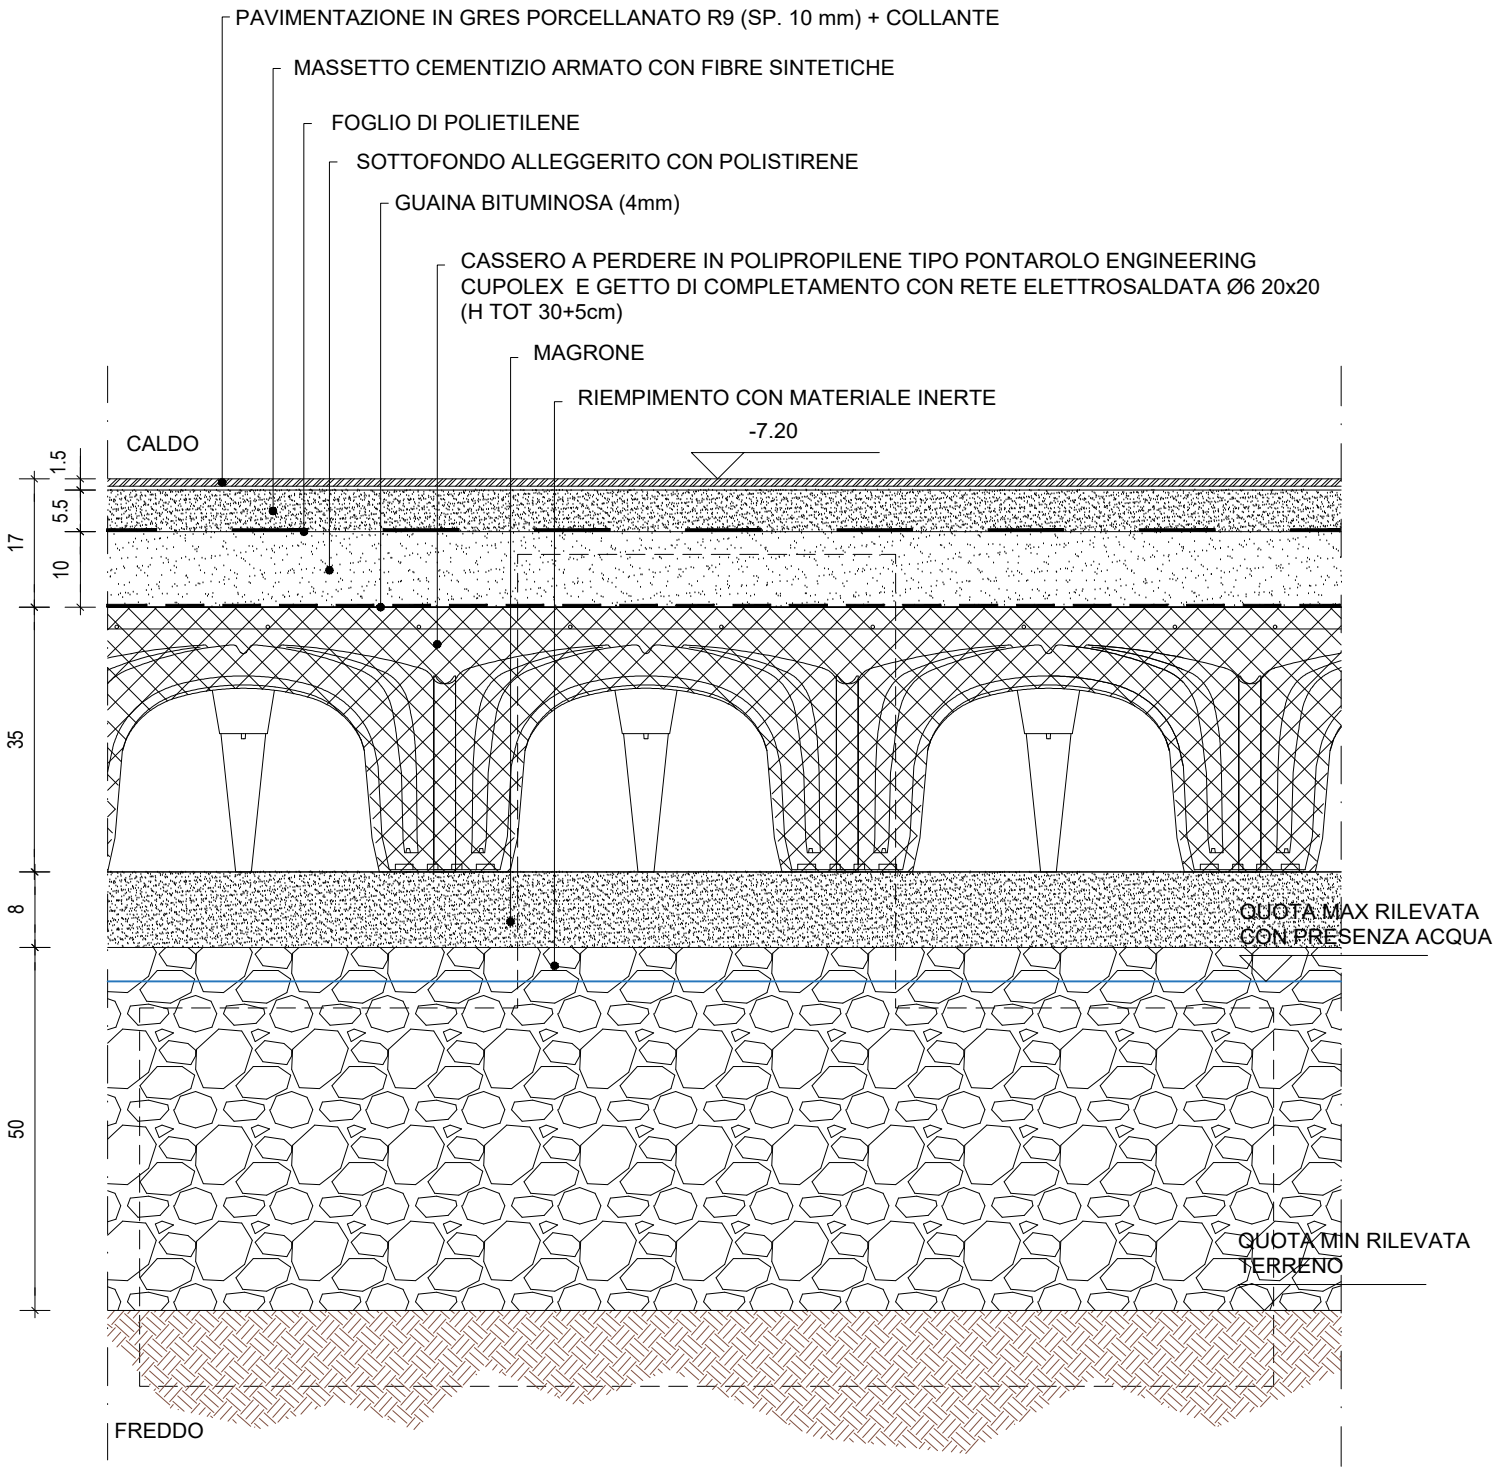


CODICE	COI1+GRE
VISTA	SEZIONE VERTICALE 1:10
DESCRIZIONE	PAVIMENTAZIONE CON FINITURA IN GRES
POSIZIONE	PIANO SECONDO INTERRATO
NOTE	-

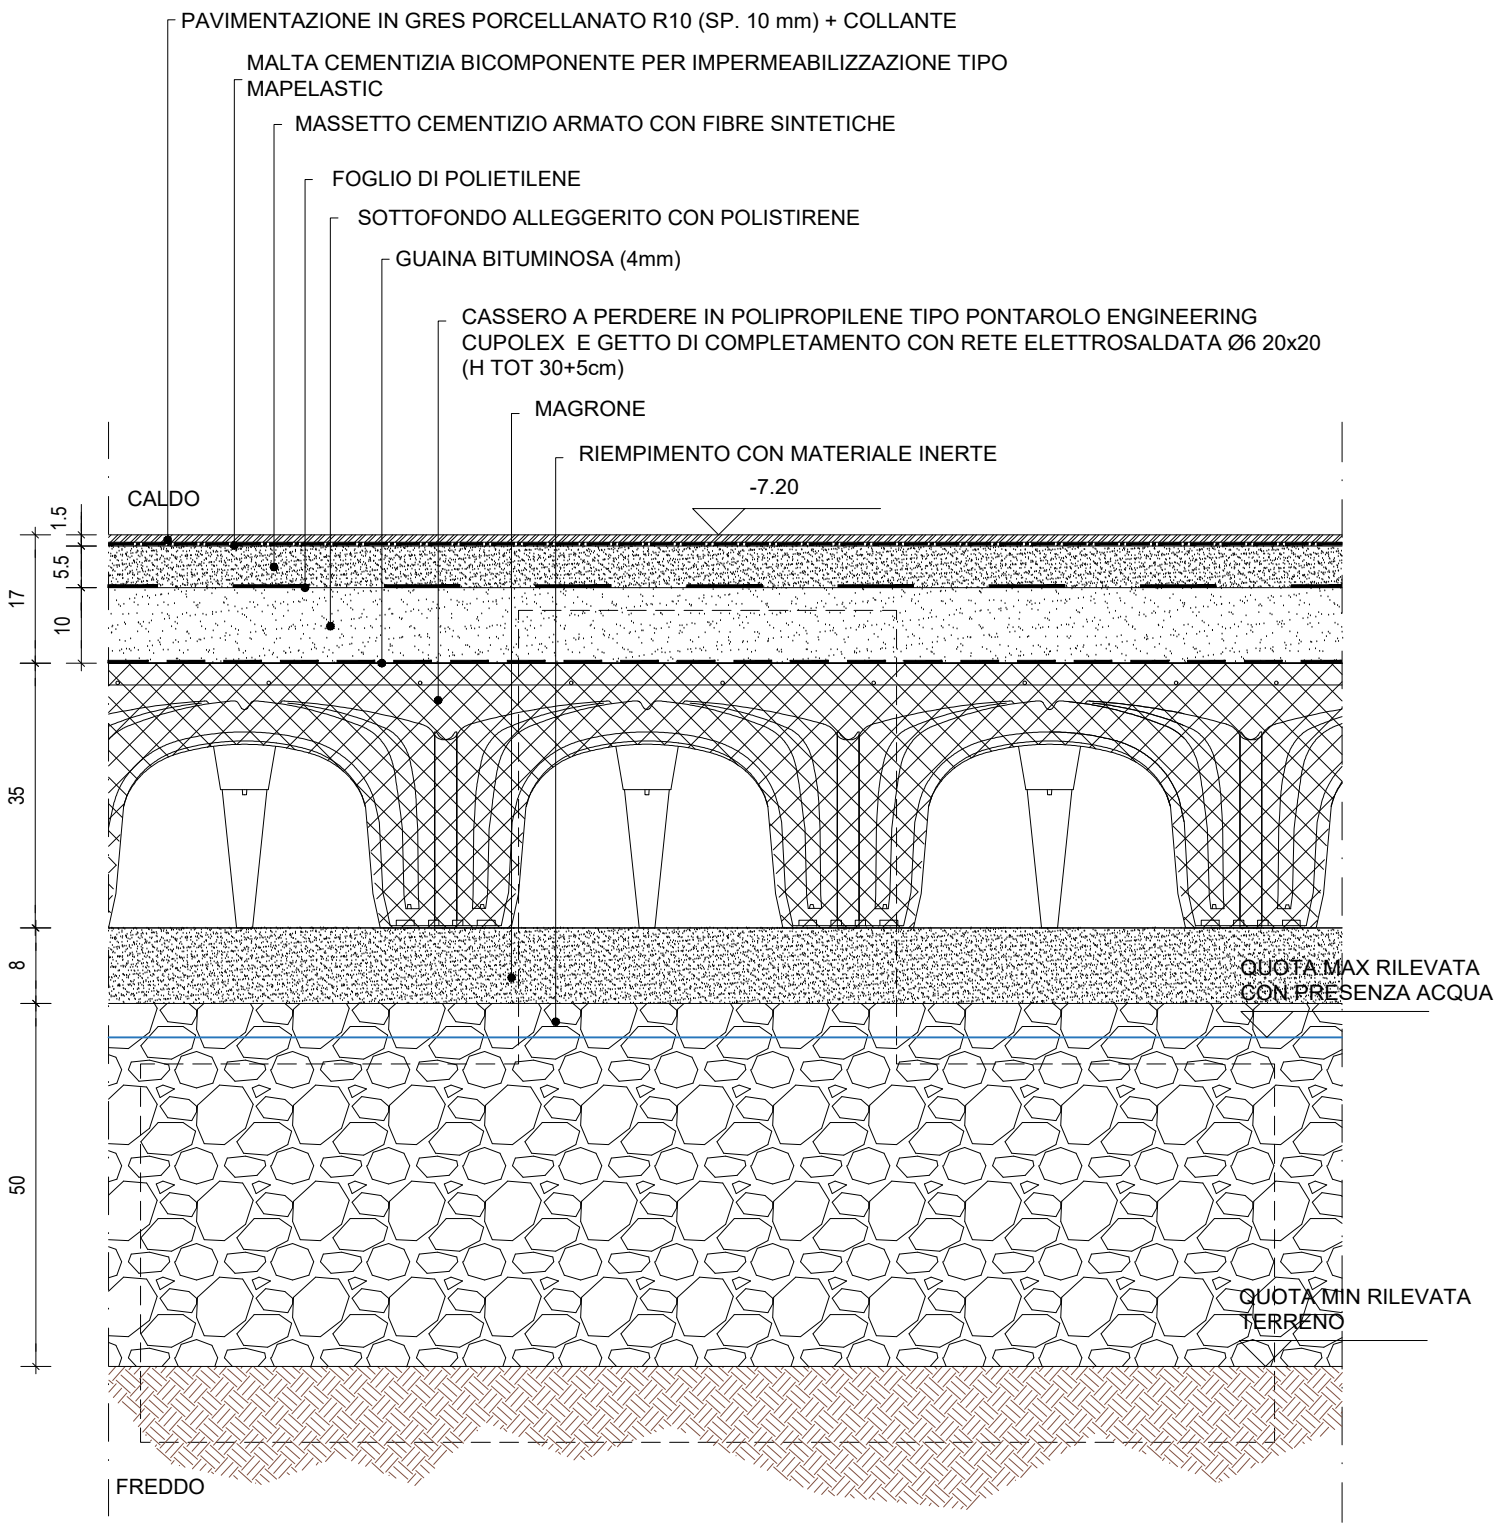


CODICE	COI1+GRE-S
VISTA	SEZIONE VERTICALE 1:10
DESCRIZIONE	PAVIMENTAZIONE CON FINITURA IN GRES PER LOCALI UMIDI
POSIZIONE	PIANO SECONDO INTERRATO
NOTE	-

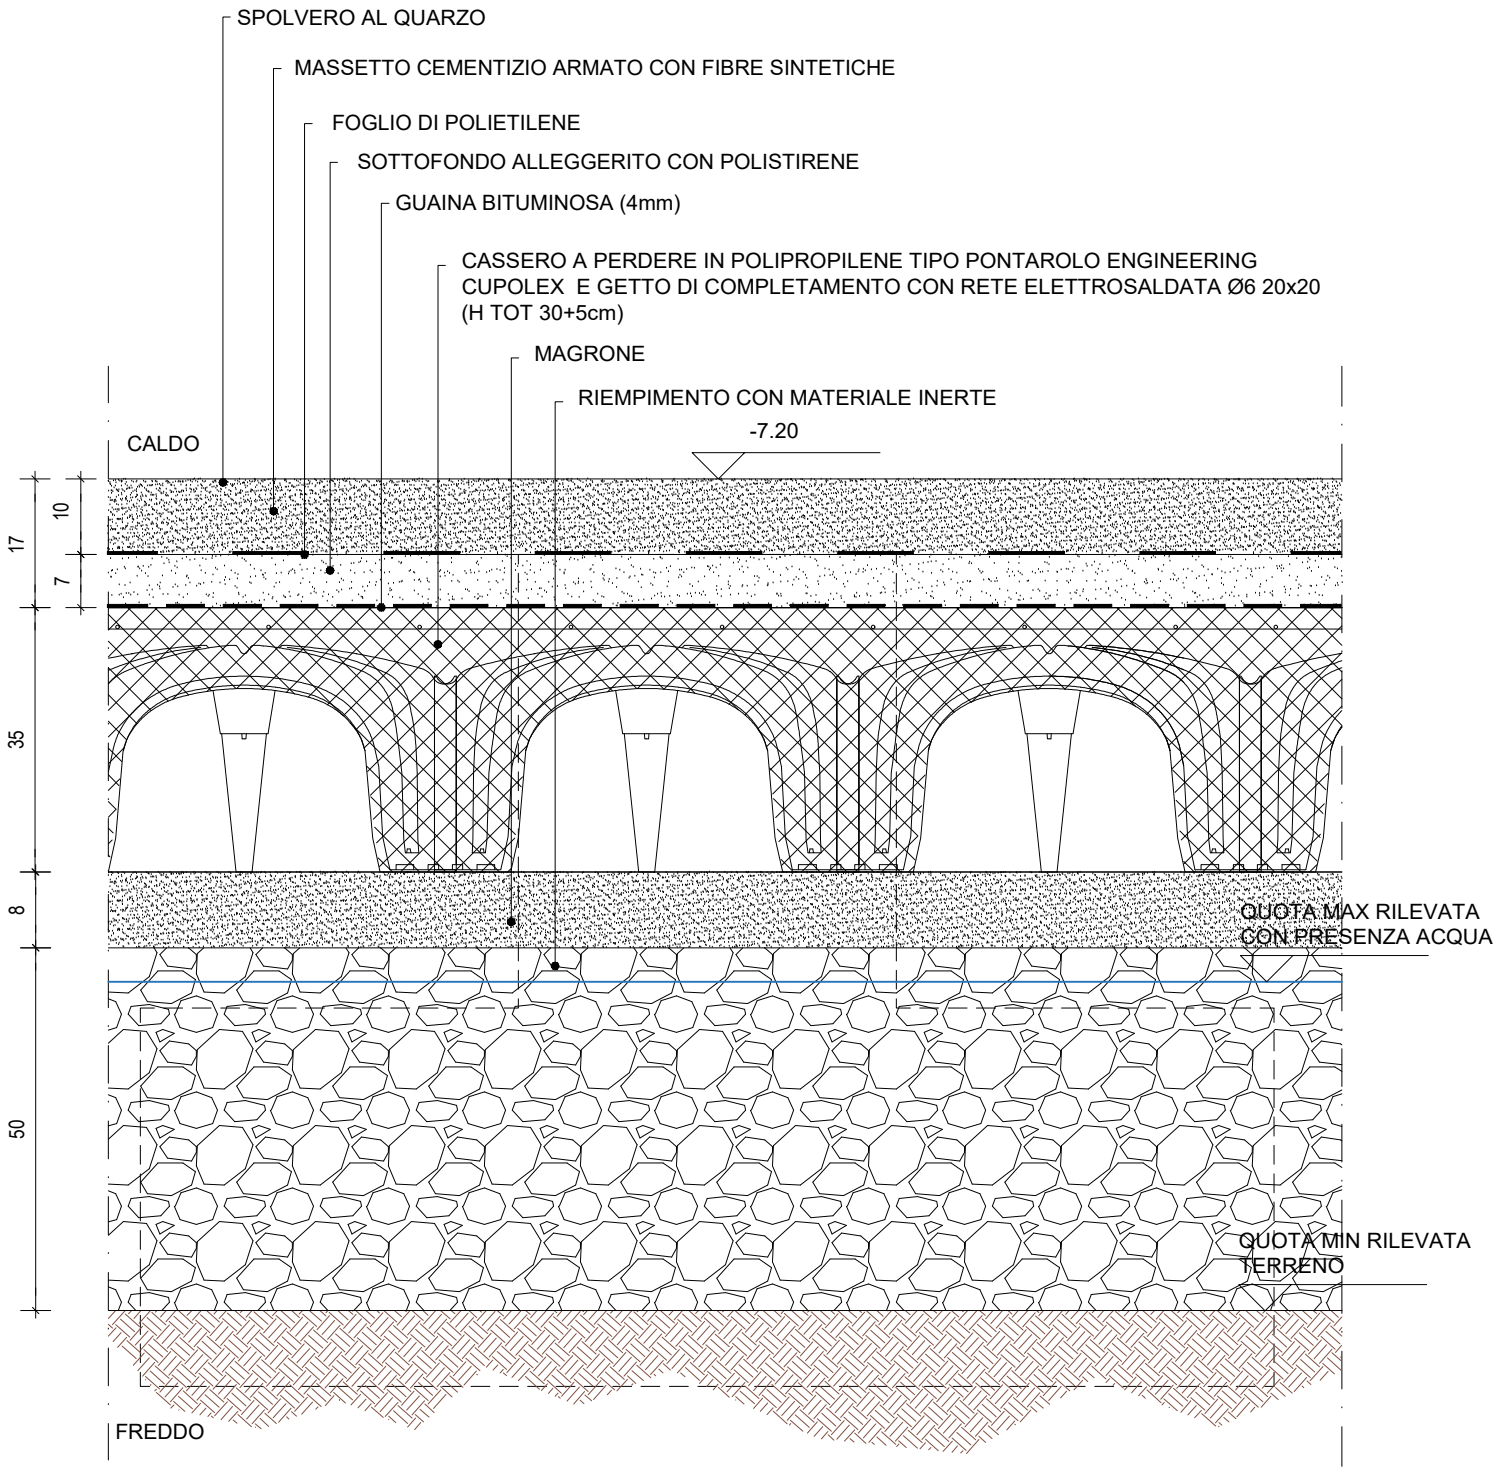

CODICE	COI1+QCS
VISTA	SEZIONE VERTICALE 1:10
DESCRIZIONE	PAVIMENTAZIONE INDUSTRIALE PER LOCALI TECNICI
POSIZIONE	PIANO SECONDO INTERRATO
NOTE	-

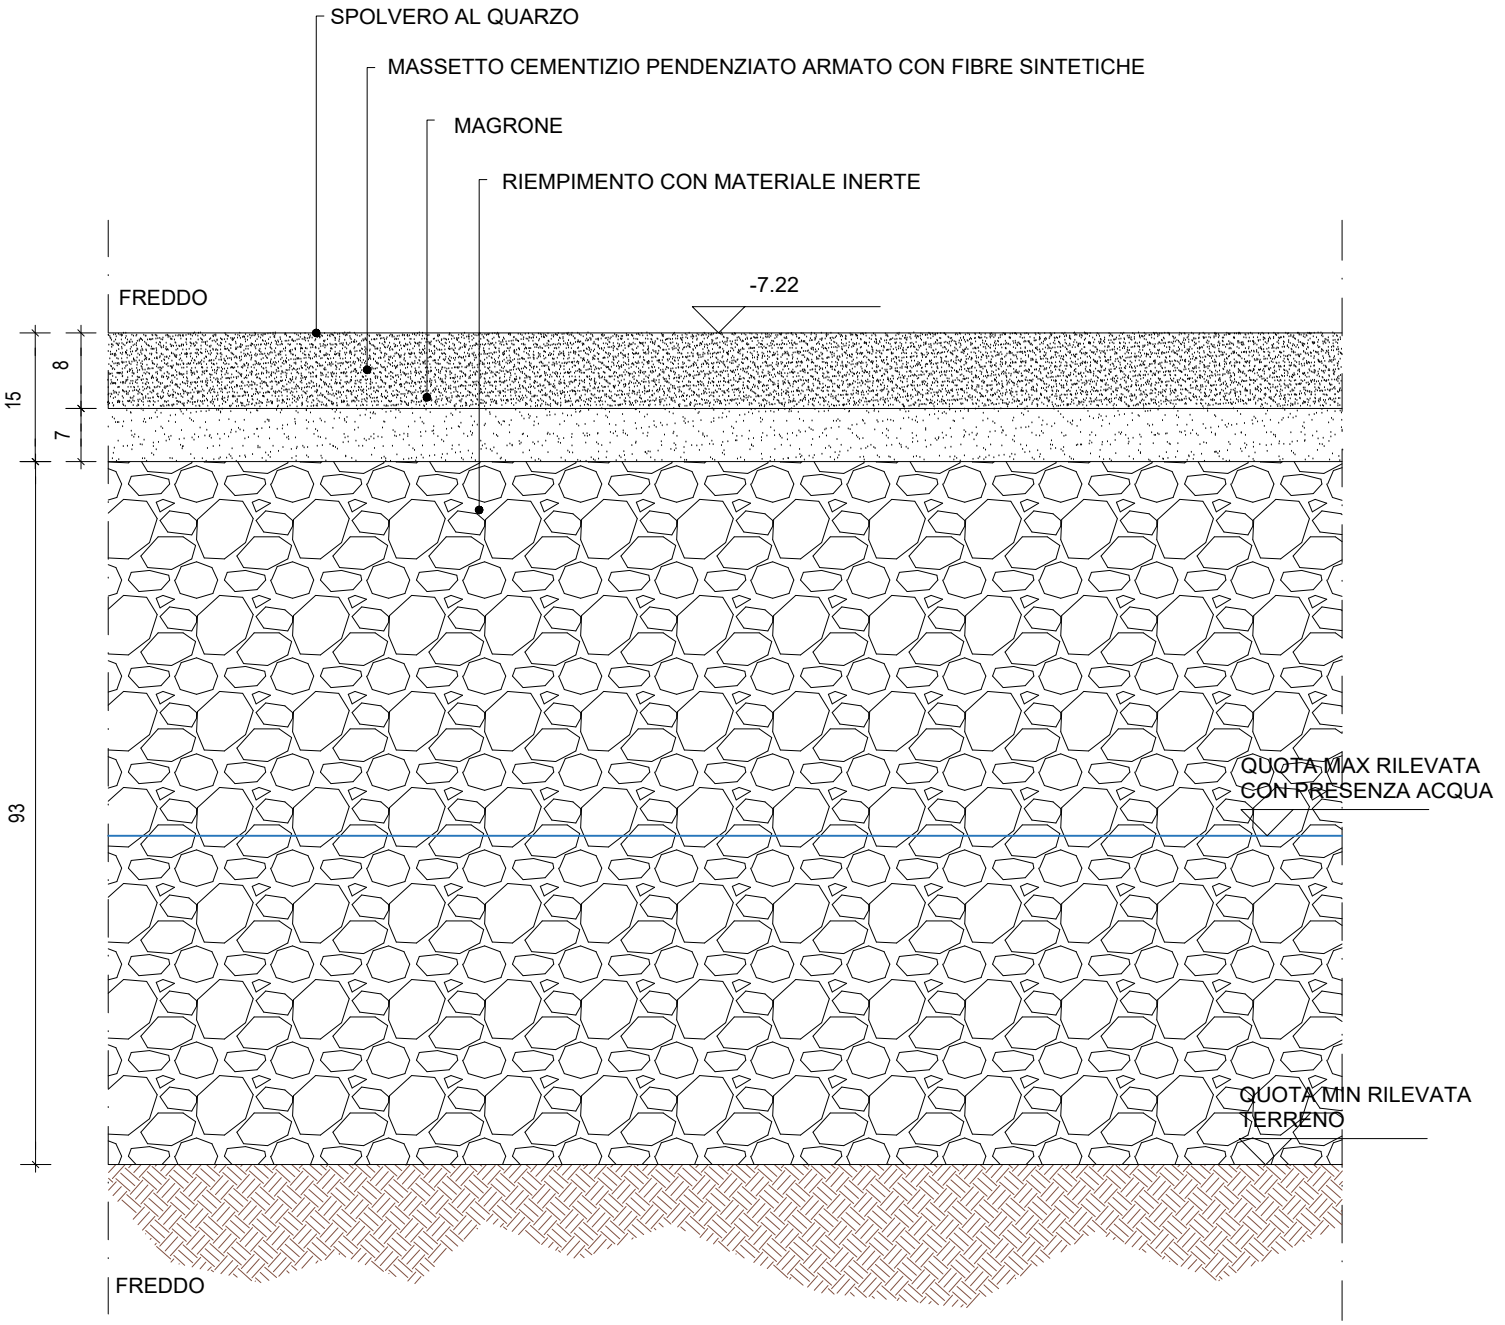


CODICE	COI2-QCS
VISTA	SEZIONE VERTICALE 1:10
DESCRIZIONE	PAVIMENTAZIONE INDUSTRIALE
POSIZIONE	BOCCHE DI LUPO PIANO SECONDO INTERRATO
NOTE	-

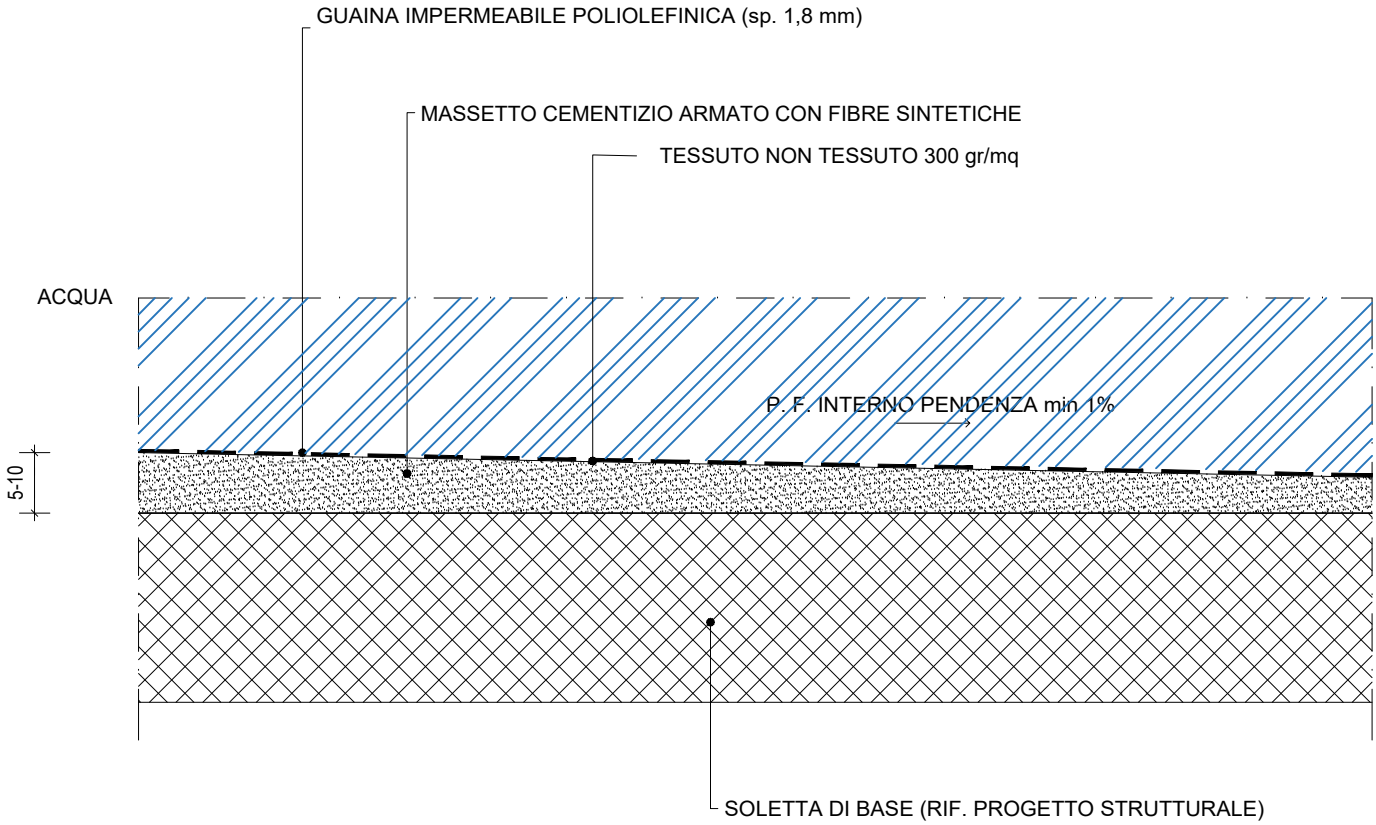


CODICE	COI10+TPO
VISTA	SEZIONE VERTICALE 1:10
DESCRIZIONE	VASCA ANTINCENDIO
POSIZIONE	PIANO SECONDO INTERRATO
NOTE	-

PIO


PARTIZIONI INTERNE ORIZZONTALI
DI PROGETTO

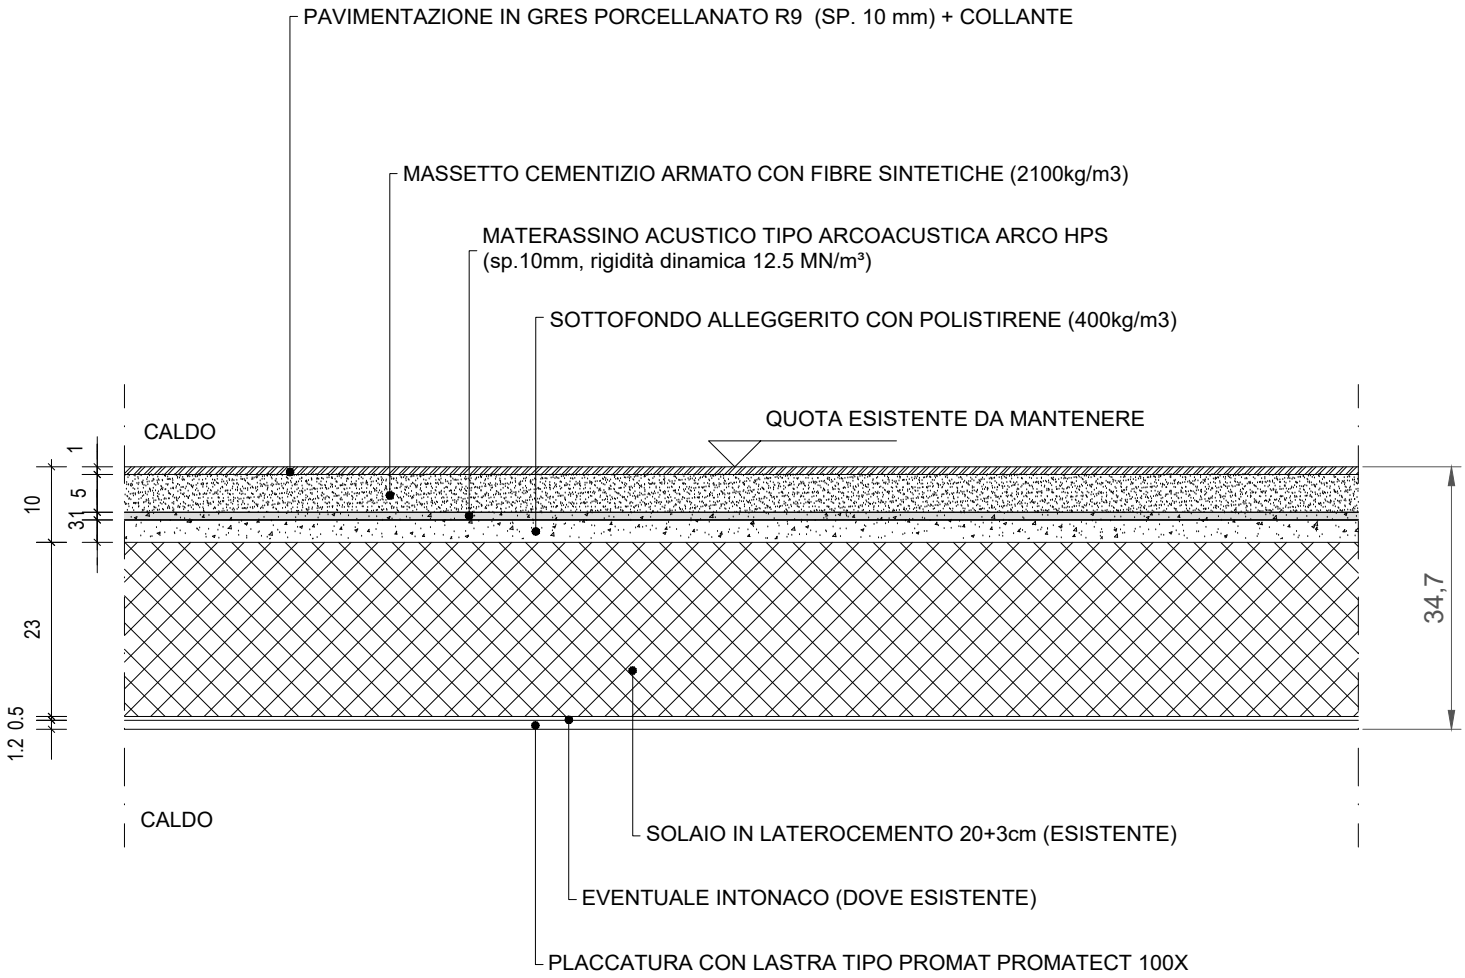

CODICE	PIO1+GRE
VISTA	SEZIONE VERTICALE 1:10
DESCRIZIONE	PAVIMENTAZIONE CON FINITURA IN GRES
POSIZIONE	TUTTI I PIANI
NOTE	LA RIQUALIFICAZIONE PROPOSTA GARANTISCE UNA PRESTAZIONE PARI A REI120, VALORE CHE PUO' ESSERE RIDOTTA NEL RISPETTO DEI VALORI MINIMI INDICATI NELLA PRATICA TENENDO CONTO DELLE DIVERSE DESTINAZIONI D'USO DEI LOCALI SOTTOSTANTI IL SOLAIO

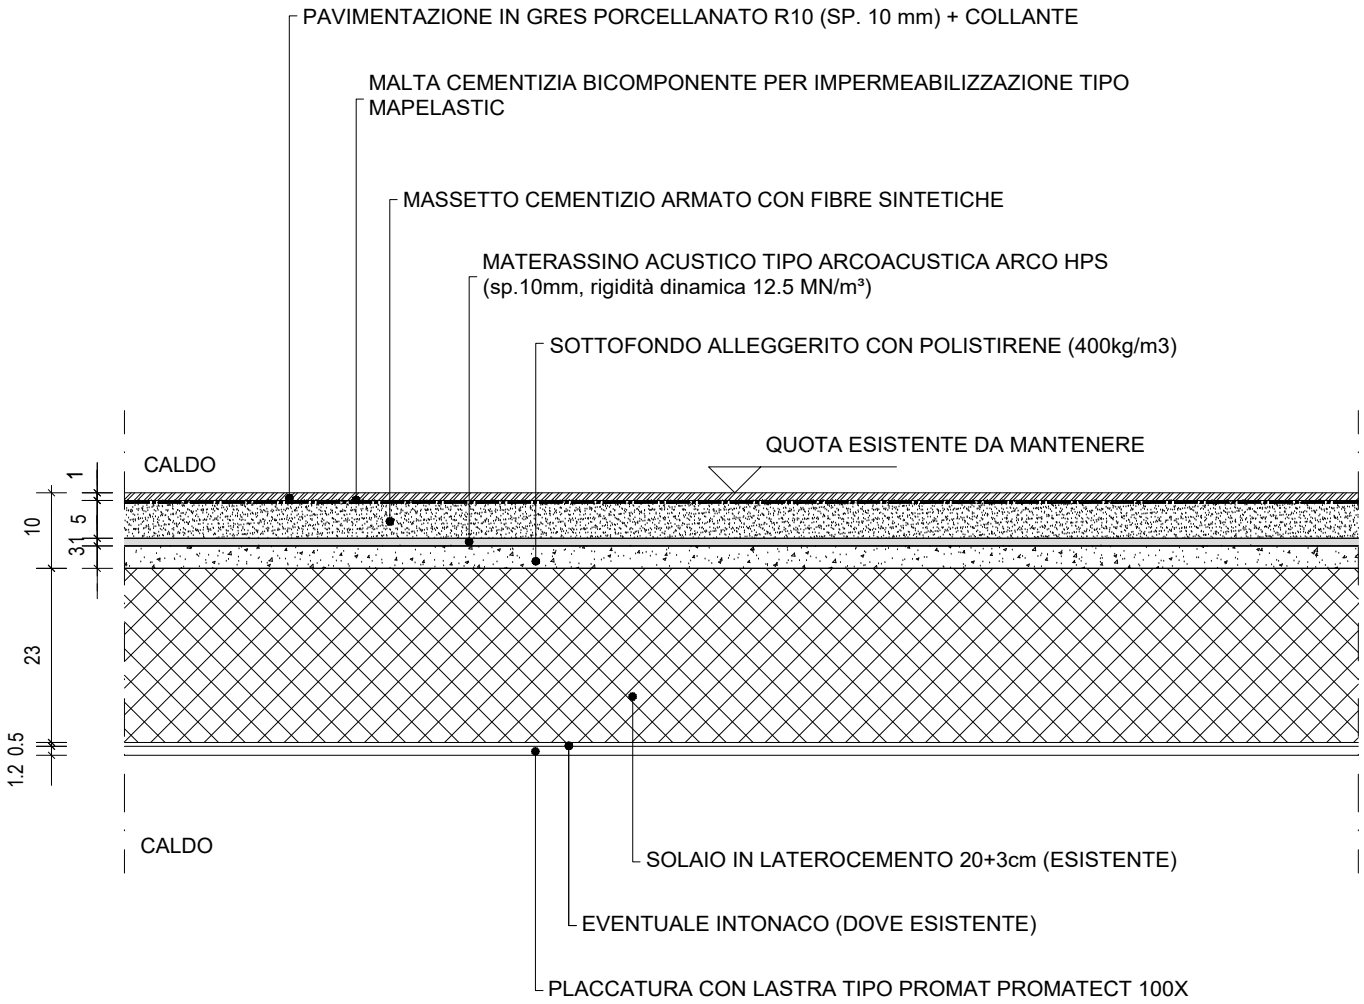


CODICE	PIO2+GRE-S
VISTA	SEZIONE VERTICALE 1:10
DESCRIZIONE	PAVIMENTAZIONE CON FINITURA IN GRES PER LOCALI UMIDI
POSIZIONE	TUTTI I PIANI
NOTE	LA RIQUALIFICAZIONE PROPOSTA GARANTISCE UNA PRESTAZIONE PARI A REI120, VALORE CHE PUO' ESSERE RIDOTTA NEL RISPETTO DEI VALORI MINIMI INDICATI NELLA PRATICA TENENDO CONTO DELLE DIVERSE DESTINAZIONI D'USO DEI LOCALI SOTTOSTANTI IL SOLAIO

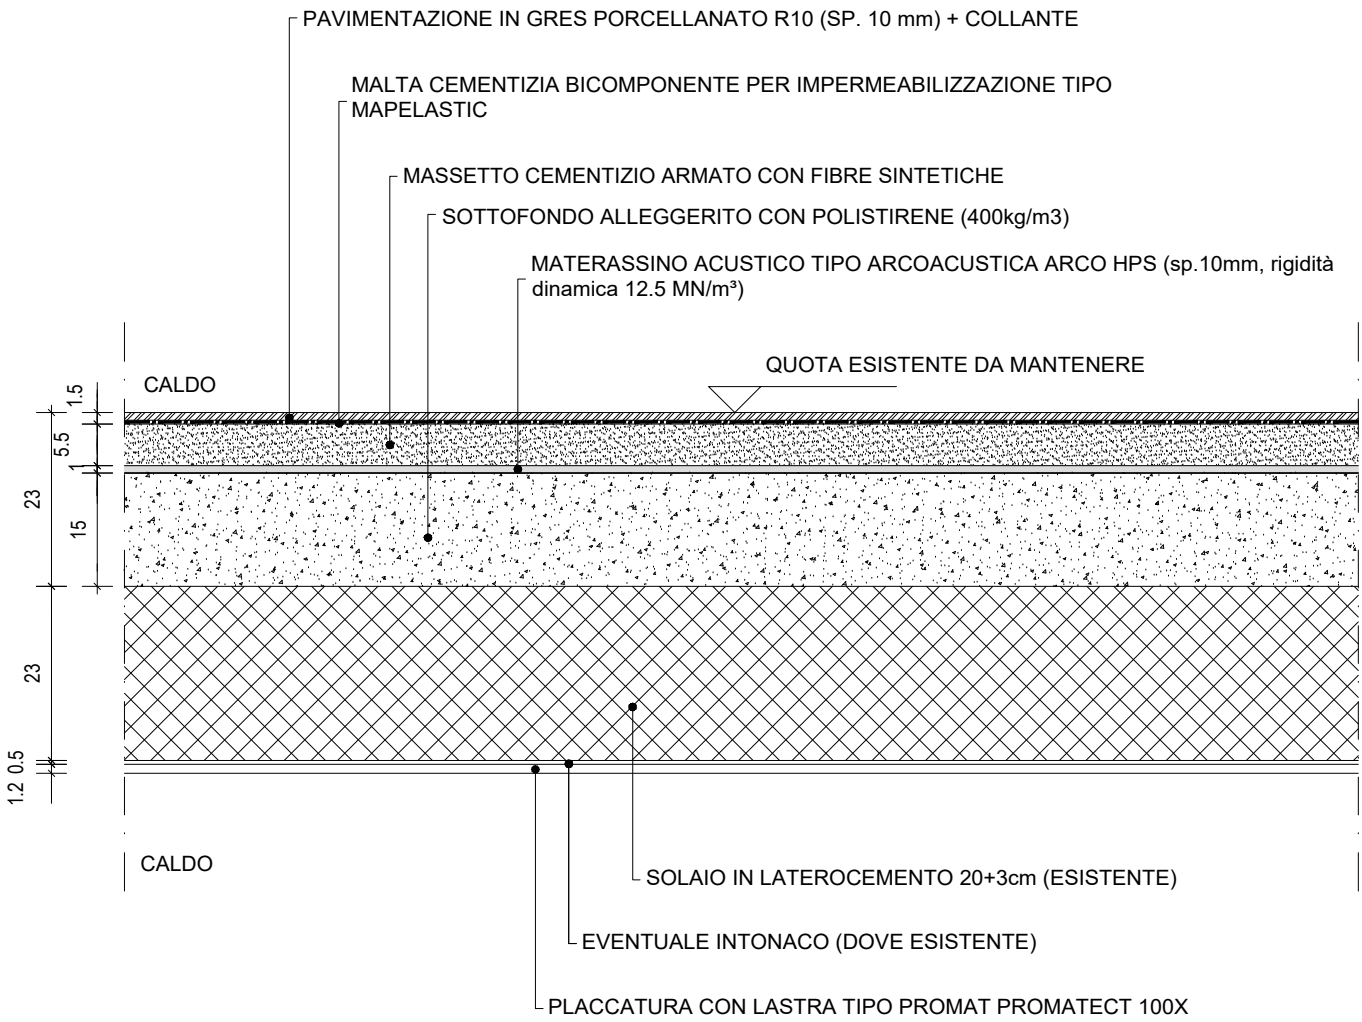


CODICE	PIO21+GRE-S
VISTA	SEZIONE VERTICALE 1:10
DESCRIZIONE	PAVIMENTAZIONE CON FINITURA IN GRES PER LOCALI UMIDI
POSIZIONE	PIANO QUINTO
NOTE	LA RIQUALIFICAZIONE PROPOSTA GARANTISCE UNA PRESTAZIONE PARI A REI120, VALORE CHE PUO' ESSERE RIDOTTA NEL RISPETTO DEI VALORI MINIMI INDICATI NELLA PRATICA TENENDO CONTO DELLE DIVERSE DESTINAZIONI D'USO DEI LOCALI SOTTOSTANTI IL SOLAIO

COS

CHIUSURE ORIZZONTALI SUPERIORI DI PROGETTO

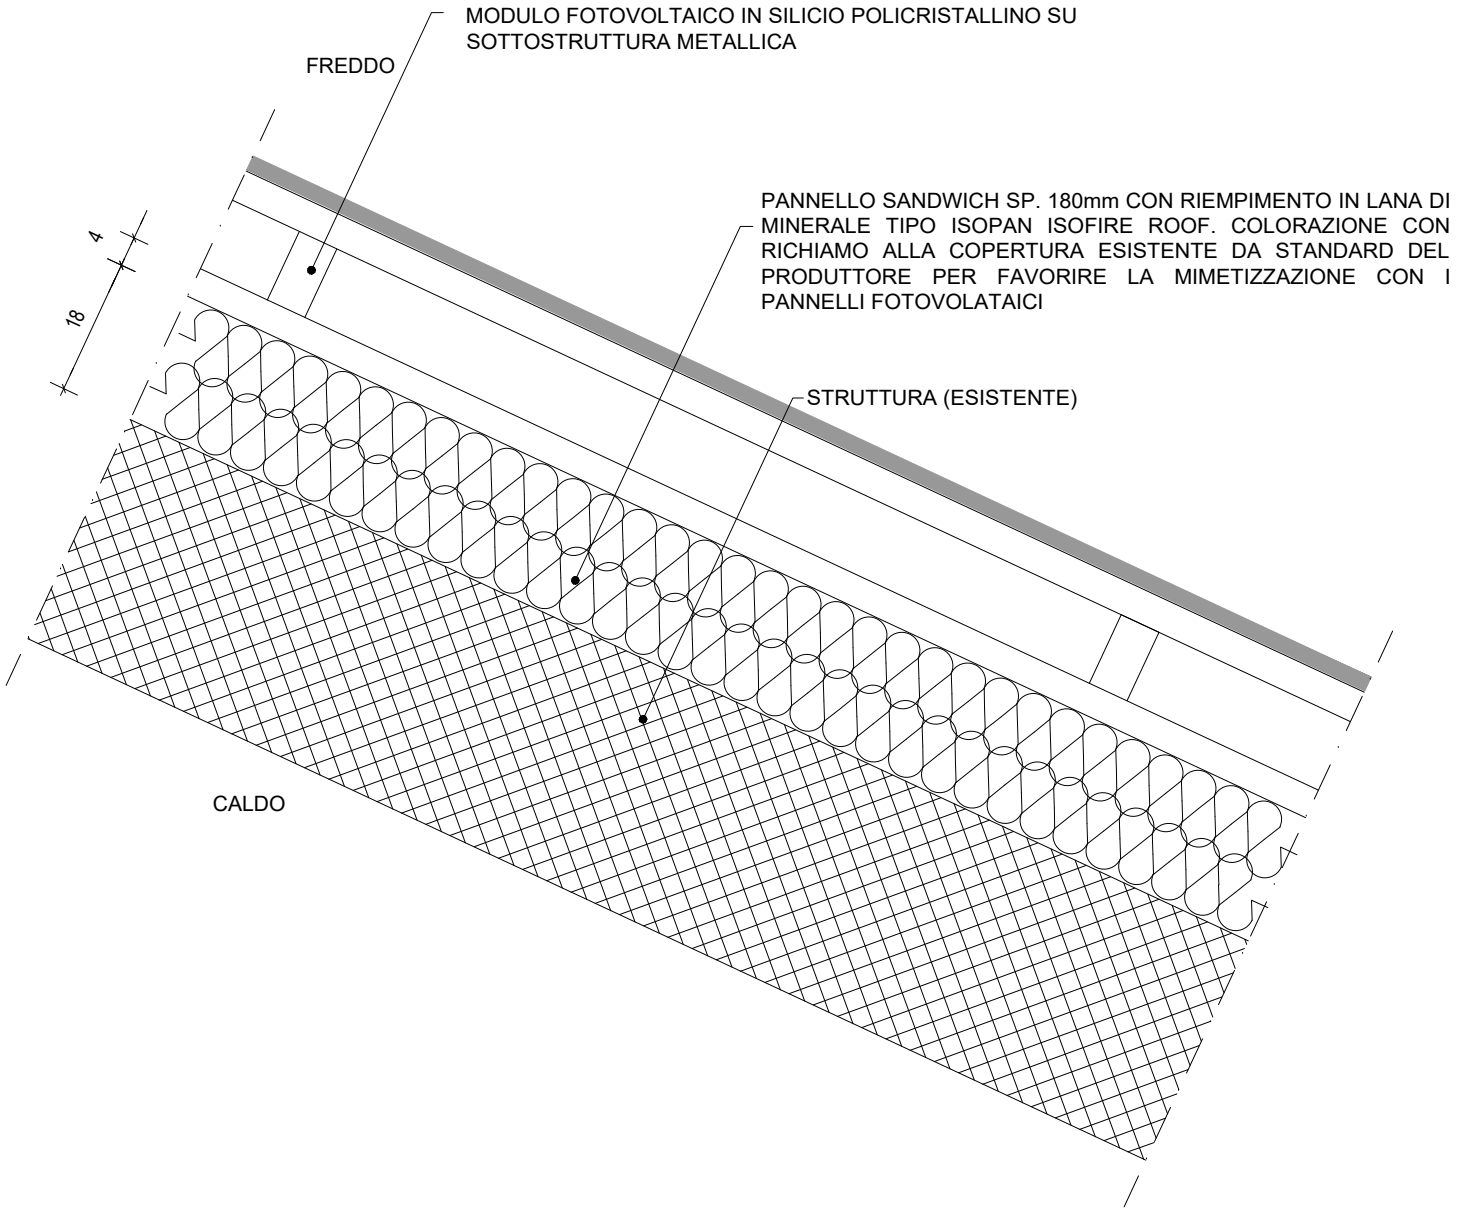


CODICE	COS10
VISTA	SEZIONE VERTICALE 1:10
DESCRIZIONE	COPERTURA CON PANNELLI SANDWICH
POSIZIONE	COPERTURA DEL PIANO QUINTO
NOTE	-

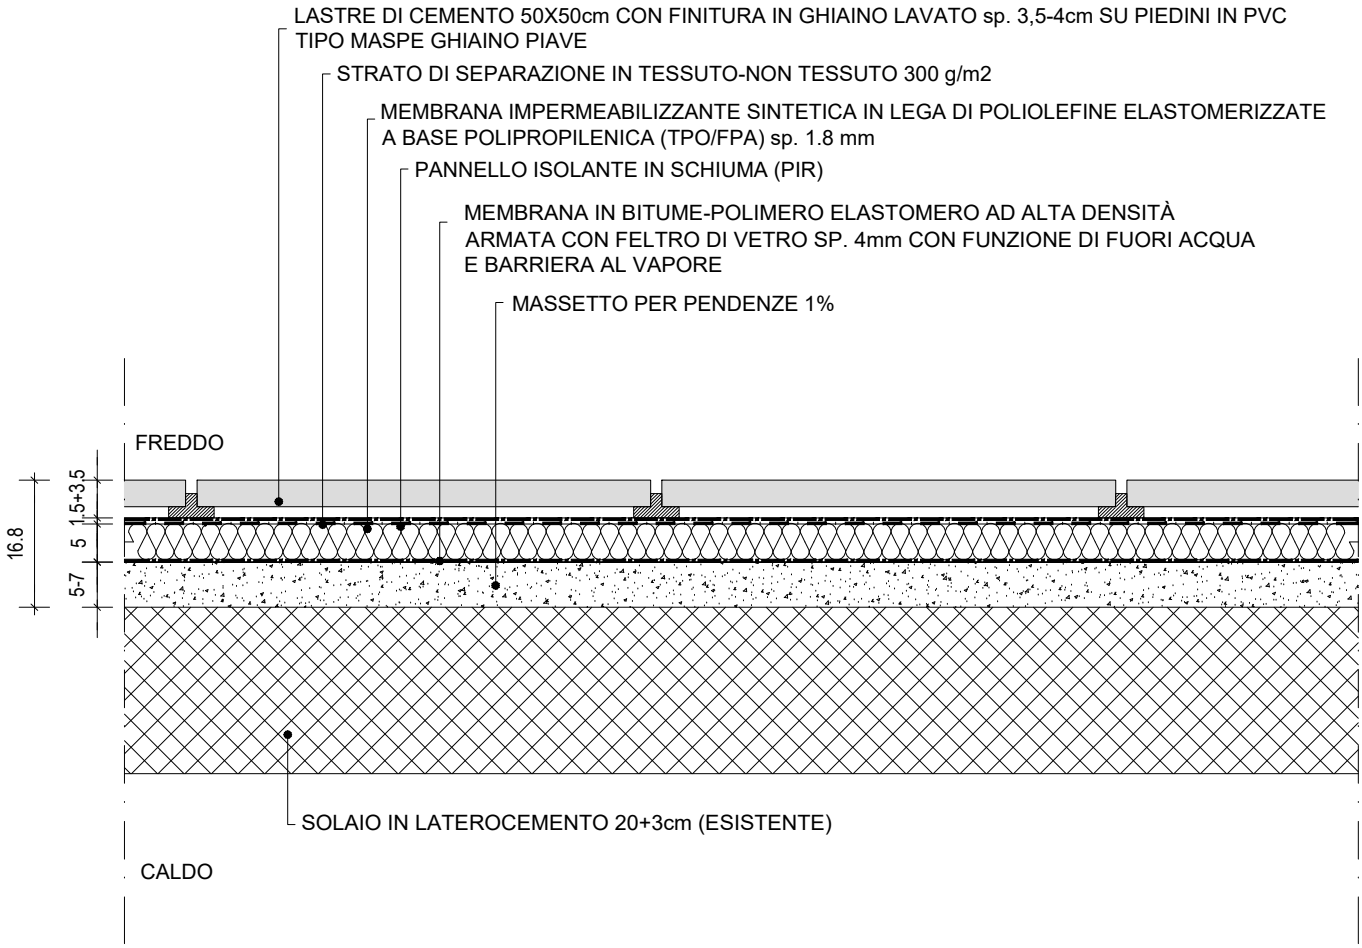


CODICE	COS2+CEM
VISTA	SEZIONE VERTICALE 1:10
DESCRIZIONE	COPERTURA CON QUADROTTI IN CLS
POSIZIONE	PIANO QUINTO - POGGIOLI ESTERNI
NOTE	-


GIUNTI
DI PROGETTO

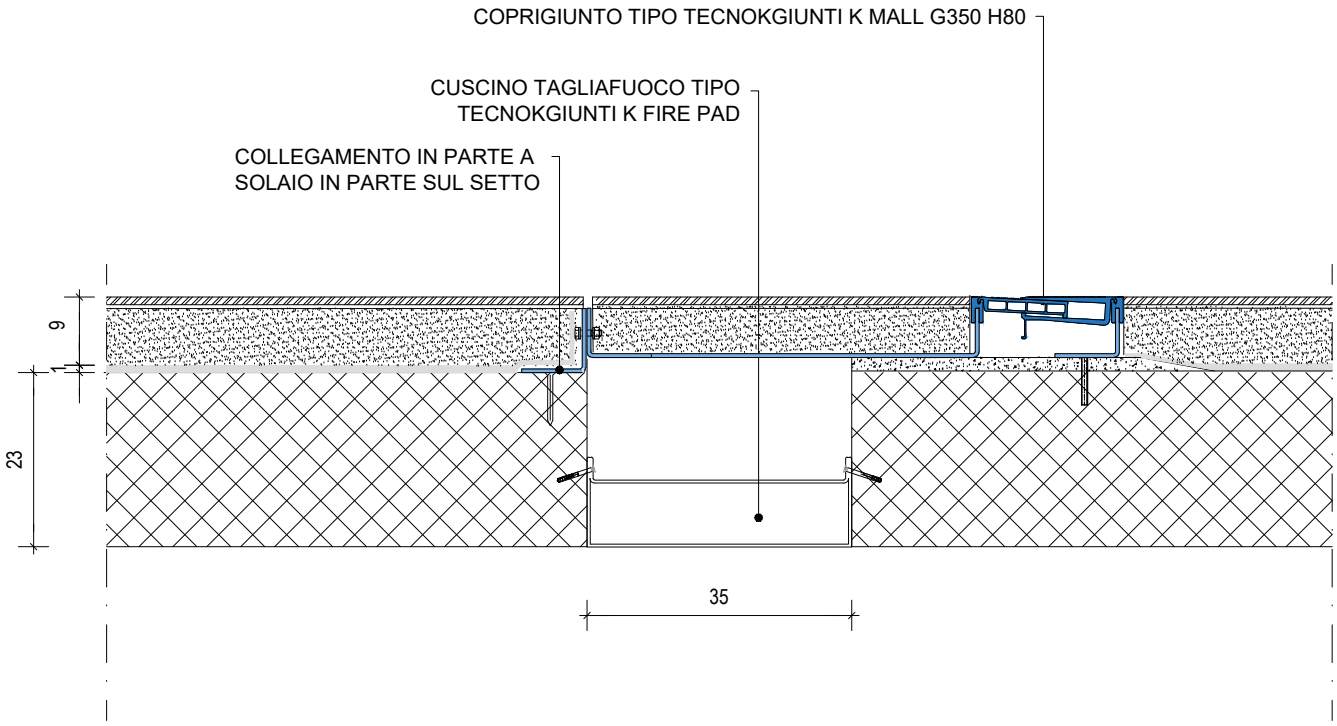

CODICE	GIU-COI-1
VISTA	SEZIONE VERTICALE 1:10
DESCRIZIONE	DETTAGLI DEL GIUNTO A PAVIMENTO
POSIZIONE	PIANO TIPO (CORPO CENTRALE)
NOTE	-

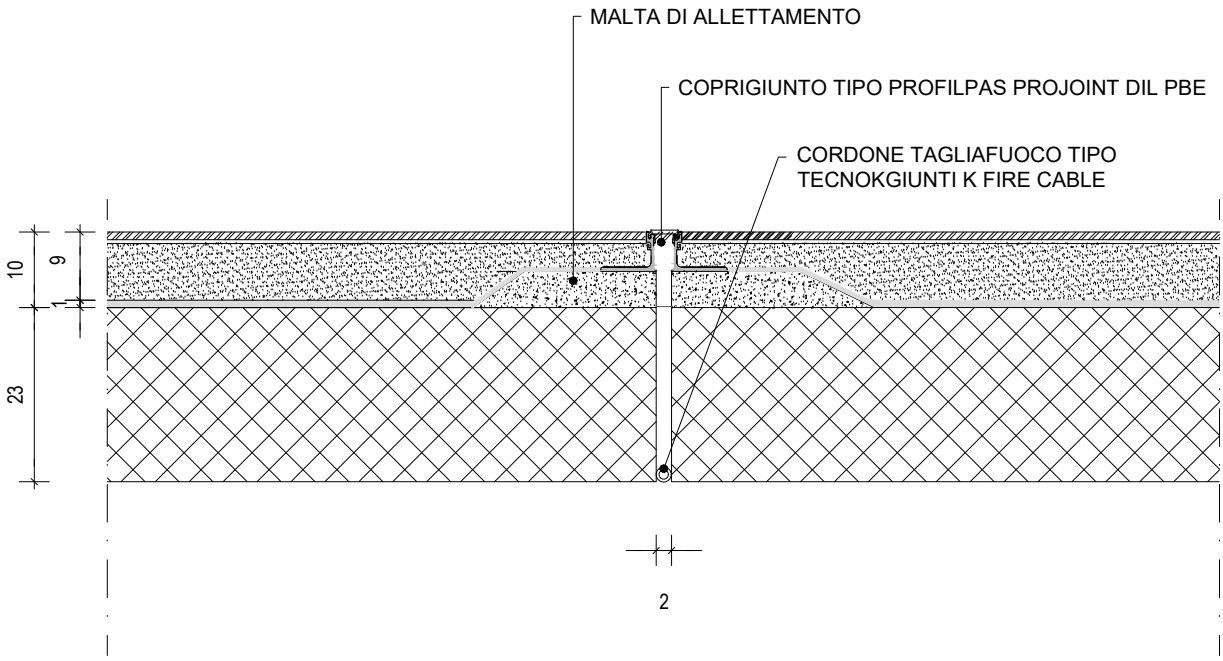

CODICE	GIU-COI-2
VISTA	SEZIONE VERTICALE 1:10
DESCRIZIONE	DETTAGLI DEL GIUNTO A PAVIMENTO (sp. 2 cm)
POSIZIONE	PIANO TIPO (ALI NORD E SUD)
NOTE	-

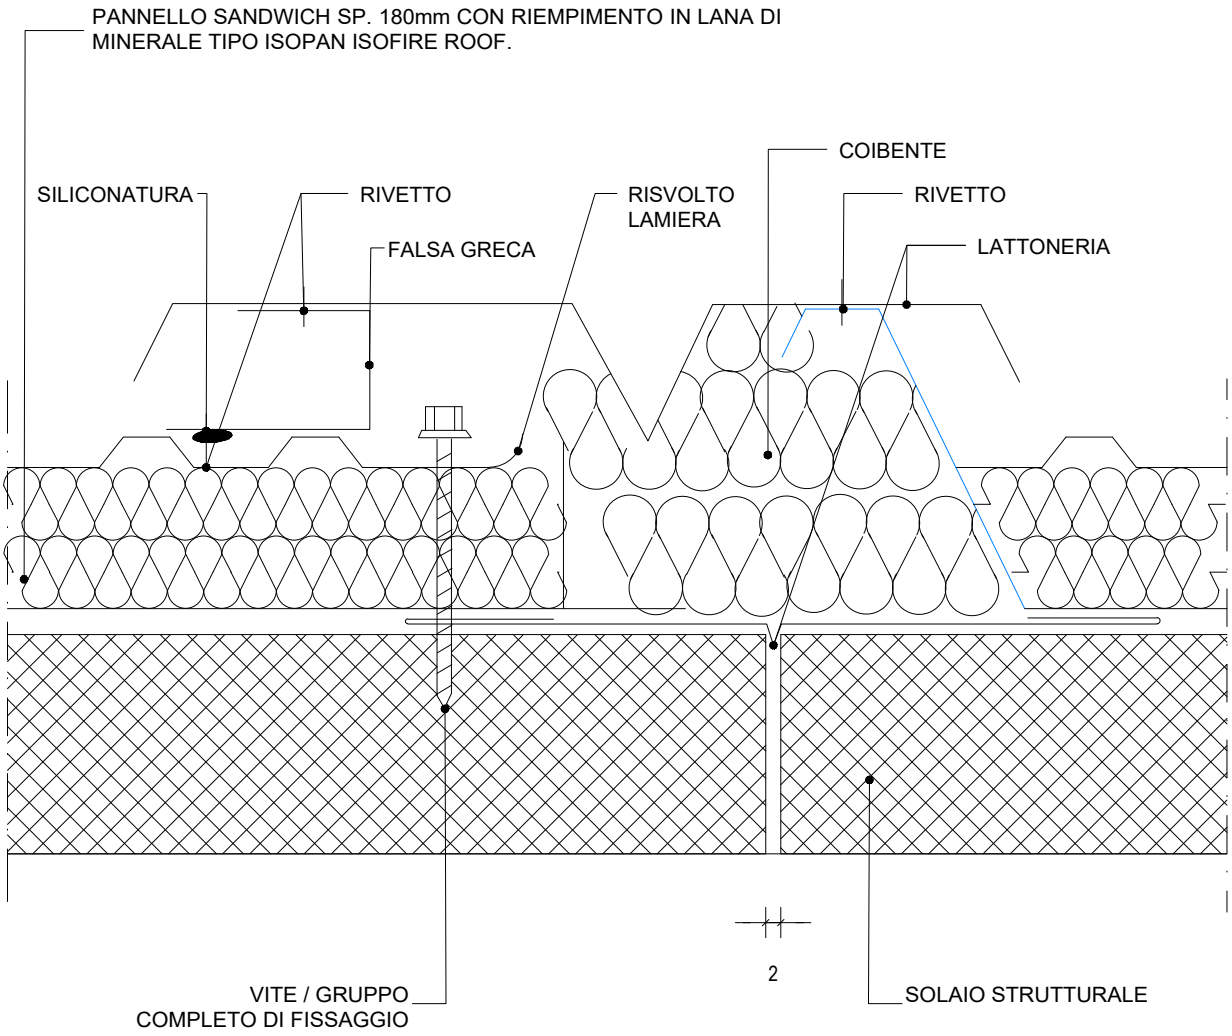

CODICE	GIU-COS-1
VISTA	SEZIONE VERTICALE 1:10
DESCRIZIONE	DETTAGLI DEL GIUNTO IN COPERTURA (sp. 2 cm)
POSIZIONE	COPERTURA
NOTE	-