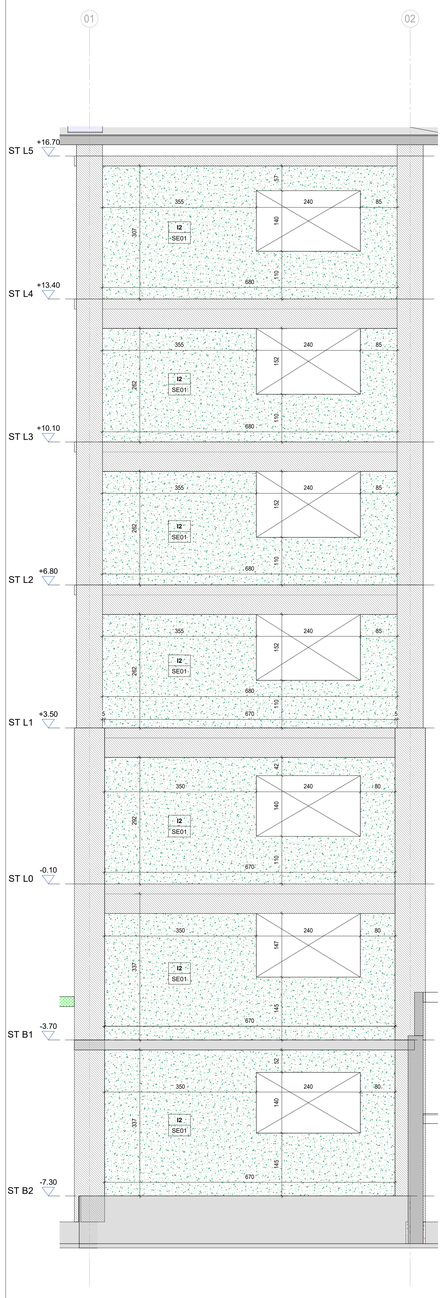
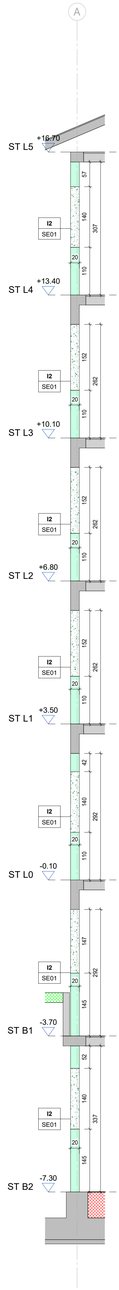
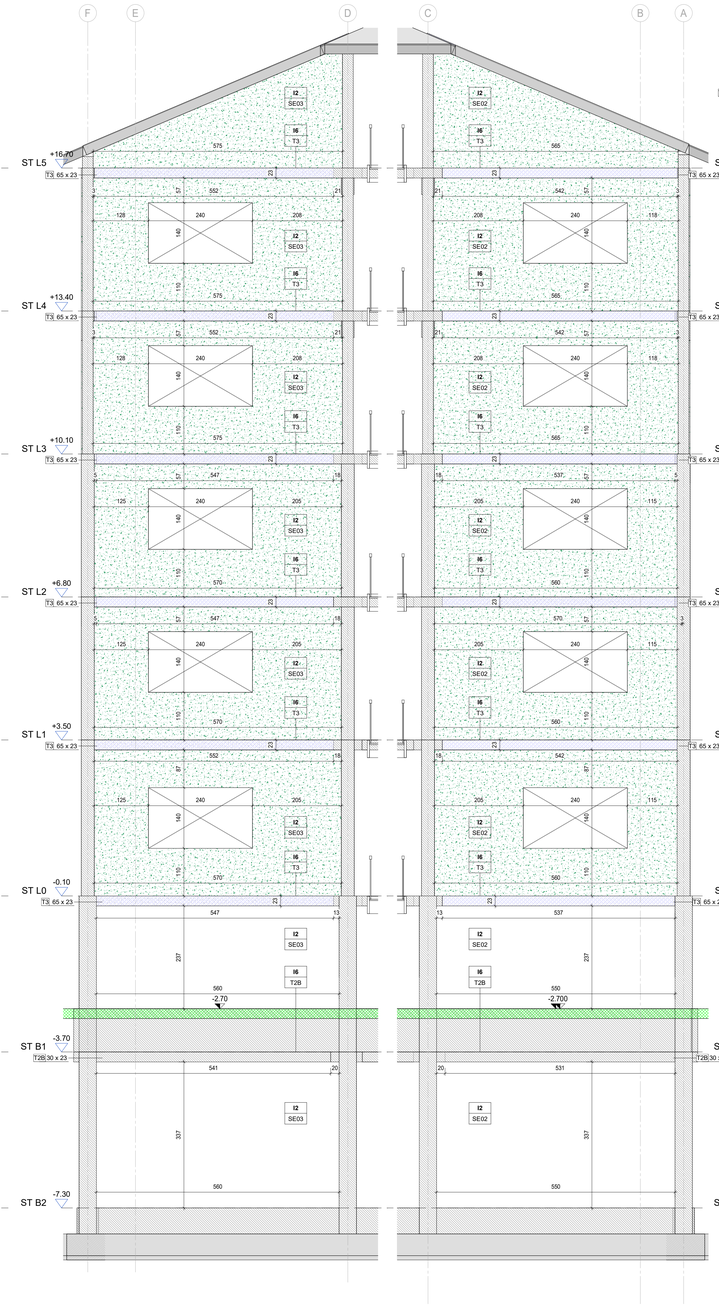
## SE01
Scala 1 : 50





## SE01-1
Scala 1 : 50



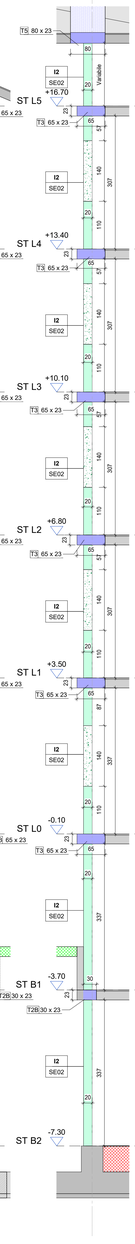

## SE02-SE03
Scala 1 : 50





## SE02-1
Scala 1 : 50





## SE03-1
Scala 1 : 50

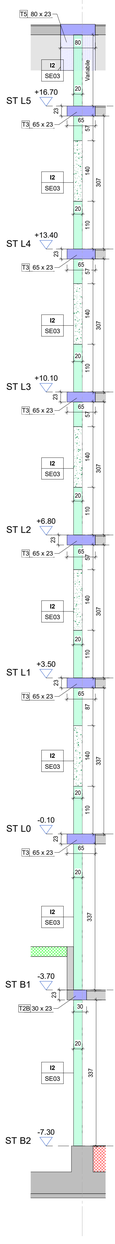



## SE04
Scala 1 : 50

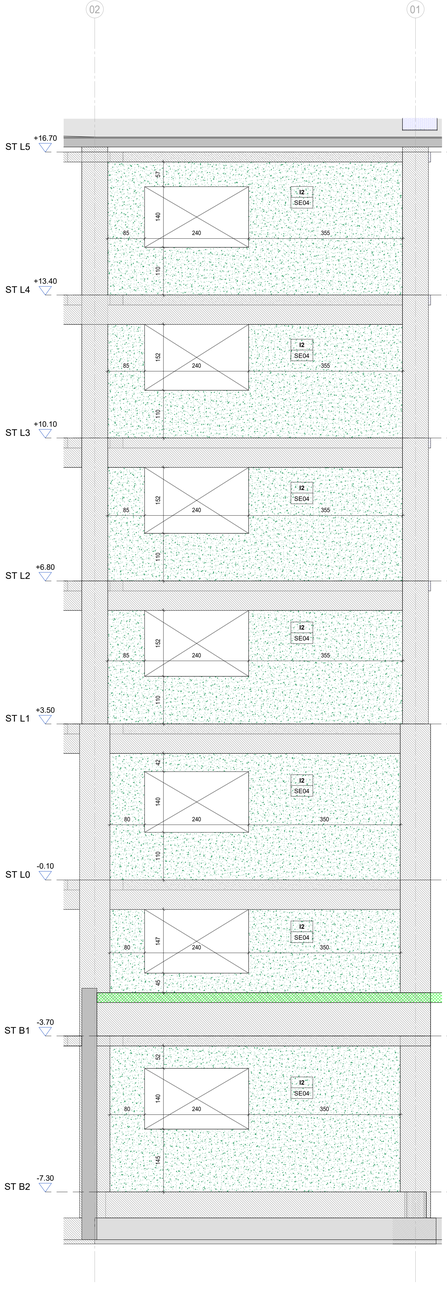



## SE04-1
Scala 1 : 50

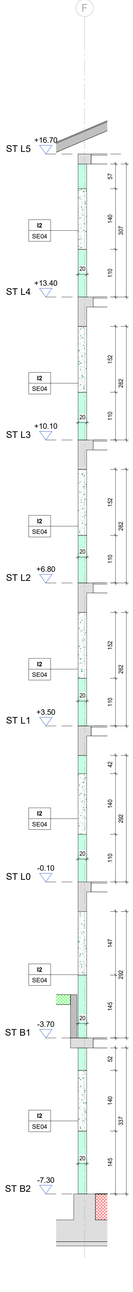


## Key-Plan Setti
Scala 1 : 600

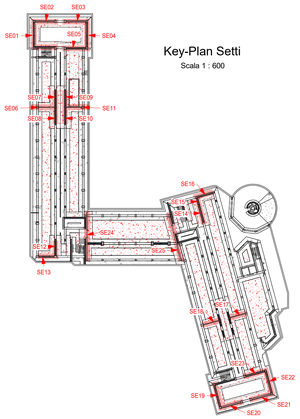


### NODI BULLONATI

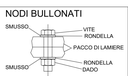


### ACCIAIO PER CARPENTERIA METALLICA

- Carpenteria metallica: S275JR zincato
- Zincatura a caldo
- Zincatura a freddo nelle zone di saldatura in opera
- Inghisaggi chimici:
  Connessioni certificate C2 con resina TIPO HILTI HIT RE500 V4 e barre filettate classe 8.8

### CLASSE DI ESECUZIONE SECONDO UNIEN1090

| | |
|---|---|
| Classe di conseguenza | CC3 |
| Categoria di servizio | SC1 |
| Categoria di produzione | PC2 |
| Classe di esecuzione | EXC3 |

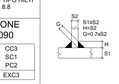
### INGHISAGGI CHIMICI




### BULLONI
classe 8.8

| | | | | | |
|---|---|---|---|---|---|
| Ø BULL | 12 | 14 | 16 | 20 | 24 |
| Ø FORO | 13.0 | 15.0 | 17.0 | 21.0 | 25.5 |
| COPPIE SERR.(N•m) | conforme vigente normativa | | | | |
| SIMBOLO | ◆ | □ | ➔ | ✣ | ✤ |

### SALDATURA A CORDONE D'ANGOLO
(OVE NON ALTRIMENTI INDICATO)





### SALDATURA DI PRIMA CLASSE PER GIUNTO a "T" A COMPLETA PENETRAZIONE
(PER TUTTE LE FLANGE OVE NON ALTRIMENTI INDICATO)




*- LE STRUTTURE METALLICHE DOVRANNO AVERE LE CONTROFRECCE DI MONTAGGIO OVE PREVISTO*
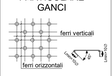
### PARTICOLARE GANCI




min 9/28/mq su tutti i muri

### PARTICOLARE RIPRESA DI GETTO VERTICALE




### PARTICOLARE SOVRAPPOSIZIONI




Sovrapposizione di reti elettrosaldate minimo due maglie

### PARTICOLARE CHIUSURA DELLE GABBIE

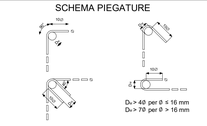



### SPECIFICA COPRIFERRO/QUOTATURA




Le quote sono riferite al filo esterno

### SCHEMA PIEGATURE




$D_m$ > 40 per ∅ ≤ 16 mm
$D_m$ > 70 per ∅ > 16 mm




Piegare alle estremità tutte le armature correnti:
- h = H - 10 per fondazioni
- h = H - 5 per travi/solette/solai
(salvo indicazione maggiore di copriferro)

### CALCESTRUZZO

| Calcestruzzo per | Magrone | Fondazione | Orizzontale | Strutture in elevazione |
|---|---|---|---|---|
| Classe di resistenza (Fck/Rck) | C12/15 | C28/35 | C35/45 | C35/45 |
| Classe esposizione ambientale | - | XC2 | XC2 | XC2 |
| Cemento tipo | 42.5N | 42.5N | 42.5N | 42.5N |
| Rapporto max acqua/cemento | CONFORME ALLA NORMATIVA VIGENTE | | | |
| Contenuto min. cemento (kg/m³) | | | | |
| Ø max inerti (mm) | - | 16 | 16 | 16 |
| Classe di consistenza | - | S4 | S5 | SCC |
| Copriferro netto (mm) | - | 40 | 30 | 30 |
| Copriferro netto controterra | ≥ 40 mm | | | |
| Profondità permeazione acqua secondo ISO7031 | < 20 mm | | | |

### ACCIAIO PER CEMENTO ARMATO

ACCIAIO TIPO B450C controllato in stabilimento e saldabile

### PRESCRIZIONI NOTE GENERALI

*- VERIFICARE TUTTE LE MISURE IN CANTIERE PRIMA DI EFFETTUARE L'ORDINATIVO DEI MATERIALI*
*- VERIFICARE TUTTE LE MISURE E I FORI CON IL PROGETTO ARCHITETTONICO E IMPIANTISTICO*
*- OVE PREVISTI FIORETTI INGHISATI CON RESINA E TASSELLI CHIMICI DOVRANNO ESSERE POSTI IN OPERA SECONDO LE PRESCRIZIONI DEL PRODUTTORE DELLE RESINE NELLE CONDIZIONI AMBIENTALI IDONEE E PREVIA PERFETTA PULIZIA DEL FORO*
-UN SEGUITO ALLO STRIP-OUT VERIFICARE GEOMETRIA E DIMENSIONI DELLE STRUTTURE INTERESSATE DAGLI INTERVENTI IN CANTIERE
-VERIFICA PREVENTIVAMENTE LA STABILITA' DELLE STRUTTURE ESISTENTI E LE FASI OPERATIVE PRIMA DI DEMOLIRE
-PER LE DEMOLIZIONI DEI SOLAI PROCEDERE PER AREE LIMITATE VERIFICANDONE LA STABILITA' PRIMA DI PROCEDERE IN ALTRE ZONE
-PER LE DEMOLIZIONI PREVEDERE OPPORTUNE OPERE PROVVISIONALI E PUNTELLAZIONE

**CUP F18H22000220005 - CIG 9210532374**



UNIVERSITA' DEGLI STUDI DI BERGAMO

EX CASERMA GUARDIA DI FINANZA

**Progetto di investimento relativo all'intervento di ristrutturazione e rifunzionalizzazione del complesso immobiliare di Via dello Statuto, n. 21 - Bergamo - Corpo C) - "Residenze"**

**PROGETTO ESECUTIVO**

**COMMITTENZA**
Università degli studi di Bergamo
Area Infrastrutture - Settore Infrastrutture
via Salvecchio 19, 24129 Bergamo

**RESPONSABILE UNICO DEL PROCEDIMENTO**
Ing. Marta Sabbatini

**RTP DI PROGETTAZIONE**

CAPOGRUPPO MANDATARIA

**Studio Alberi S.p.A.**
Coordinamento progettuale ed integrazione specialistiche, progettazione edile-architettonica e direzione lavori strutturali in fase di progettazione

Responsabile integrazione tra le prestazioni specialistiche & PM
**Ing. Alessandro Artuso**

Project Coordinator & CDE Manager (Gli/varie professionista)
**Ing. Filippo Bee**

BIM Manager
**Geom. Marika Riccobene**

Progettazione architettonica
**Arch. Andrea Chiarvilini**
**Arch. Laura Von Dellemann**

Esperto in sistemi edilizi
**Ing. Andrea Sbalchiero**

Progettazione ambientale
**Ing. Laura Dalla Valle**

Coordinatore della Sicurezza in fase di Progettazione
**Geom. Moreno Gazzetto**

MANDANTI

**ICONIA Ingegneria Civile S.r.l.**
Progettazione strutturale
**Ing. Ronj Frisa**
**Ing. Domenico D'Arca**

**Energo S.r.l.**
Responsabile progettazione impianti meccanici, elettrici, idrici sanitari
Certificazione energetica
Professionista antincendio
**Arch. Denis Zulin**

**Dott. Geol. Paolo Corsale** Geologo

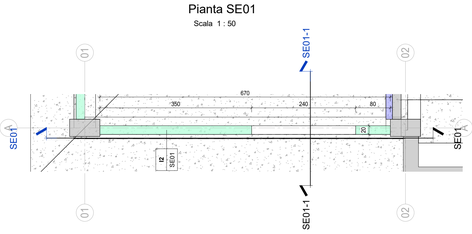
**TITOLO DEL DOCUMENTO:** STRUTTURE
NUOVI SETTI-DETTAGLI CARPENTERIA 1 DI 6

SCALA: VAR


**CODICE:** C1088 | E | ST | DET | 00 | 100 | r00
Commessa | Fase | Disciplina | Set | Livello | Numero | Revisione

| Revisione | Data | Motivo | Redatto | Controllato | Approvato |
|---|---|---|---|---|---|
| 00 | 19/10/2026 | Prima emissione | RM | MG | DD |
| | | | | | |
| | | | | | |
| | | | | | |
| | | | | | |
| | | | | | |

## Pianta SE01
Scala 1 : 50




## Pianta SE02-SE03
Scala 1 : 50

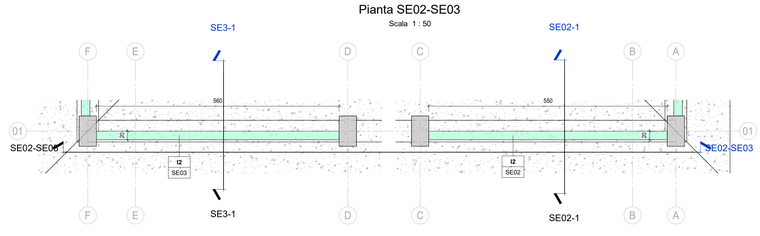


## Pianta SE04
Scala 1 : 50

