SE05
Scala 1 : 50

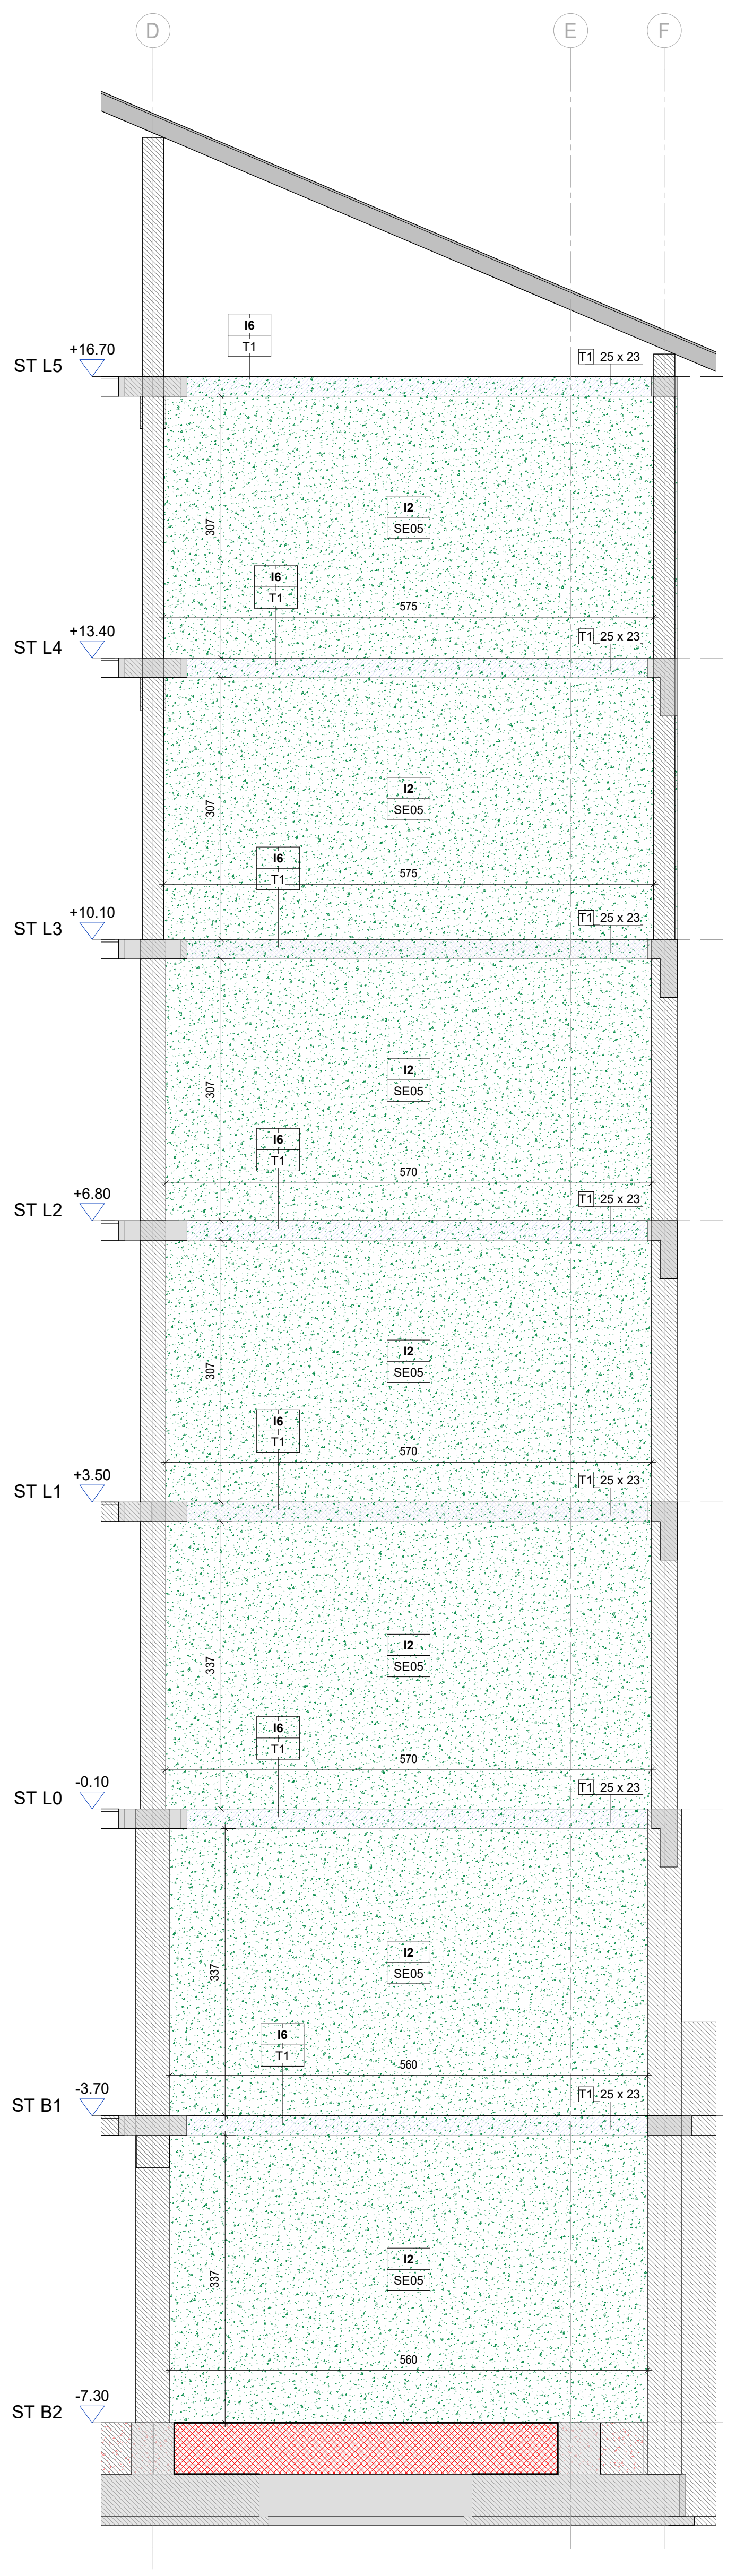

SE05-1
Scala 1 : 50

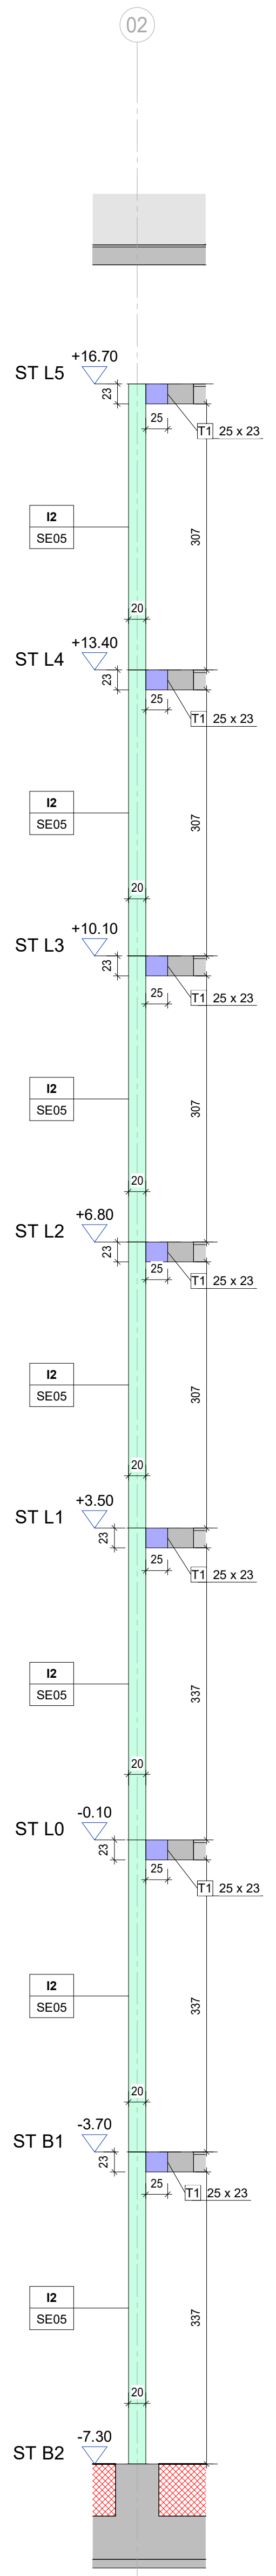

SE07-SE08
Scala 1 : 50

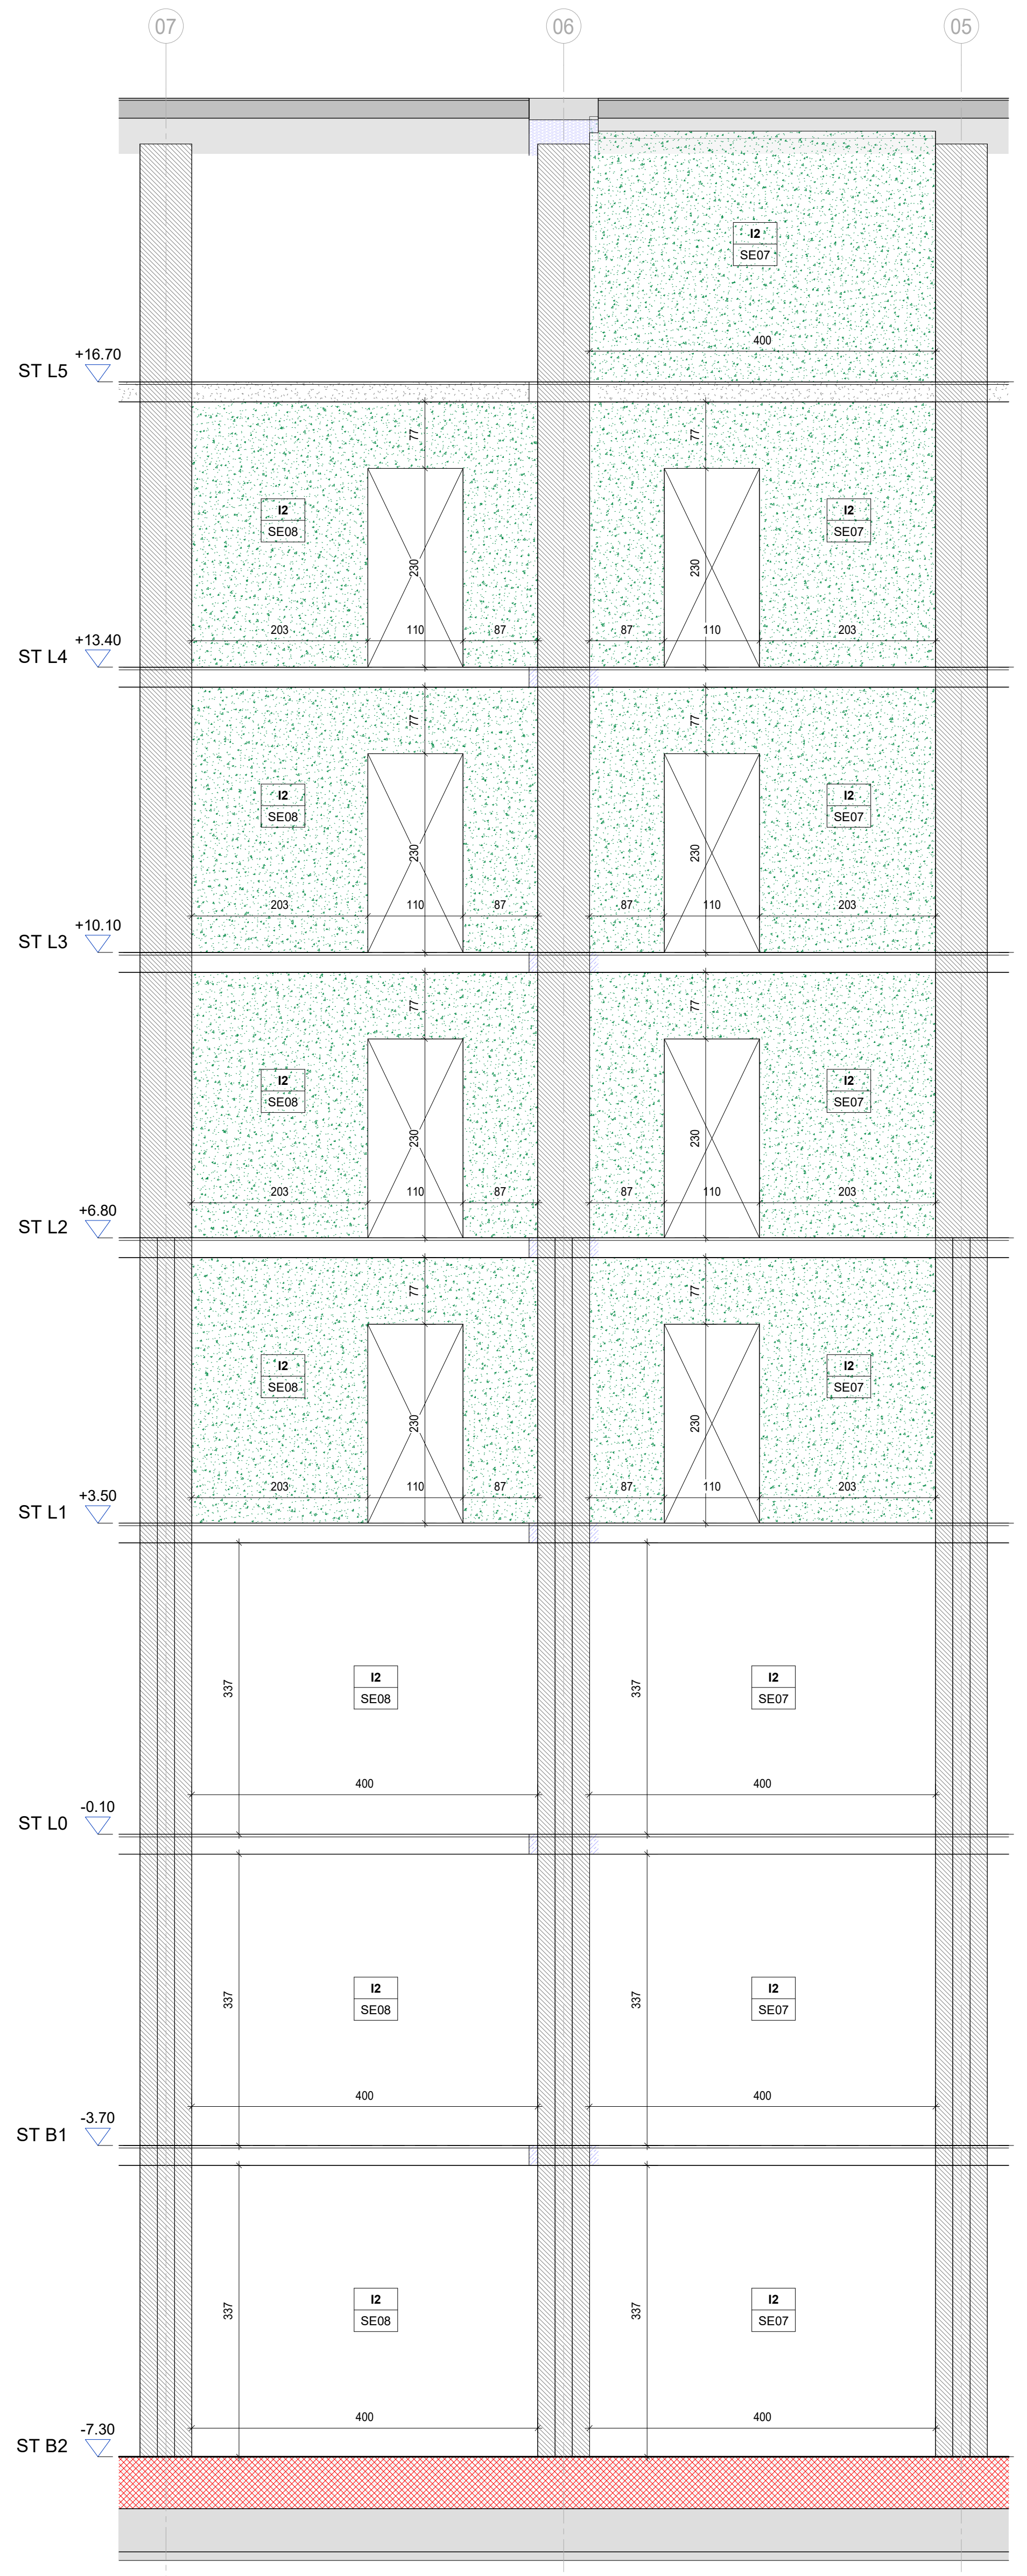

SE07-1
Scala 1 : 50

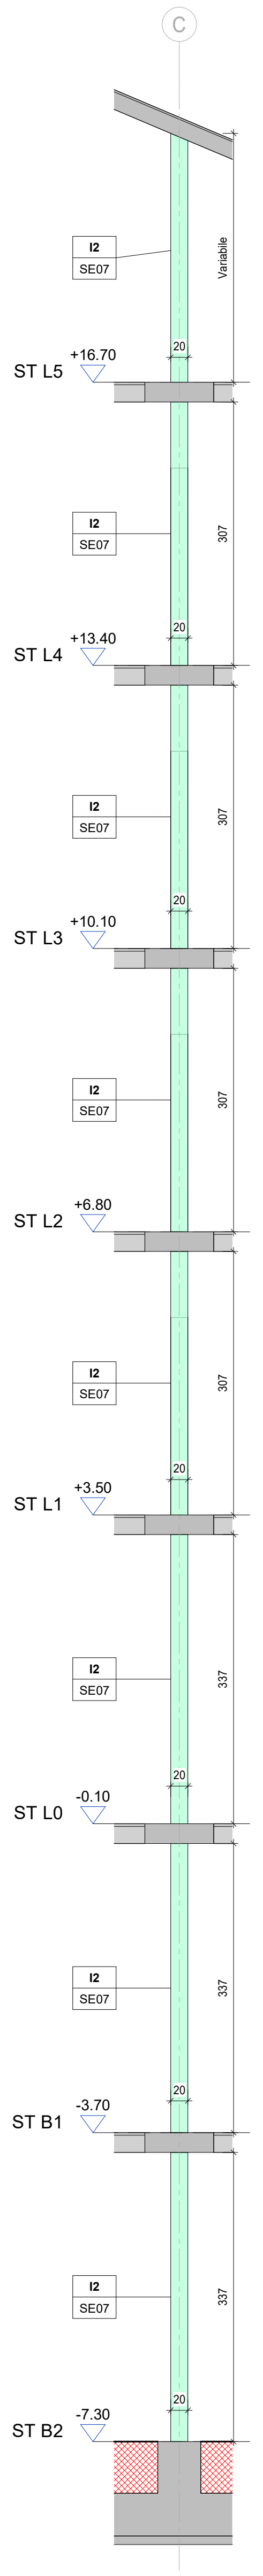

SE08-1
Scala 1 : 50

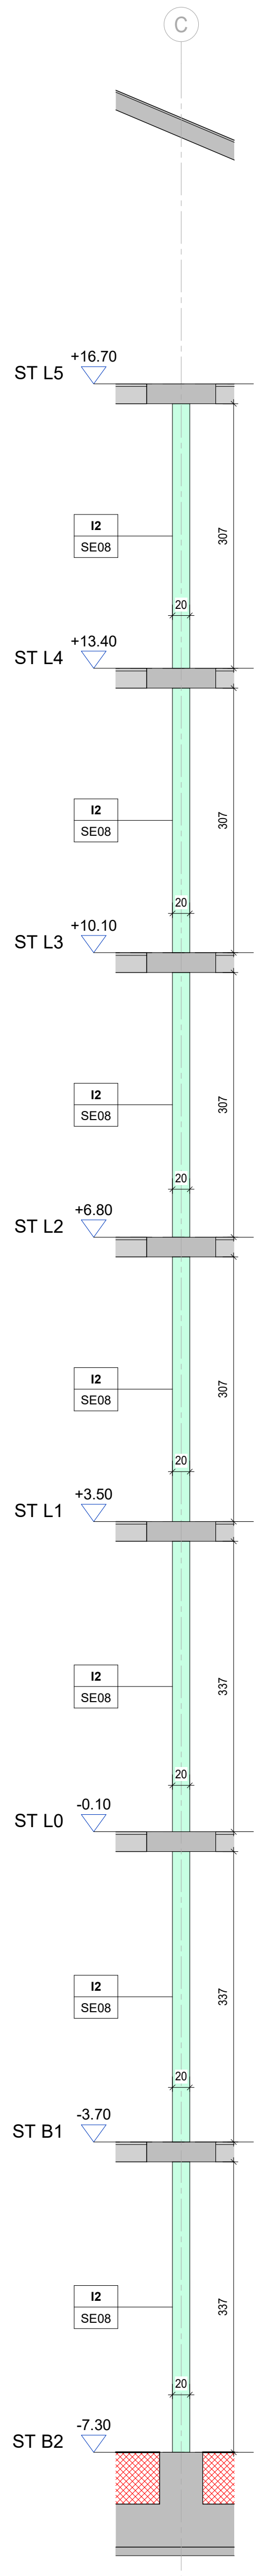

SE06-SE11
Scala 1 : 50

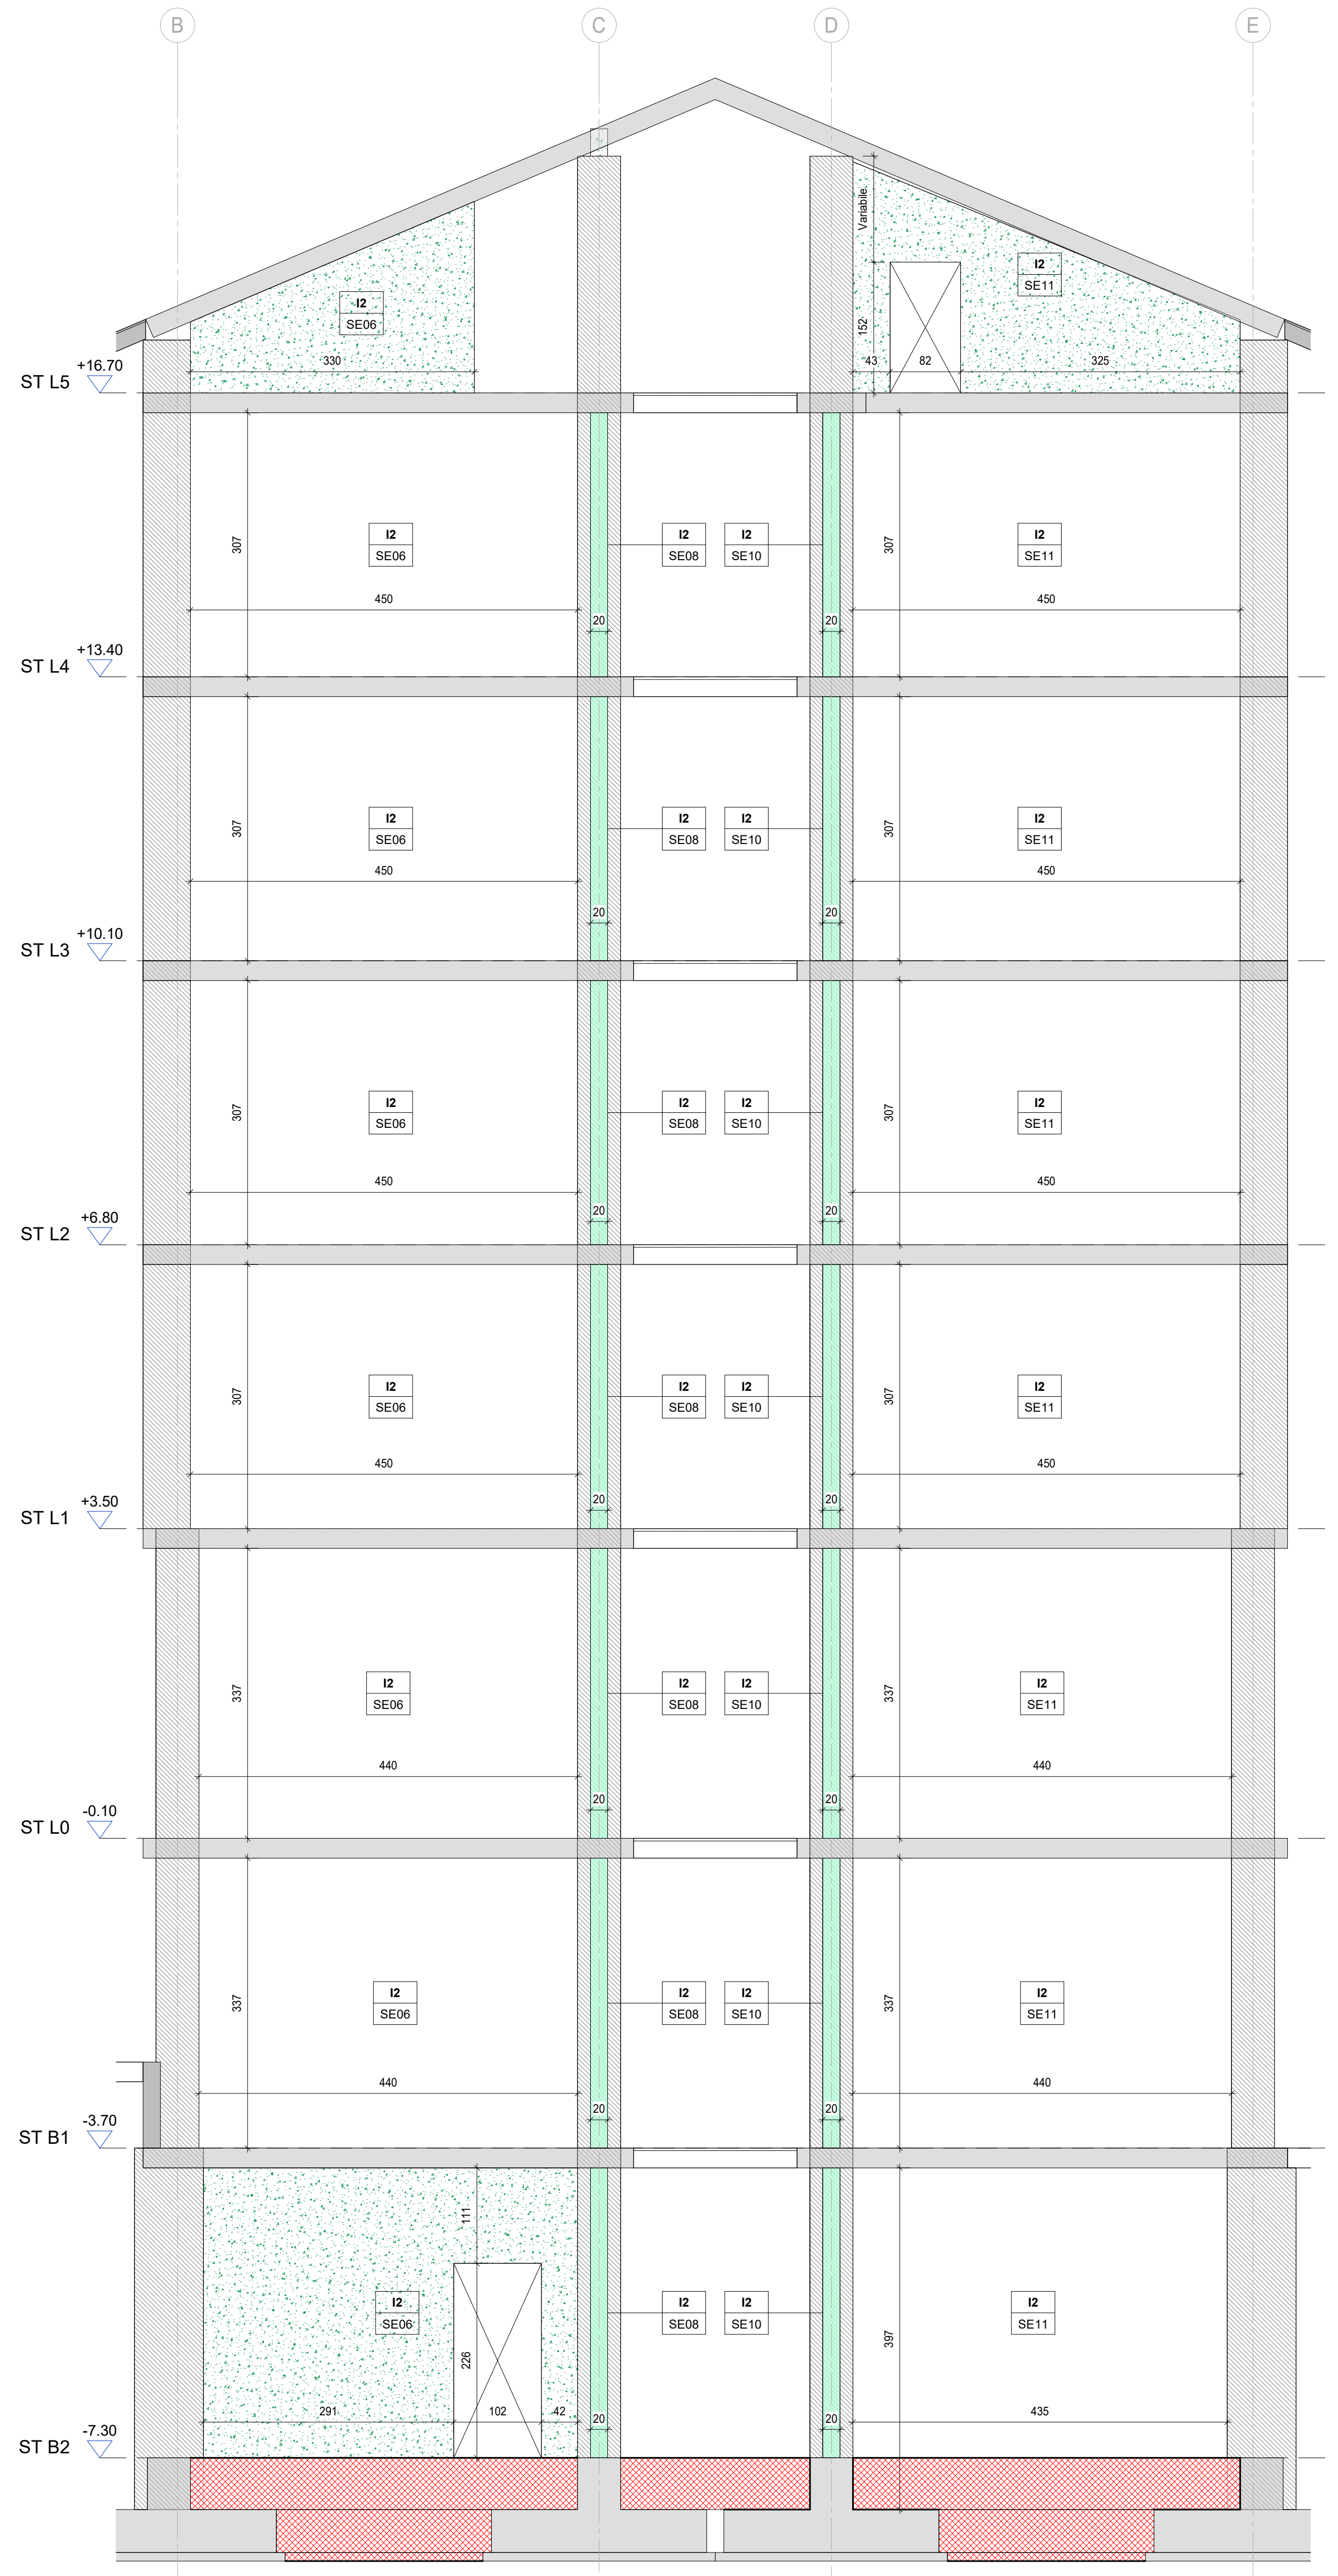

SE06-1
Scala 1 : 50

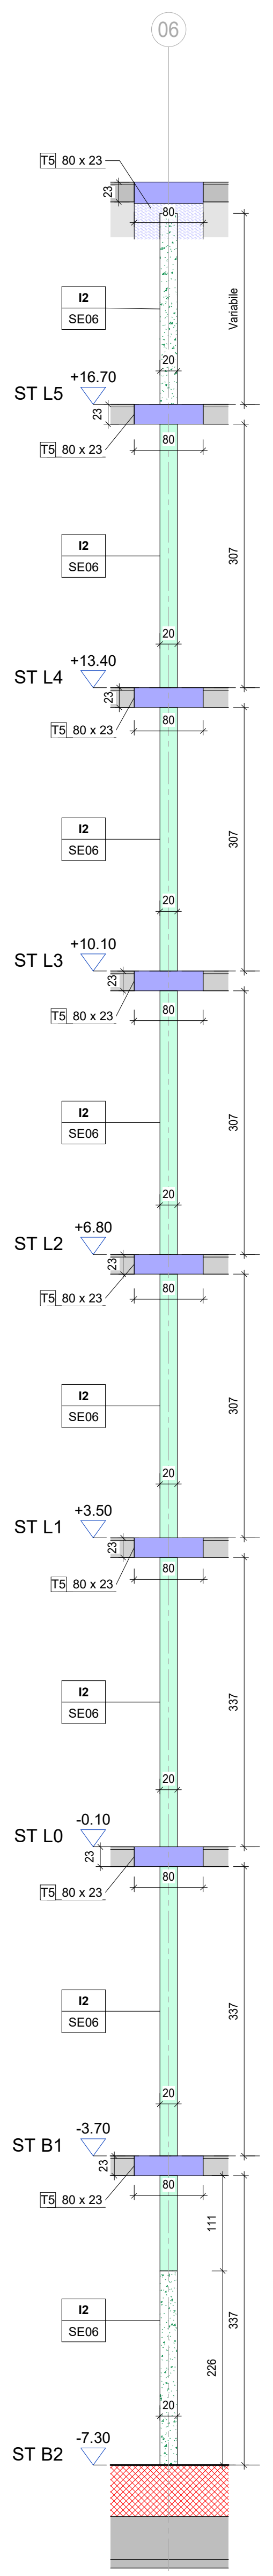

SE11-1
Scala 1 : 50

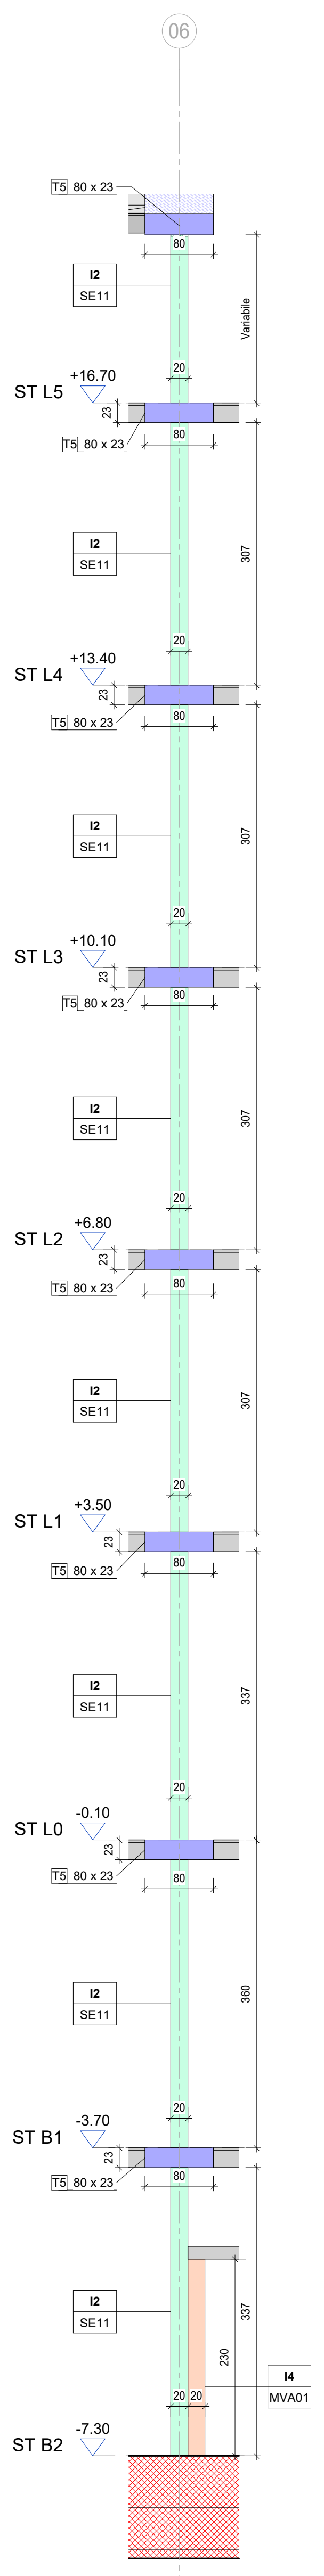

Key-Plan Setti
Scala 1 : 600

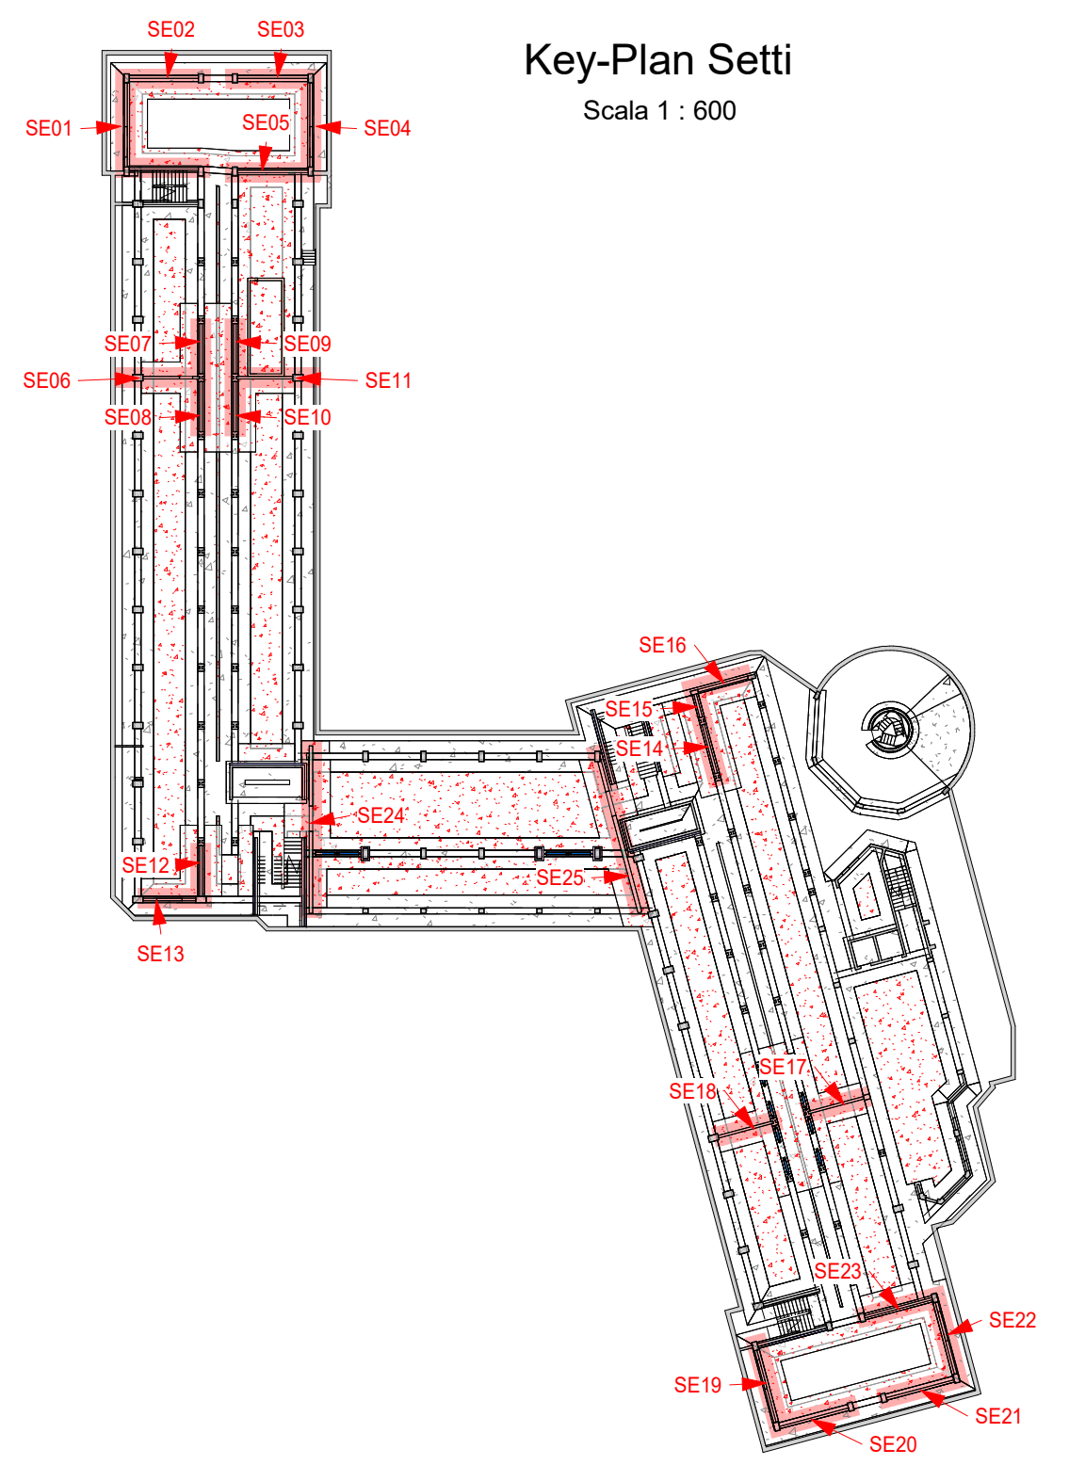

Pianta SE05
Scala 1 : 50

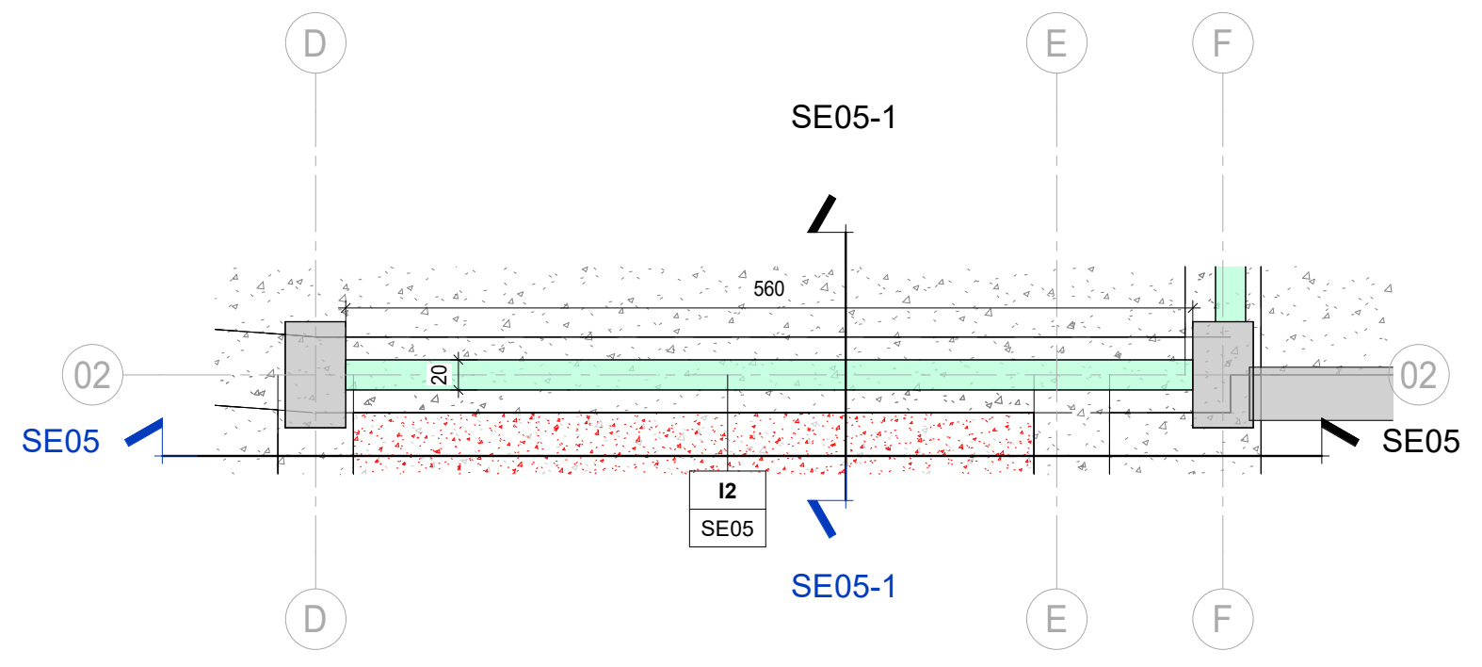

Pianta SE07-SE08
Scala 1 : 50

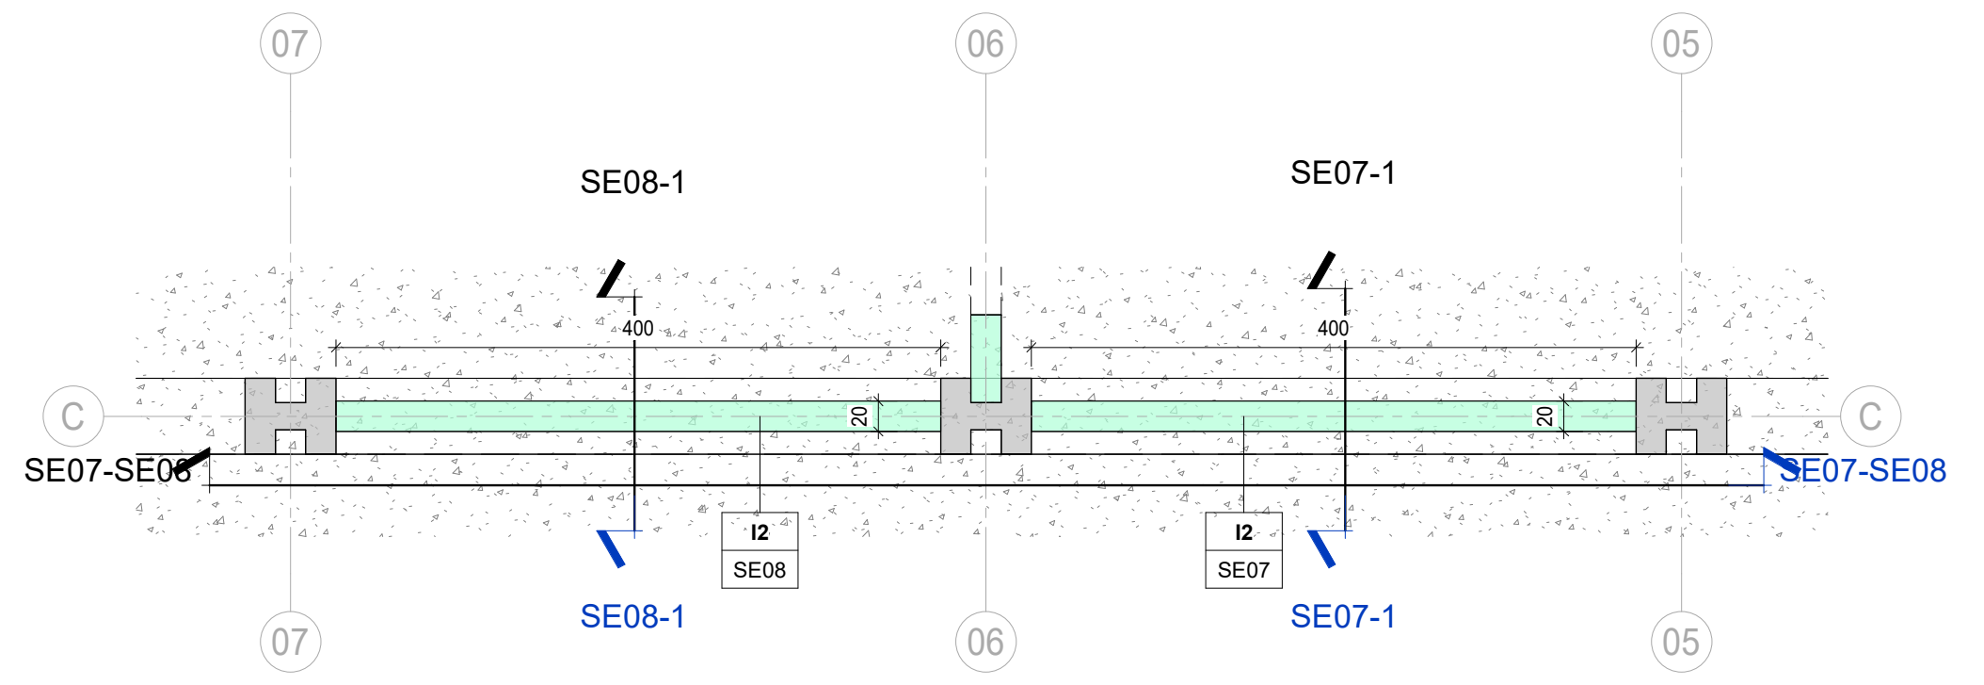

Pianta SE06-SE11
Scala 1 : 50

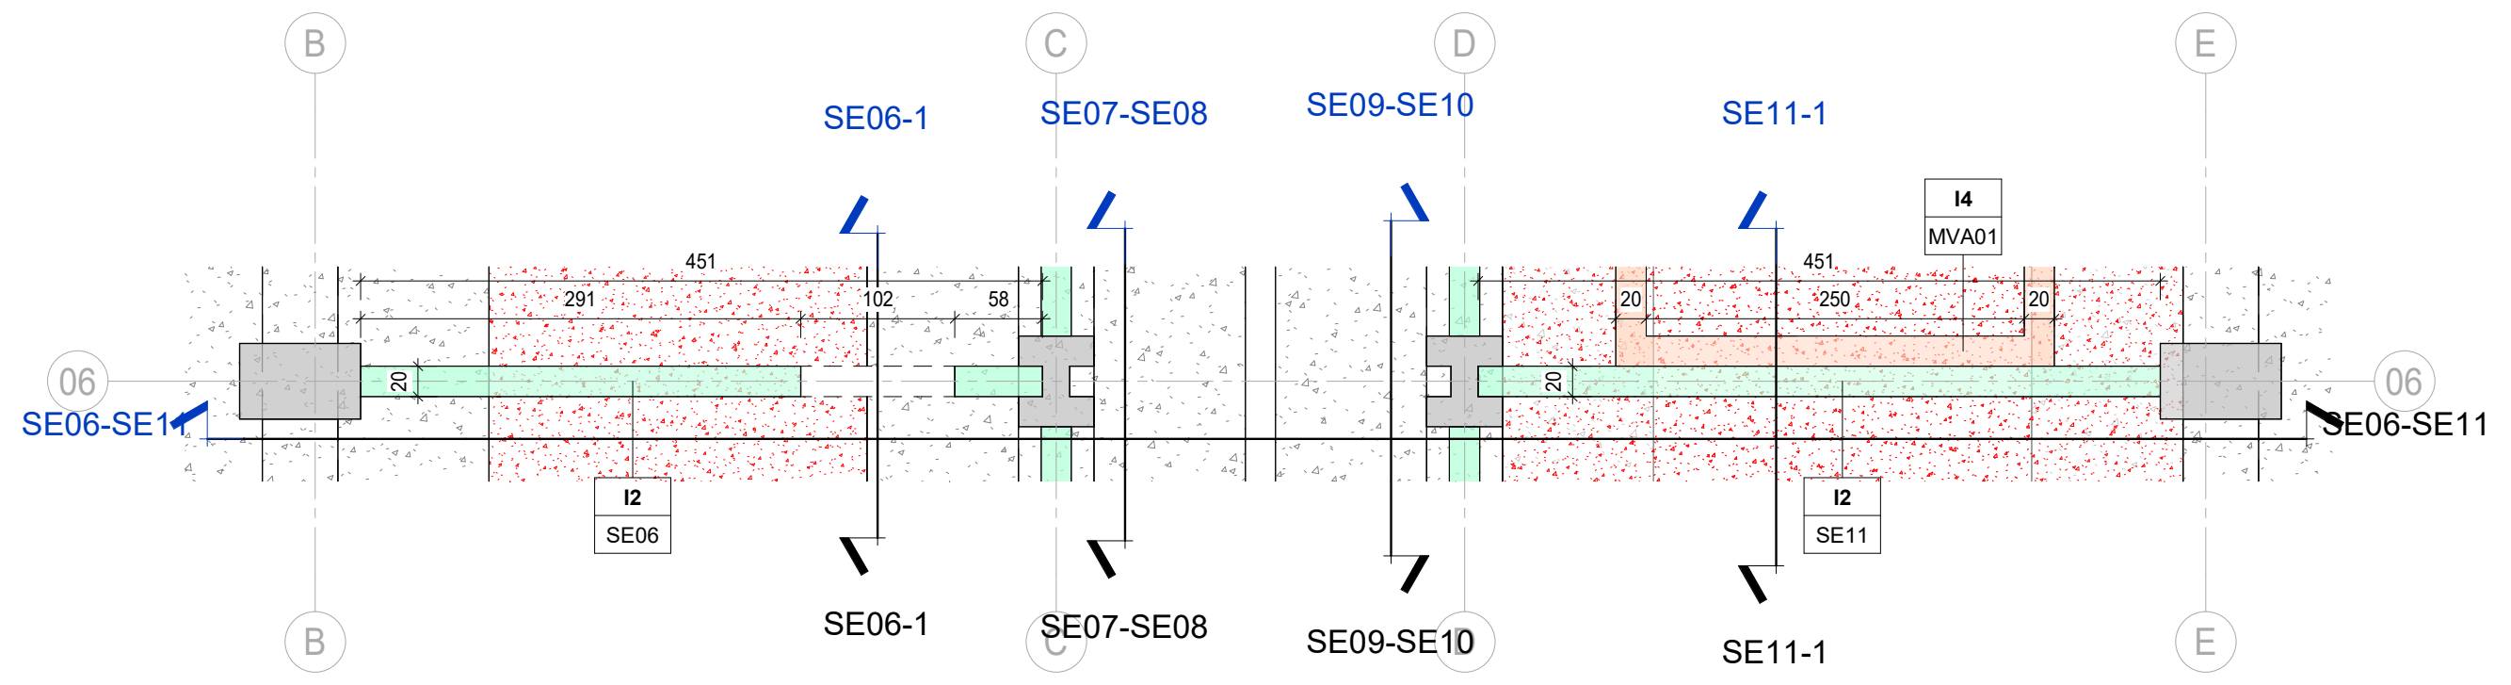

NODI BULLONATI

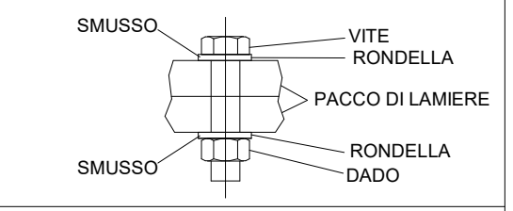

INGHISAGGI CHIMICI

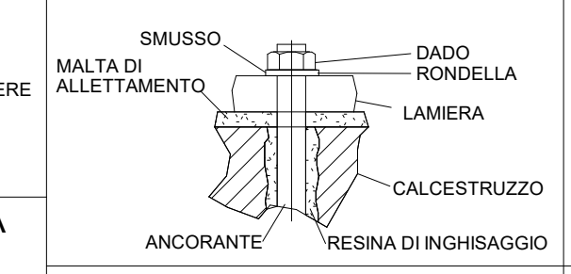

BULLONI
classe 8.8

∅ BULL	12	14	16	20	24
∅ FORO	13.0	15.0	17.0	21.0	25.5
COPPIE SERR.[N*m]	conforme vigente normativa				
SIMBOLO	●	¤	◐	⊕	◑

ACCIAIO PER CARPENTERIA METALLICA

- Carpenteria metallica: S275JR zincato
- Zincatura a caldo
- Zincatura a freddo nelle zone di saldatura in opera
- Inghisaggi chimici:
  Connessioni certificate C2 con resina TIPO HILTI HIT RE500 V4 e barre filettate classe 8.8

SALDATURA A CORDONE D'ANGOLO
(OVE NON ALTRIMENTI INDICATO)

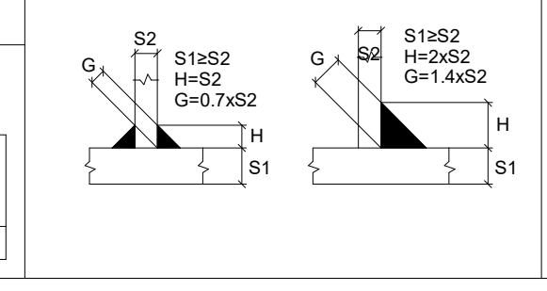

SALDATURA DI PRIMA CLASSE PER GIUNTO a "T" A COMPLETA PENETRAZIONE
(PER TUTTE LE FLANGE OVE NON ALTRIMENTI INDICATO)

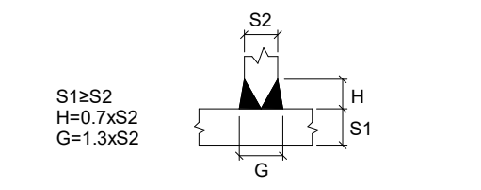

CLASSE DI ESECUZIONE SECONDO UNIEN1090

Classe di conseguenza	CC3
Categoria di servizio	SC1
Categoria di produzione	PC2
Classe di esecuzione	EXC3

- LE STRUTTURE METALLICHE DOVRANNO AVERE LE CONTROFRECCE DI MONTAGGIO OVE PREVISTO

PARTICOLARE GANCI

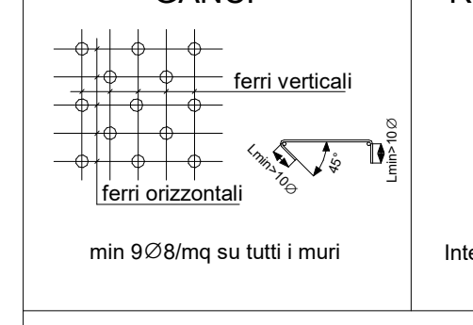

min 9∅8/mq su tutti i muri

PARTICOLARE RIPRESA DI GETTO VERTICALE

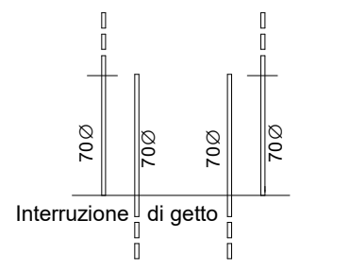

Interruzione di getto

PARTICOLARE SOVRAPPOSIZIONI

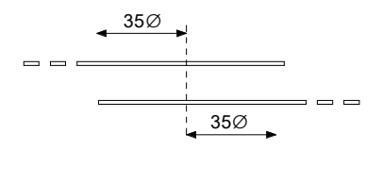

Sovrapposizione di reti elettrosaldate minimo due maglie

PARTICOLARE CHIUSURA DELLE GABBIE

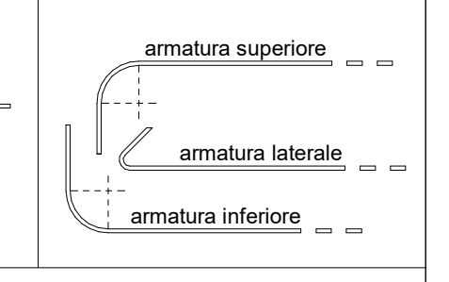

SPECIFICA COPRIFERRO/QUOTATURA

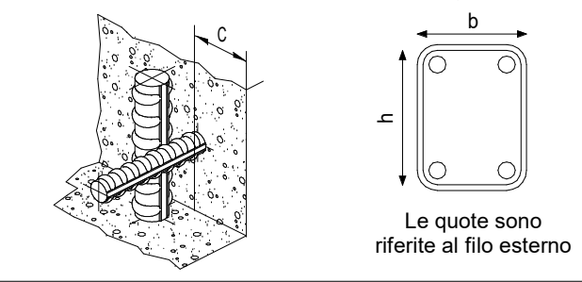

Le quote sono riferite al filo esterno

SCHEMA PIEGATURE

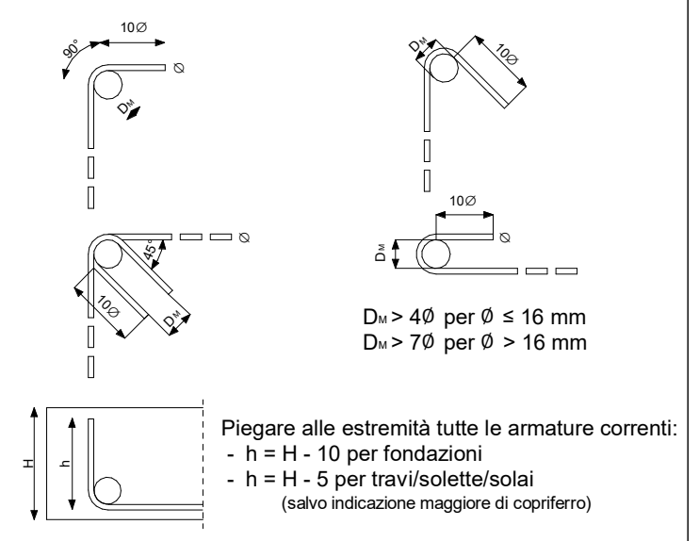

$D_M > 4\varnothing$ per $\varnothing \le 16$ mm
$D_M > 7\varnothing$ per $\varnothing > 16$ mm

Piegare alle estremità tutte le armature correnti:
- h = H - 10 per fondazioni
- h = H - 5 per travi/solette/solai
(salvo indicazione maggiore di copriferro)

CALCESTRUZZO

Calcestruzzo per	Magrone	Fondazione	Orizzontale	Strutture in elevazione
Classe di resistenza (Fck/Rck)	C12/15	C28/35	C35/45	C35/45
Classe esposizione ambientale	-	XC2	XC2	XC2
Cemento tipo	42.5N	42.5N	42.5N	42.5N
Rapporto max acqua/cemento	CONFORME ALLA NORMATIVA VIGENTE			
Contenuto min. cemento (kg/m³)				
Ø max inerti (mm)	-	16	16	16
Classe di consistenza	-	S4	S5	SCC
Copriferro netto (mm)	-	40	30	30
Copriferro netto controterra	≥ 40 mm			
Profondità permeazione acqua secondo ISO7031	< 20 mm			

ACCIAIO PER CEMENTO ARMATO

ACCIAIO TIPO B450C controllato in stabilimento e saldabile

PRESCRIZIONI NOTE GENERALI

- VERIFICARE TUTTE LE MISURE IN CANTIERE PRIMA DI EFFETTUARE L'ORDINATIVO DEI MATERIALI
- VERIFICARE TUTTE LE MISURE E I FORI CON IL PROGETTO ARCHITETTONICO E IMPIANTISTICO
- OVE PREVISTI FIORETTI INGHISATI CON RESINA E TASSELLI CHIMICI DOVRANNO ESSERE POSTI IN OPERA SECONDO LE PRESCRIZIONI DEL PRODUTTORE DELLE RESINE NELLE CONDIZIONI AMBIENTALI IDONEE E PREVIA PERFETTA PULIZIA DEL FORO
-IN SEGUITO ALLO STRIP-OUT VERIFICARE GEOMETRIA E DIMENSIONI DELLE STRUTTURE INTERESSATE DAGLI INTERVENTI IN CANTIERE
-VERIFICA PREVENTIVAMENTE LA STABILITA' DELLE STRUTTURE ESISTENTI E LE FASI OPERATIVE PRIMA DI DEMOLIRE
-PER LE DEMOLIZONI DEI SOLAI PROCEDERE PER AREE LIMITATE VERIFICANDONE LA STABILITA' PRIMA DI PROCEDERE IN ALTRE ZONE
-PER LE DEMOLIZIONI PREVEDERE OPPORTUNE OPERE PROVVISONALI E PUNTELLAZIONE

CUP F18H22000220005 - CIG 9210532374

UNIVERSITA' DEGLI STUDI DI BERGAMO
EX CASERMA GUARDIA DI FINANZA

Progetto di investimento relativo all'intervento di ristrutturazione e rifunzionalizzazione del complesso immobiliare di Via dello Statuto, n. 21 - Bergamo - Corpo C) - "Residenze"

PROGETTO ESECUTIVO

COMMITTENZA
Università degli studi di Bergamo
Area Infrastrutture - Settore Infrastrutture
via Salvecchio 19, 24129 Bergamo

RESPONSABILE UNICO DEL PROCEDIMENTO
Ing. Marta Sabbatini

RTP DI PROGETTAZIONE

CAPOGRUPPO MANDATARIA

Studio Altieri S.p.A.
Coordinamento progettuale ed integrazioni specialistiche, progettazione edile-architettonica e coordinamento della sicurezza in fase di progettazione

Responsabile integrazione tra le prestazioni specialistiche & PM
Ing. Alessandro Artuso

Project Coordinator & CDE Manager (Giovane professionista)
Ing. Filippo Bee

Esperto in sistemi edilizi
Ing. Andrea Sbalchiero

BIM Manager
Geom. Marika Riccobene

Progettazione ambientale
Ing. Laura Dalla Valle

Progettazione architettonica
Arch. Andrea Chiarolini
Arch. Laura Von Dellemann

Coordinatore della Sicurezza in fase di Progettazione
Geom. Moreno Gazzetto

MANDANTI

ICONIA Ingegneria Civile S.r.l.

Progettazione strutturale
Ing. Romj Friso
Ing. Domenico D'Anza

Energo S.r.l.

Responsabile progettazione impianti meccanici, elettrici, idrico sanitari
Certificazione energetica
Professionista antincendio
Arch. Denis Zuin

Dott. Geol. Paolo Cornale Geologo

TITOLO DEL DOCUMENTO: STRUTTURE
NUOVI SETTI-DETTAGLI CARPENTERIA 2 DI 6

SCALA: VAR

CODICE:

C1088	E	ST	DET	00	101	r00
Commessa	Fase	Disciplina	Set	Livello	Numero	Revisione

Revisione	Data	Motivo	Redatto	Controllato	Approvato
00	19/10/2026	Prima emissione	RM	MG	DD